

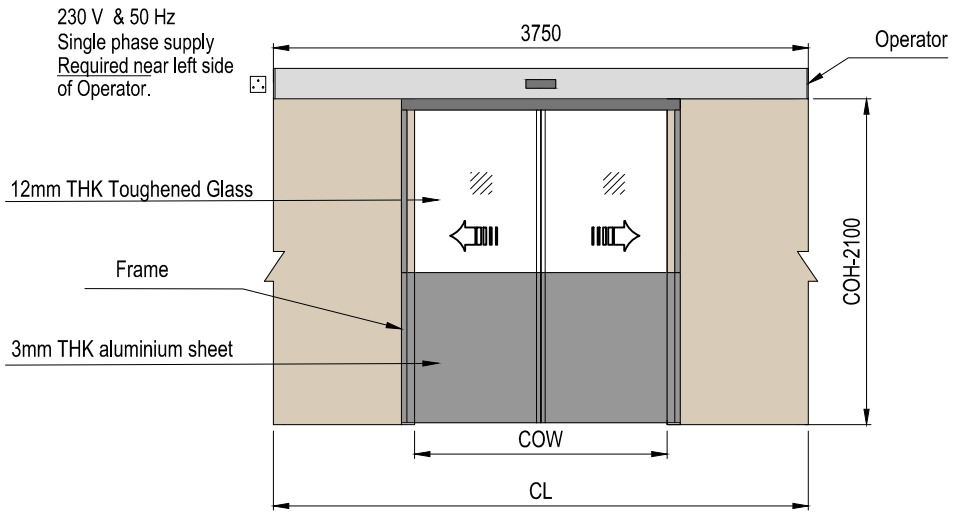


Inside Elevation

Fixing Plan

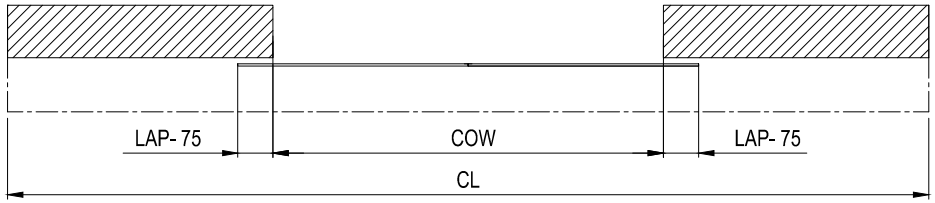


Closed Condition

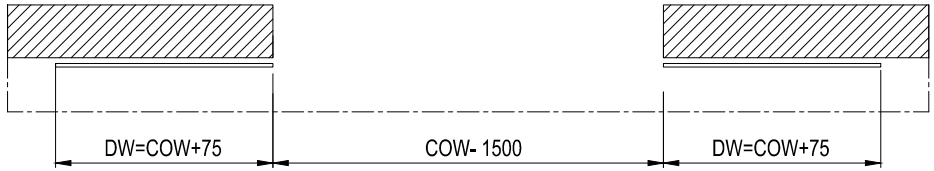

Open Condition

Plan

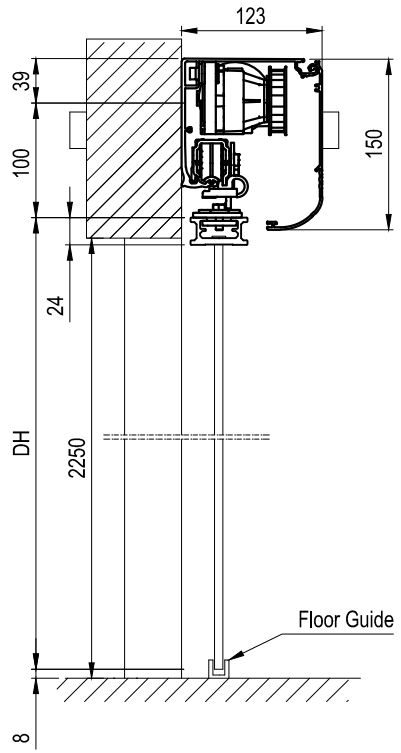

Door Size			
Sr. No.	Clear Width (COW)	Clear Height (COH)	Quantity
1	1500	2100	2
2	1400	2100	1
3	1300	2100	1
4	1200	2100	2

Glass Type- 12mm Toughened

This drawing & designing is the property of NIHVA TECHNOLOGIES. Not to be sold or copied to any other concern.

TITLE: AUTOMATIC SLIDING GLASS DOOR

NIHVA TECHNOLOGIES PVT. LTD. PUNE
Tel : 020 66304033
Email:- info@nihva.com
Website:- www.nihva.com

	NAME	SIGN	DATE
DRAWN	SURAJ		01/06/18
CHECK	SHAILENDRA		01/06/18
APPROVAL	PRADEEP		01/06/18

CLIENT - SHIMIZU
PROJECT -TRMN
SITE - BENGALURU,KARNATAKA.

If any queries contact : design@nihva.com
DWG. NO. : NIHVA/18-19/0049. REV.- 0
ALL DIMENSION ARE IN mm
SCALE: NTS WT: SHEET: 01 OF 01