

Abbrevation's:
WOW-Wall Opening Width
WOH-Wall Opening Height
UC-Under Cut
FFL-Finished Floor Level

ASSESORIES DETALES

(A) HINGES: SS Ball bearing butt hinges size 100x75x3mm

(B) LOCK : Mortise latch with double cylinder with Escutcheon.


(C) DOOR CLOSER : F8500

(D) VISION PANEL : 5 mm THK. VISION GLASS OF SIZE 200(W) X 300(H)mm


(E) LEVER HANDLE (BOTH SIDE)

Shutter thickness : 47 mm
Frame Sheet thick : 1.20mm
Shutter sheet thick : 0.80mm
Fixing : On Solid Brick plastered wall with Anchors


NOTE:- *All Dimensions are in mm.
*Tolerance:-All Linear Dimensions ±3mm,Others ±0.5mm.
*The Drawing Is For Location of Hardware only. Drawing Does Not Represent The Hardware For More Clarity, Please Go Through Hardware Broucher.

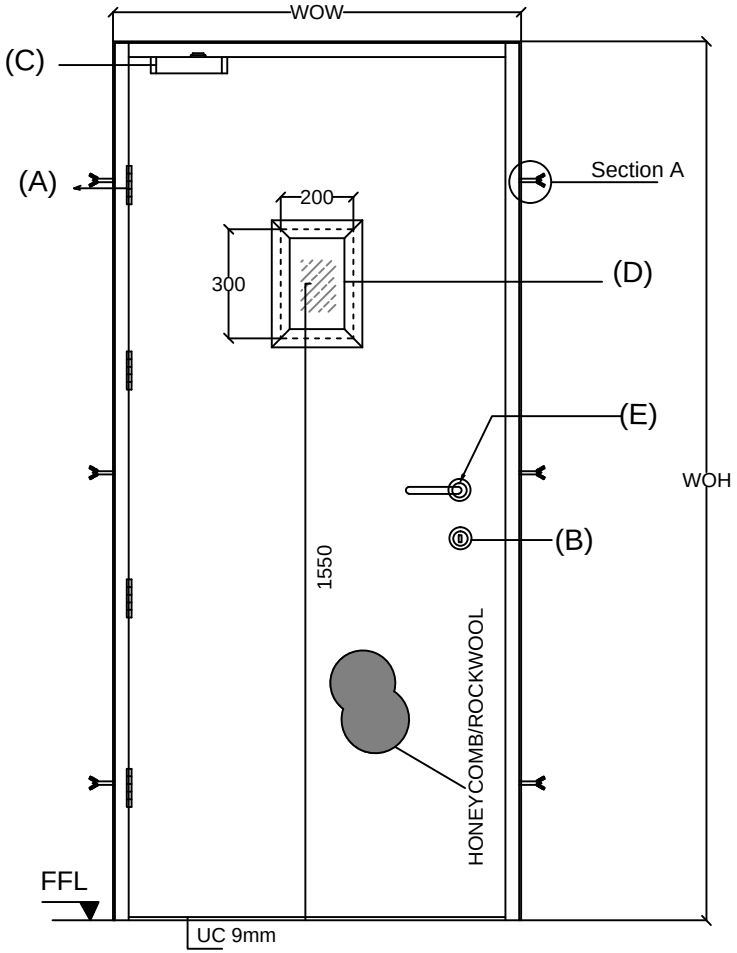

OUTSIDE ELEVATION

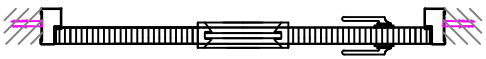

TOP VIEW

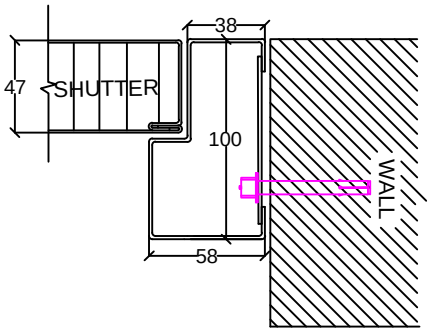

Detail view of Section A

FIRE RATED STEEL DOOR					
SR. NO.	WOW	WOH	TYPE 3	QUANTITY	LOCATION
1	1030	2080	1	1	PUMP ROOM

NOTE- 1.CLIENT SHOULD MENTION COLOR FOR DOOR.
2.CLIENT SHOULD CHECK DOOR ORIENTATION & APPROVE THE SAME.

COLOR
1.TRAFFIC WHITE (RAL 9016)
2.LIGHT GREY (RAL 7035)
3.GENTION BLUE (RAL 5010)
4.SIGNAL RED (RAL 3001)

REVISION 1- QUANTITY OF DOORS HAS BEEN REVISED.

This drawing & design is the property of NIHVA TECHNOLOGIES. Not be sold or copy to any other concern.

FIRE RATED STEEL DOOR (SINGLE LEAF)

CLIENT APPROVAL

ALL DIMENSION ARE IN mm

	NAME	DATE	SIGN.
DRAWN BY	SURAJ	24/04/17	
CHECK BY	SAGAR P.	24/04/17	
REV.	1		
APPROVED BY	R.K.	24/04/17	
MFG			

NIHVA TECHNOLOGIES PVT. LTD.
NIHVA TECHNOLOGIES PVT. LTD. PUNE
Tel : 020 66304033
Email:- info@nihva.com
Website:-www.nihva.com

CLIENT - MUKUND CONSTRUCTION
PROJECT -
SITE -
DWG. NO. - NIHVA/17-18/0021/R01
SCALE: NTS | WT: | SHEET: 01 OF 01
If any queries contact : projects@nihva.com