

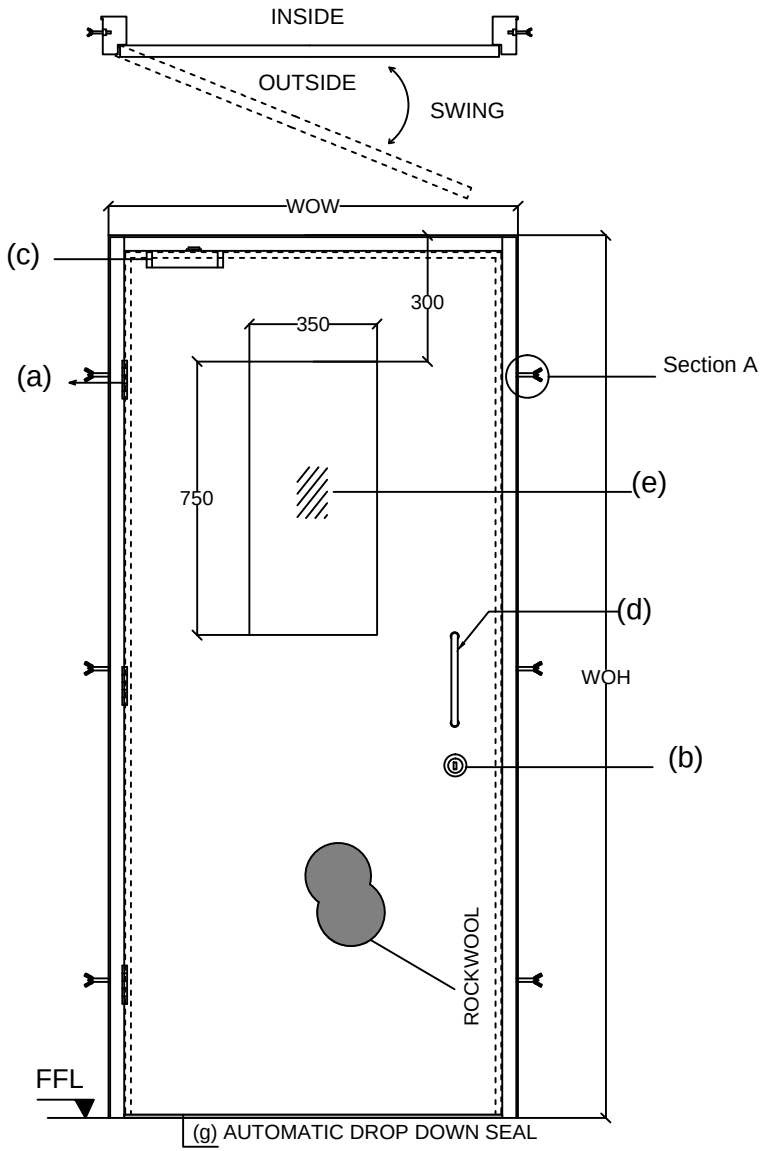


ELEVATION

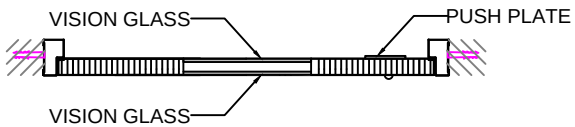

TOP VIEW

Abbreviation's:
WOW-Wall Opening Width
WOH-Wall Opening Height
FFL-Finished Floor Level

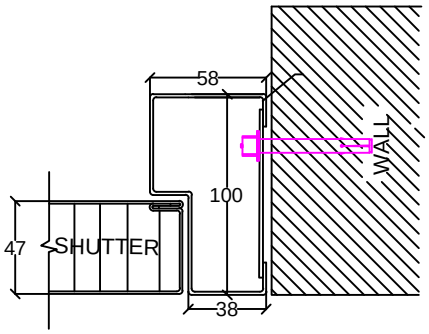

Section A

ASSESORIES DETALES

(a) HINGES: SS Ball bearing butt hinges size 100x75x3mm

(b) LOCK : Mortise Dead lock,Cylinder(Both side key) with Escutcheon

(c) DOOR CLOSER: 1 No. Door Closer

(d) HANDLE : SS D HANDLE(254mm) (D HANDLE FROM OUTSIDE& SS PUSH PLATE FROM INSIDE.)

(e) VISION PANEL- FRAME LESS VISION PANEL OF DOUBLE GLASS SHEET OF SIZE 350X750mm.

(g) AUTOMATIC DROP DOWN SEAL

Shutter thickness : 47 mm
Frame Sheet thick : 1.20mm
Shutter sheet thick : 0.80mm
Fixing : On Soliid Brick plasterd wall with Anchors

NOTE:- *All Dimensions are in mm.
*Tolerance:-All Linear Dimensions ±3mm,Others ±0.5mm.
*The Drawing Is For Location of Hardware only. Drawing Does Not Represent The Hardware For More Clarity, Please Go Through Hardware Broucher.

Steel door size

WOW	WOH	QUANTITY
1200	2150	1

ORIENTATION- TYPE 3 LEFT HAND REVERSE
COLOR:- Sapphire Blue(RAL 5003)

This drawing & designing is the property of NIHVA TECHNOLOGIES. Not be sold or copy to any other concern.

SINGLE LEAF STEEL DOOR

CLIENT APPROVAL

ALL DIMENSION ARE IN mm

	NAME	DATE	SIGN.
DRAWN	OMKAR	14/09/16	
CHECK	ANIL	14/09/16	
REV.	0		
APPRD.			
MFG			

NIHVA TECHNOLOGIES PVT. LTD.
NIHVA TECHNOLOGY PVT. LTD. PUNE
Tel : 020 66304033
Email:- info@nihva.com
Website:-www.nihva.com

CLIENT - MARS INTERNATIONAL
PROJECT -
SITE - KHED CITY
DWG. NO. - NIHVA/16-17/0075
SCALE: NTS | WT: | SHEET: 01 OF 01
If any queries contact : projects@nihva.com