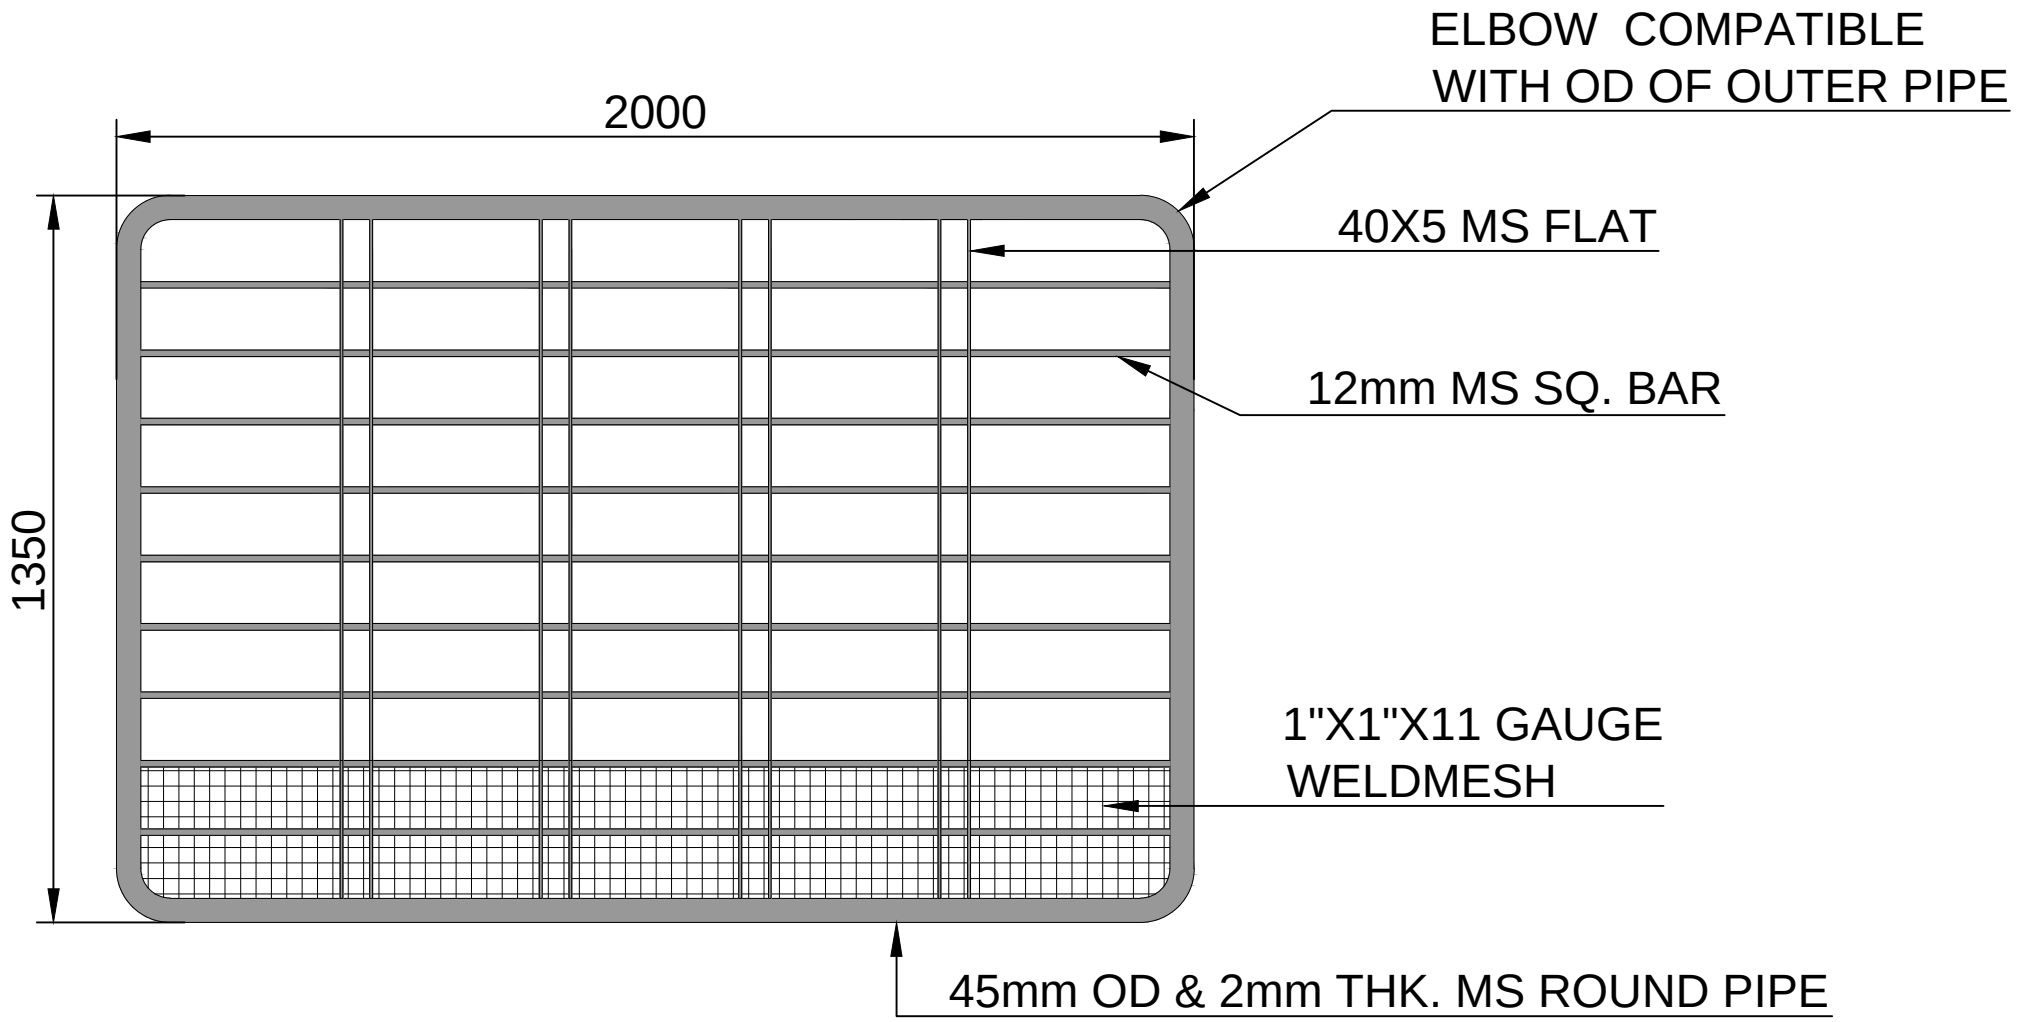
2000
1350
ELBOW COMPATIBLE
WITH OD OF OUTER PIPE
40X5 MS FLAT
12mm MS SQ. BAR
1"X1"X11 GAUGE
WELDMESH
45mm OD & 2mm THK. MS ROUND PIPE