




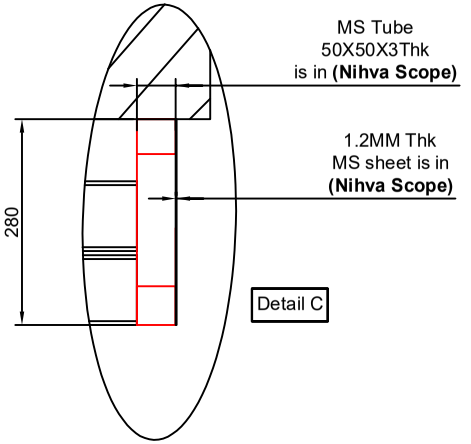


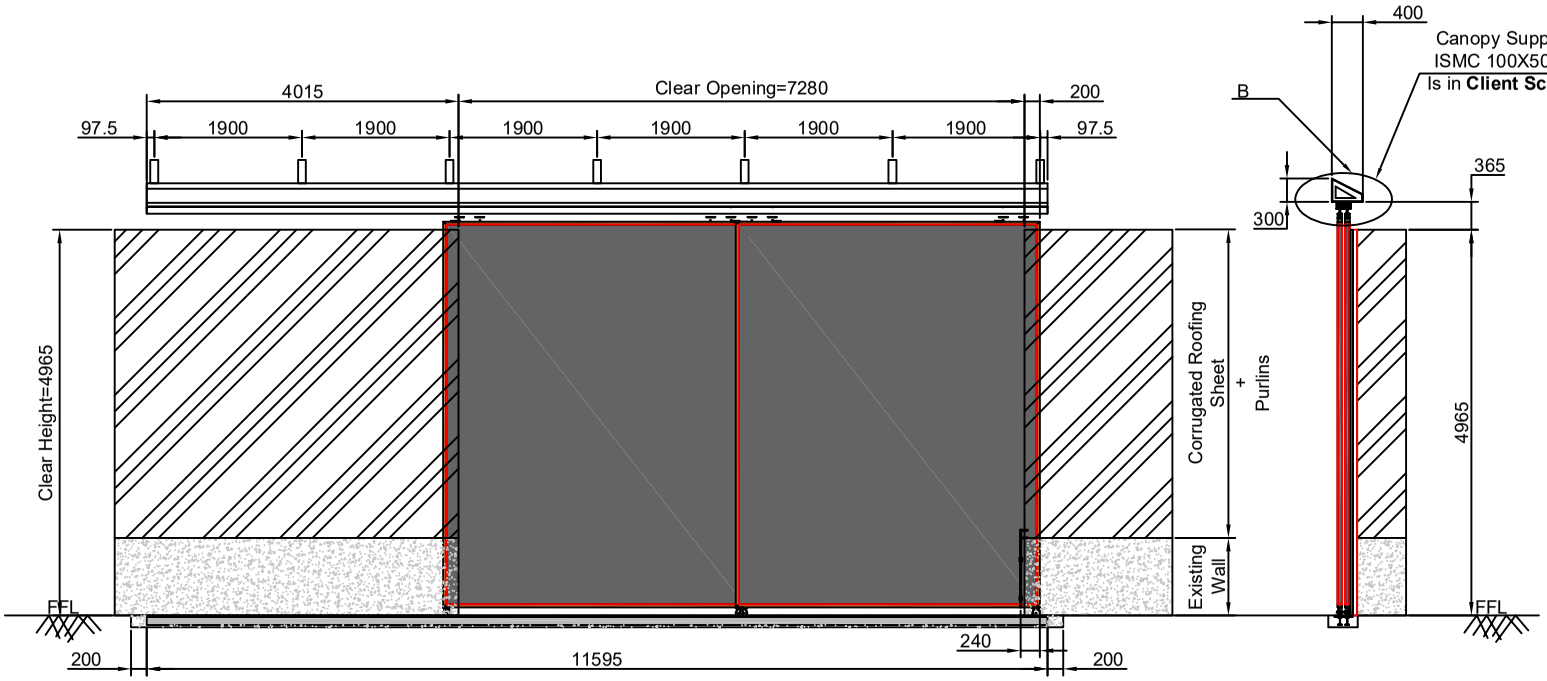

Client scope
* Roof need to be shifted by 335 mm *Civil foundation need to be done for tracks


Color code	Color
5018	Turquoise blue

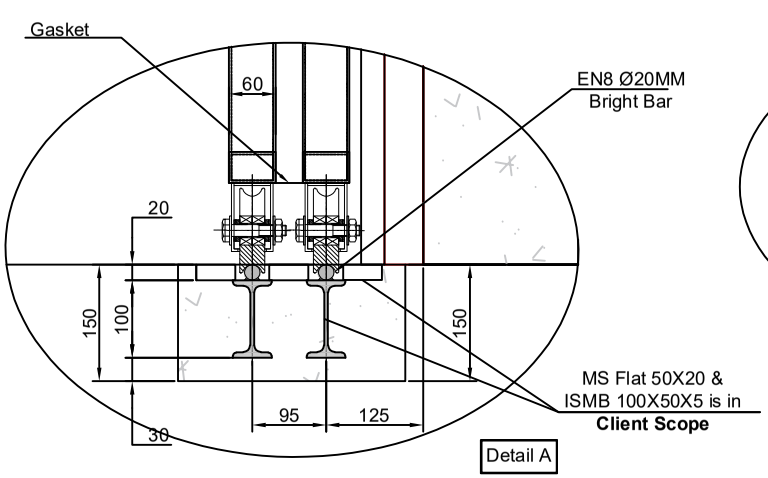

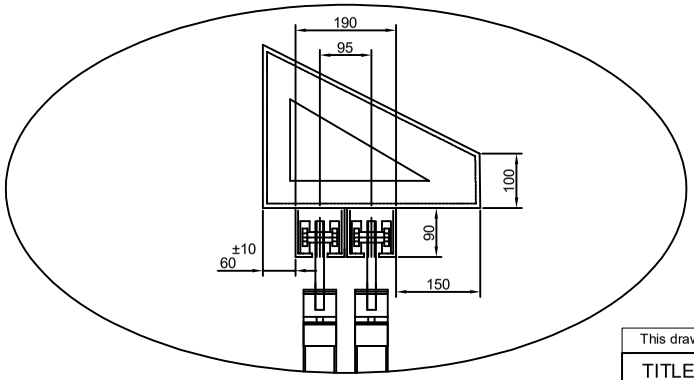

Note:--

1. All dimension are in MM
2. All Civil work will be in client scope
3. Manufacturing,civil and installation tolerance will be ±10mm
4. Top and Bottom track should be in parallal within ±3mm
5. Nihva Supervisor on site for Monitoring/Checking of civil work

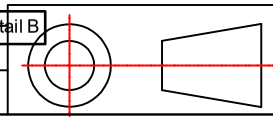

Rev No.	Revision	Date	Revised By

This drawing & design is the property of NIHVA TECHNOLOGIES. Not to be sold or copied to any other concern.

TITLE:-2LEAF-LEFT SIDE CRM DOOR-12

NIHVA TECHNOLOGIES PVT. LTD.
NIHVA TECHNOLOGIES PVT. LTD. PUNE
Tel : 020 66304033
Email:- info@nihva.com
Website:- www.nihva.com

	NAME	DATE	SIGN
DRAWN	SUJATA	11/05/2022	
CHECK	M.SUTAR	11/05/2022	
APPRD.	V.TARAK	11/05/2022	

CLIENT - LESTECH
LOCATION - POSCO MANGAON
PRODUCT - SLIDING DOOR
If any queries contact : design@nihva.com
DWG NO:-NIHVA/22-23/CLT/0036
REV- 0
ALL DIMENSION ARE IN mm
SCALE: NTS
SCALE:-- 1:1
SHEET: 01 OF 01