
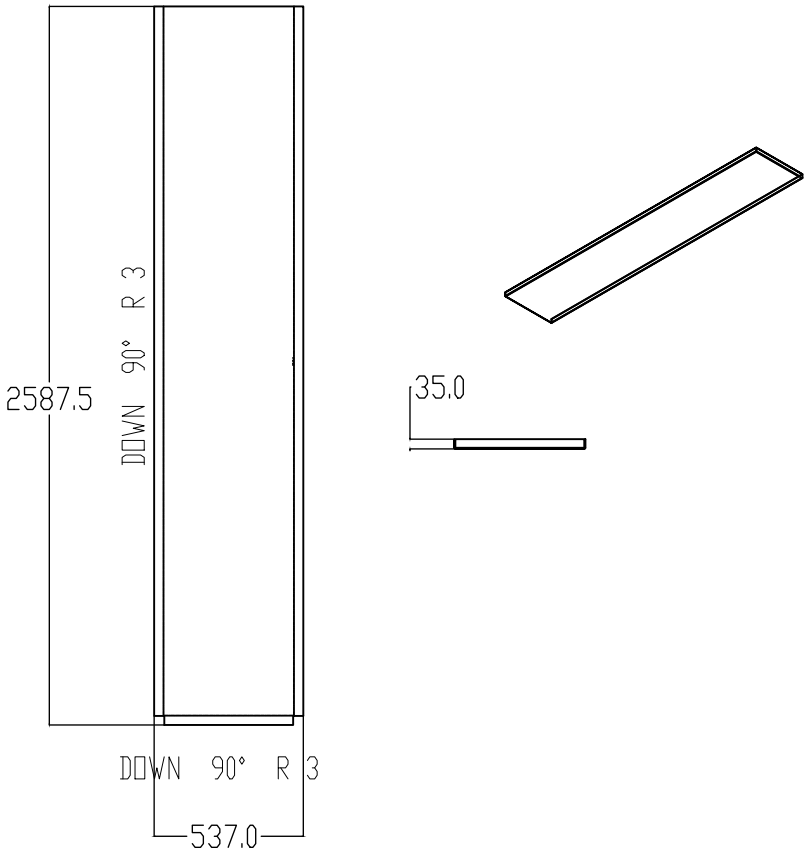


QTY=04 NOS

DOOR -01

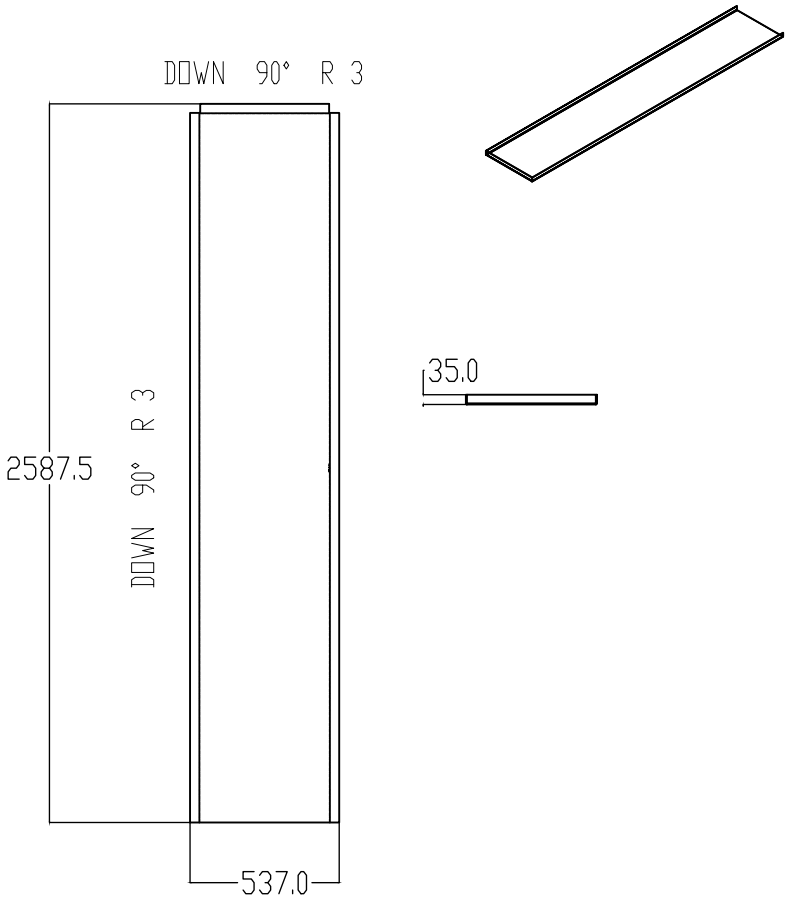

QTY=04 NOS

This drawing & design is the property of NIHVA TECHNOLOGIES. Not to be sold or copied to any other concern.

TITLE:- 4 LEAF BOTH SIDE CRM DOOR 013			NIHVA TECHNOLOGIES PVT. LTD. PUNE Tel : 020 66304033 Email:- info@nihva.com Website:- www.nihva.com
	NAME	DATE	SIGN
DRAWN	KISHAN	14/05/2022	
CHECK	M.SUTAR	14/05/2022	
APPRD.			
CLIENT - NIHVA TECHNOLOGIES			
LOCATION -			
PRODUCT - SLIDING DOOR			
If any queries contact : design@nihva.com	DWG NO:-NIHVA/22-23/MFG/0021		REV- 0
ALL DIMENSION ARE IN mm	SCALE: NTS	SCALE:-- 1:1	SHEET: 01 OF 02

	Date	Revised By