

PROPOSED PLAN LAYOUT

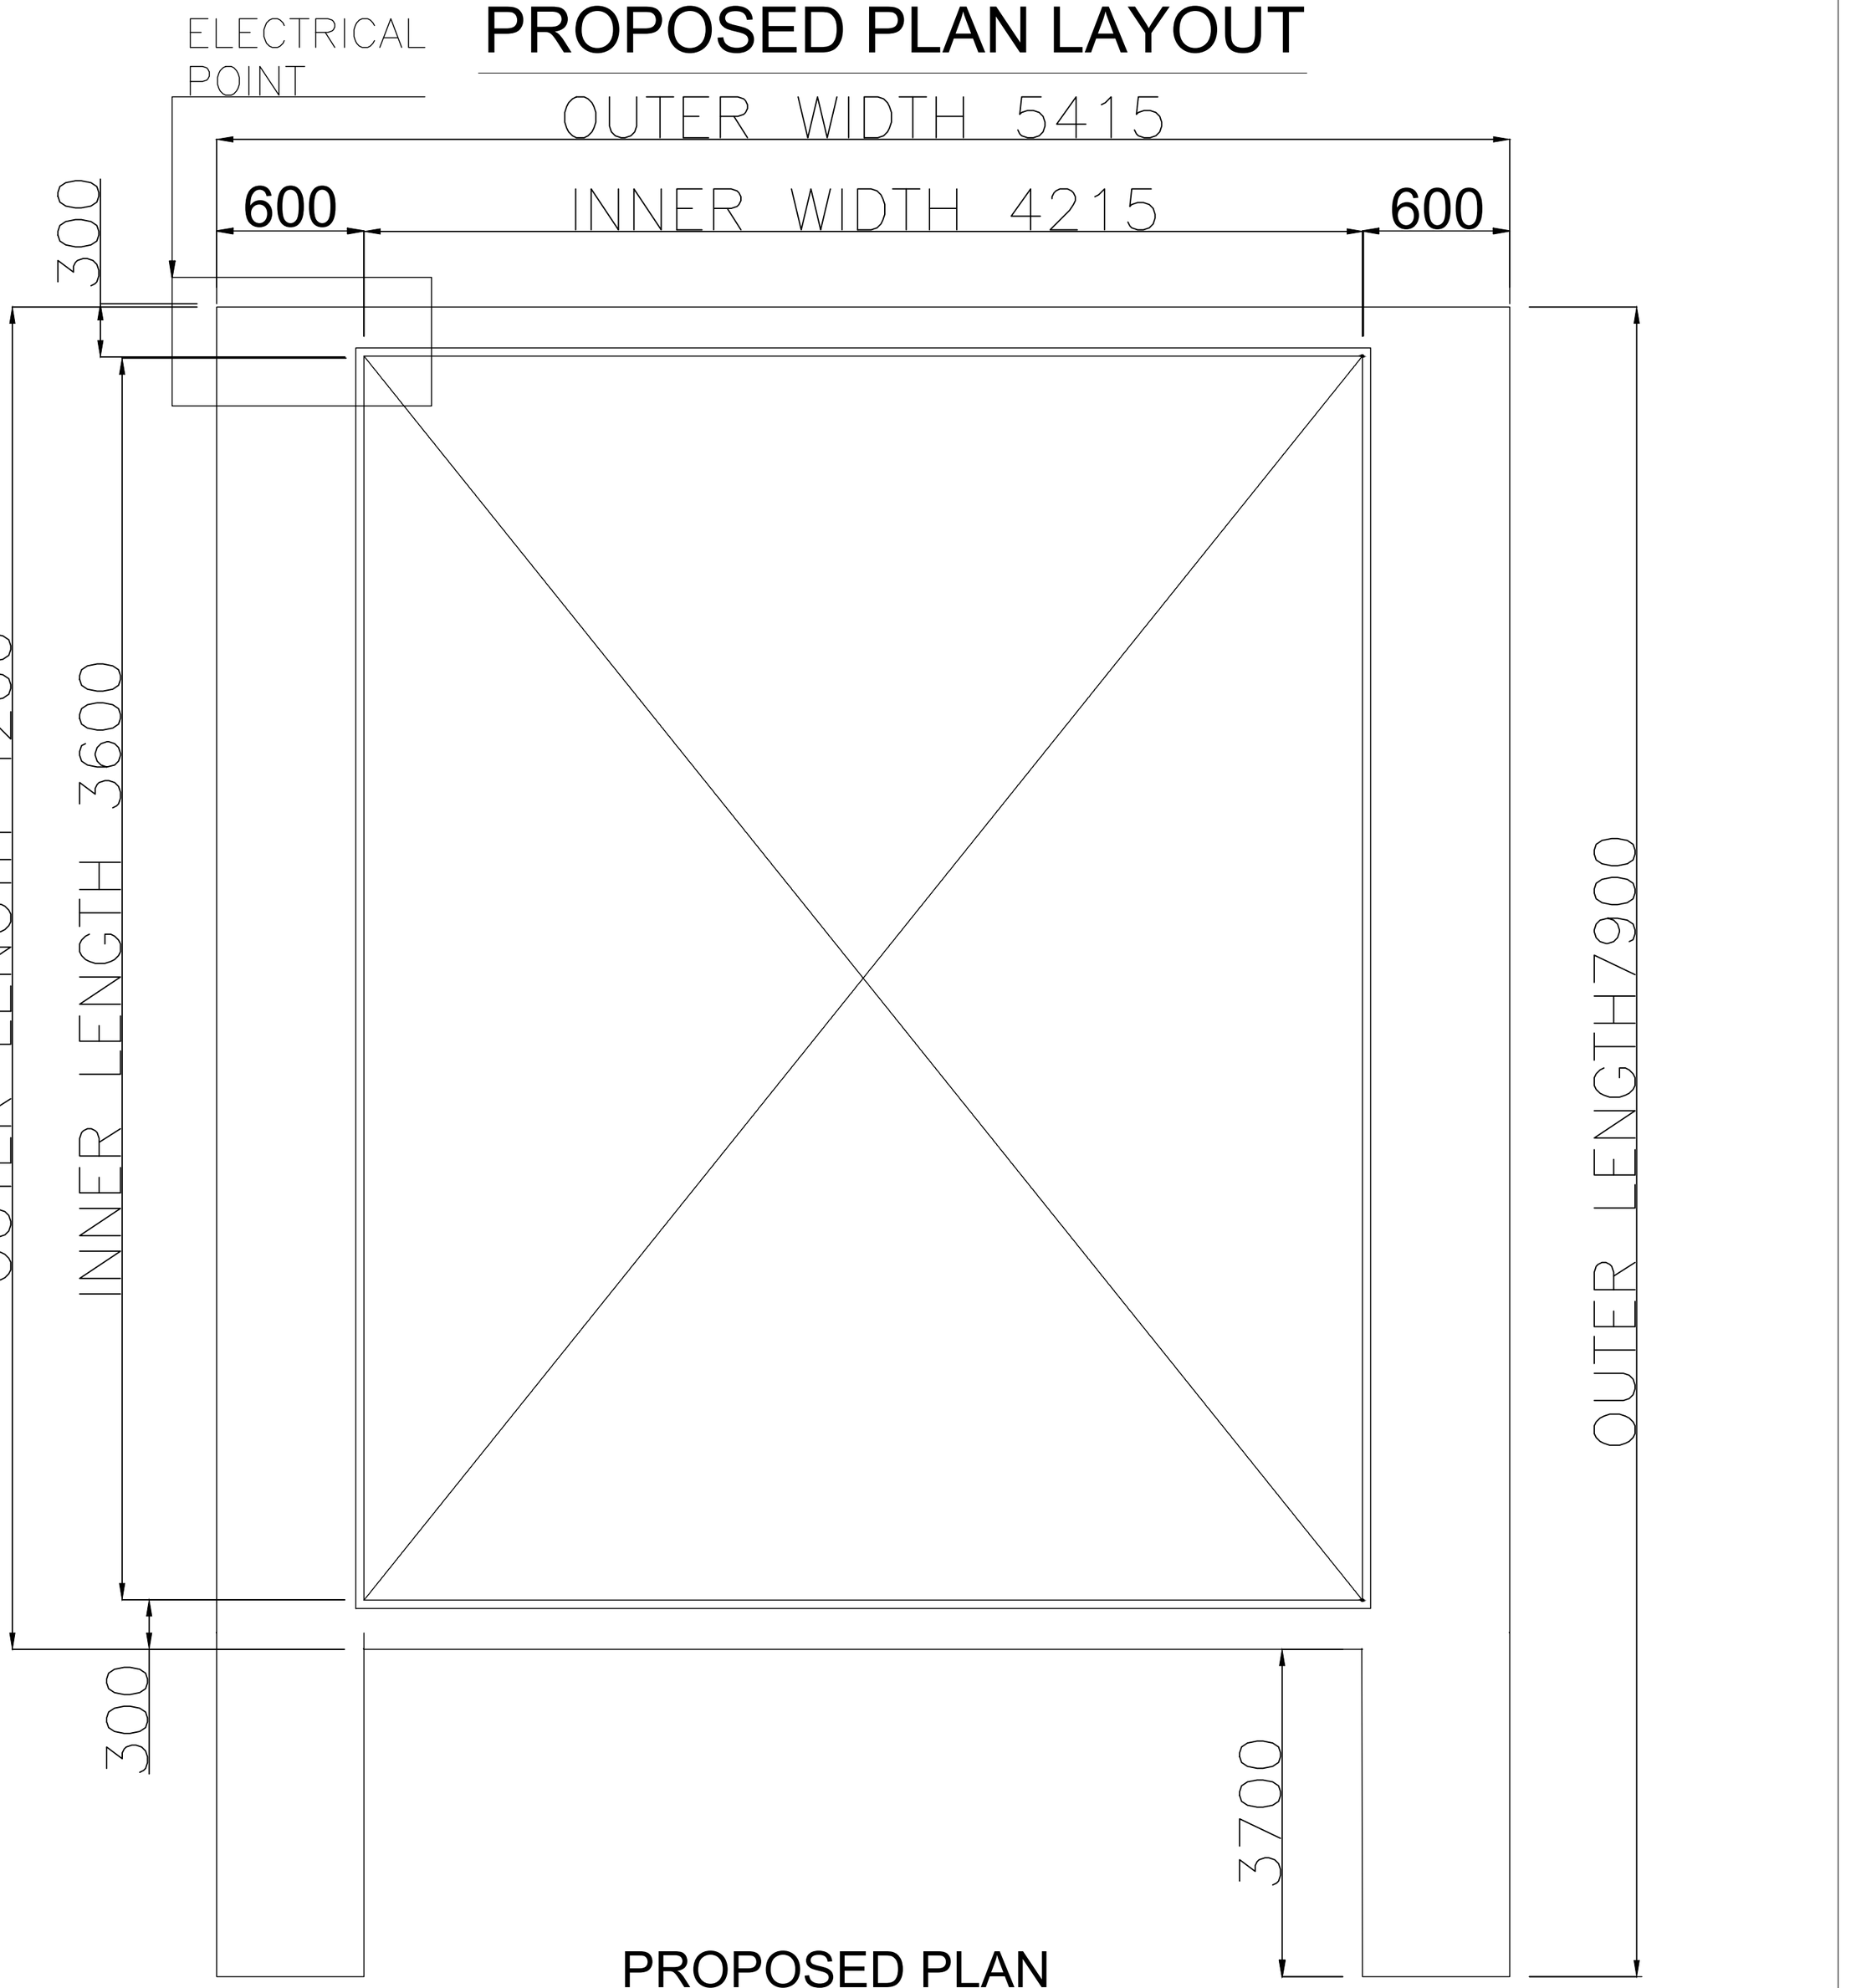

PROPOSED PLAN

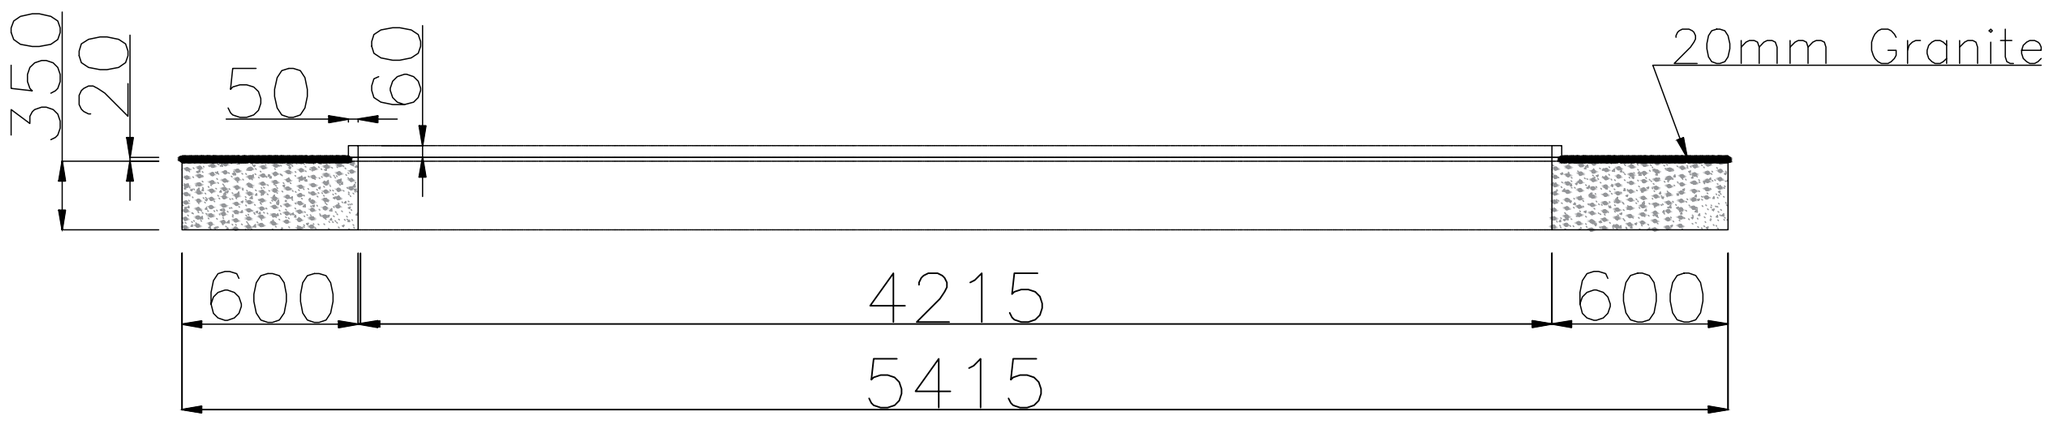

SECTION VIEW

1. THE STRUCTURE AROUND THE CUT OUT SHOULD BE OF CONCRETE FOR FOR PROPER FASTENING OF ROOF.
2. TOP SURFACE SHOULD BE OF GRANITE 20MM FOR SMOOTH FUNCTIONING OF ROOF.
3. ROOF EXTENSION IS SHOWN FOR ONLY REFERENCE. IT CAN BE MODIFIED AS PER THE WORK UNDERTAKEN.
4. GRADIENT OF 50MM NEED TO BE PROVIDED ALONG THE OUTER LENGTH TO AVOID WATER STAGNANCY IN GUIDE RAIL.
5. AL PROFILE - POWDER COATED
6. GASKET - EPDM
7. MOTOR - ITALIAN/GERMAN MAKE
8. ALL DIMENSION IN MM.
9. PROPOSED CIVIL PLAN LAYOUT (IN CLIENT SCOPE)

This drawing & design is the property of NIHVA TECHNOLOGIES. Not to be sold or copied to any other concern.

TITLE
PROPOSED CIVIL PLAN LAYOUT (IN CLIENT SCOPE)

NIHVA
NIHVA TECHNOLOGIES PVT. LTD.

	NAME	SIGN	DATE
DRAWN	MAHESH S.		07.11.22
CHECK	MAHESH S.		07.11.22
APPRD.	VIJAY T.		07.11.22

If any queries contact : projectsautomation@nihva.com

ALL DIMENSION ARE IN mm

CLIENT - MEHTA HOUSE
LOCATION - AHMEDABAD
PRODUCT - RETRACTABLE ROOF
NIHVA\22-23\02XX | REV- 0
SCALE: NTS | SHEET: 01 OF 01