

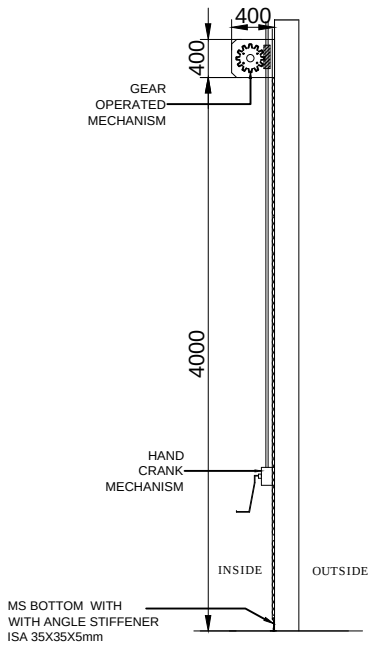



SIDE VIEW

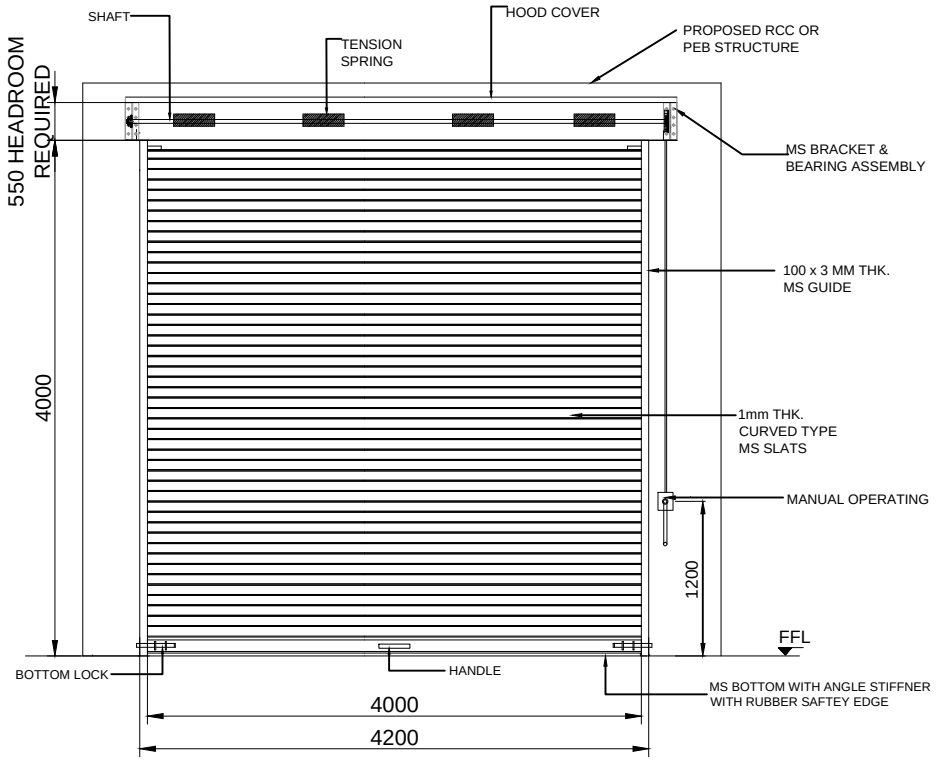


INSIDE ELEVATION

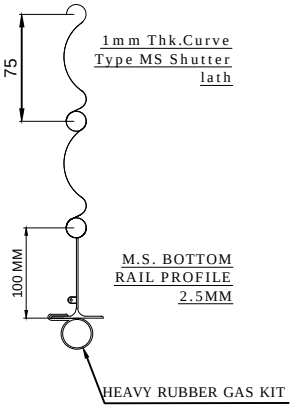

M.S. BOTTOM RAIL PROFILE 2.5MM

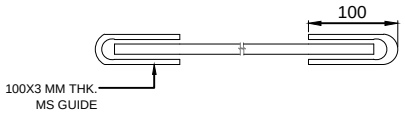

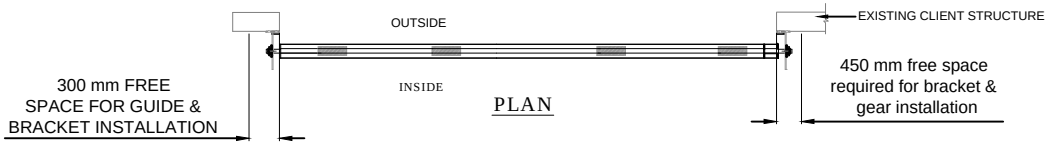

PLAN

NOTE :
COLOR : RAL 9001

S.N.	LOCATION	SIZE	QUANTITY
1	-	4000(W)X4000(H)	04
TOTAL QTY. OF SHUTTER			04

TOLERANCE - ±10mm

This drawing & design is the property of NIHVA TECHNOLOGIES. Not to be sold or copied to any other concern.

TITLE
RIGHT SIDE GEAR OPERATED
ROLLING SHUTTER 4mX4m

NIHVA TECHNOLOGIES PVT. LTD.

NIHVA TECHNOLOGIES
PVT. LTD. PUNE
Tel : 020 66304033
Email:- info@nihva.com
Website:- www.nihva.com

	NAME	SIGN	DATE
DRAWN	PRADEEP		26.07.2018
CHECK	PRADEEP		26.07.2018
APPRD.	R.D		26.07.2018

CLIENT -
PROJECT -
SITE LOCATION -

If any queries contact : design@nihva.com
DWG. NO. : NIHVA/18-19/VDR/079
REV- 0
ALL DIMENSION ARE IN mm
SCALE: NTS
WT:
SHEET: 01 OF 01