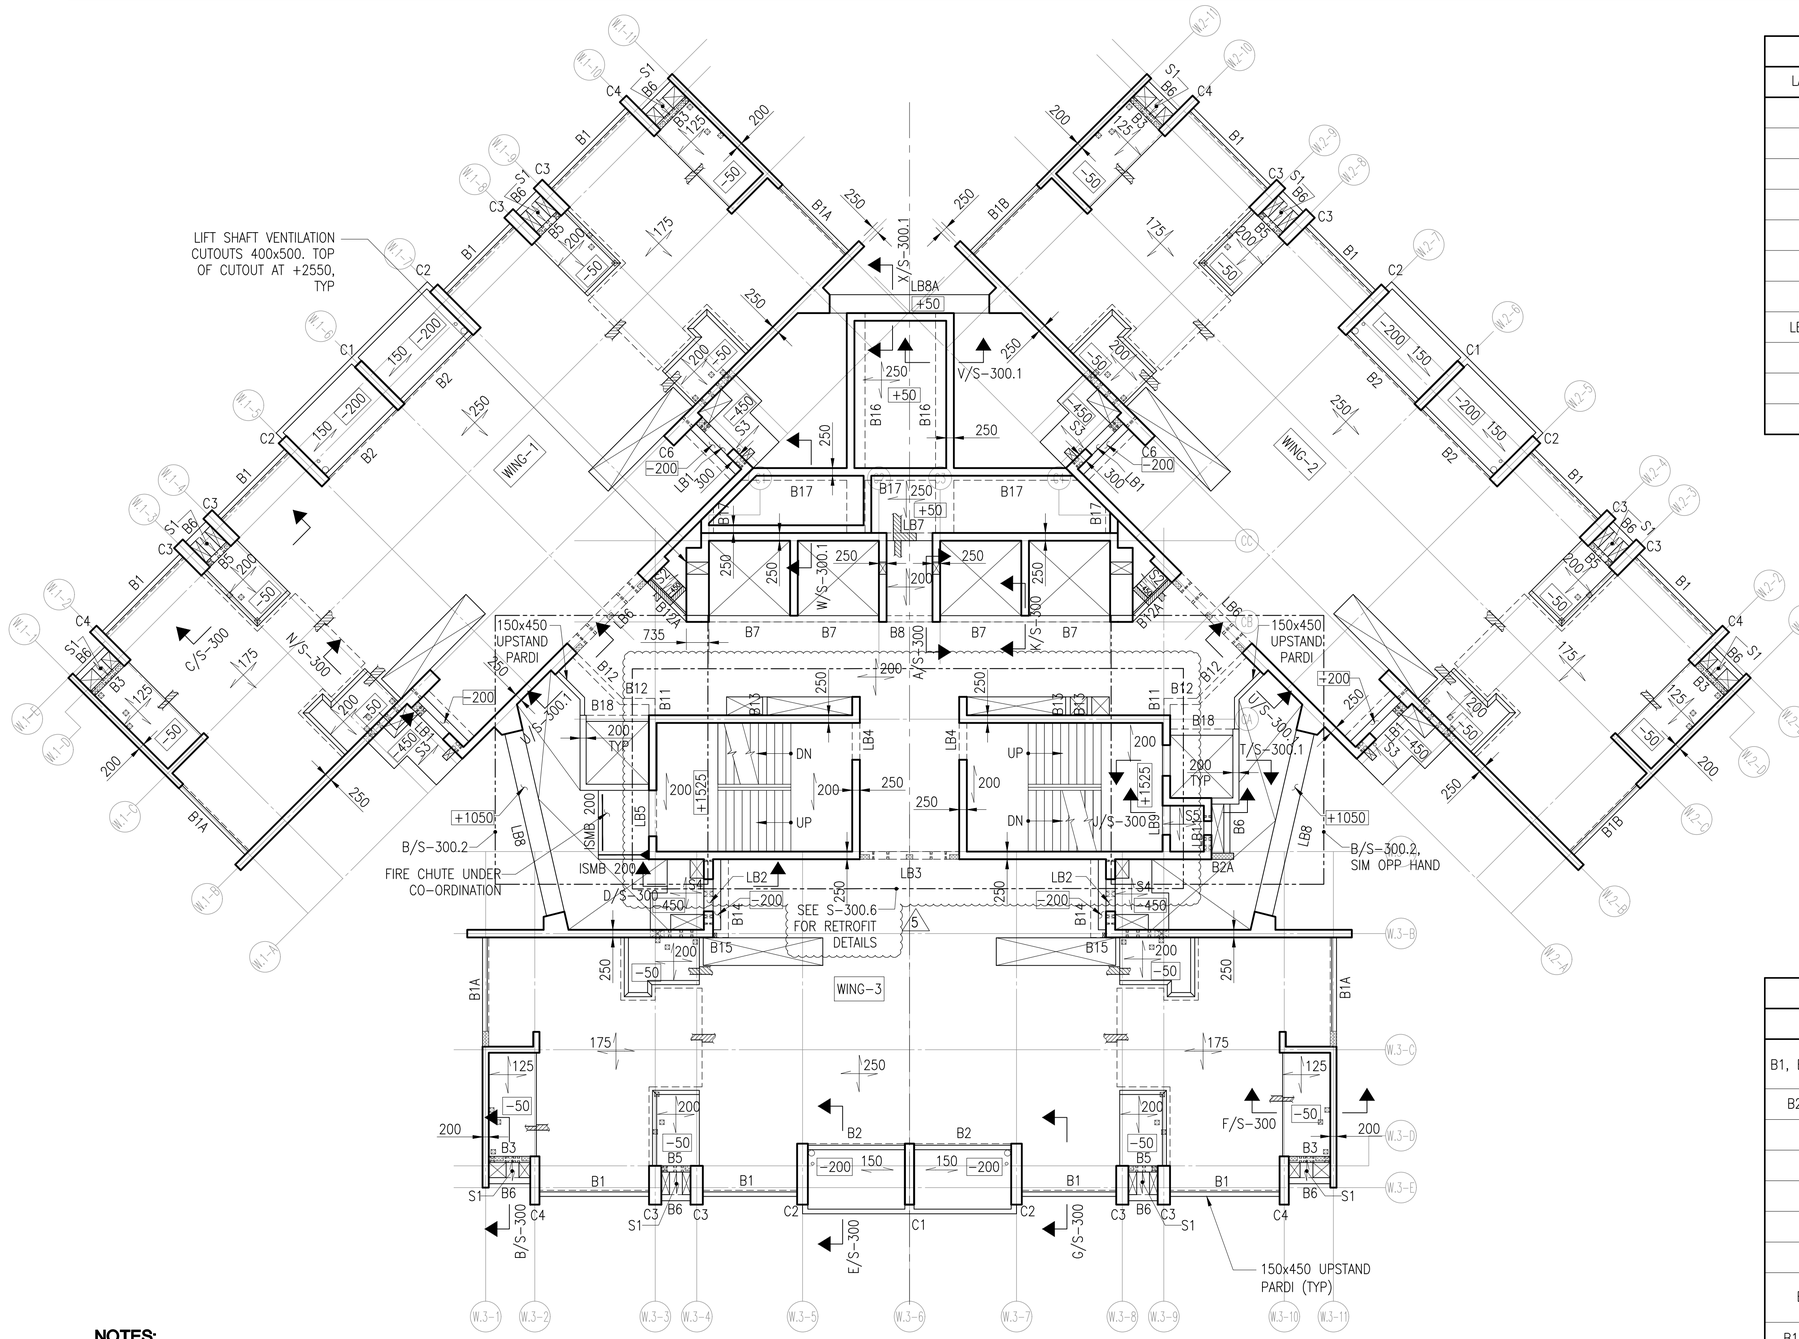


NOTES:

1. TOP OF CONCRETE IS AT REFERENCE ELEVATION NOTED IN ARCH DWGS. UNLESS OTHERWISE NOTED [XXX] ; WHERE [XXX] IS MEASURED WITH RESPECT TO REFERENCE ELEVATION IN MM.
2. REFER S-300 FOR SECTIONS.
3. SOLID CONCRETE SLAB IS INDICATED. SL
4. REINFORCEMENT SHALL BE OF FE 500D (TESTED VARIETY), UON.
5. CONCRETE STRENGTH SHALL BE AS FOLLOWS, UON:
   SLABS & FLOOR BEAMS : M40
   LINK BEAMS, WALLS & COLUMNS : M40
6. READ THIS DRAWING IN CONJUNCTION WITH ARCHITECTURAL DRAWINGS.
7. READ THIS DRAWING IN CONJUNCTION WITH MECHANICAL, ELECTRICAL & PLUMBING DRAWINGS.
8. REFER ARCHITECTURAL DRAWINGS FOR THE LOCATION OF NON STRUCTURAL WALLS.
9. REFER MEP DRAWINGS FOR THE LOCATIONS & DETAILS OF SLEEVES.
10. ALL DIMENSIONS ARE IN MM.
11. [Ψ] INDICATES INFORMATION TO BE PROVIDED BY ARCHITECT.
12. INDICATES NON STRUCTURAL RCC WALL
13. CONTRACTOR SHALL CO-ORDINATE WITH ARCHITECT FOR THE OPENING REQUIREMENTS IN SLAB FOR THE STAIR CASE.
14. LIGHT WEIGHT FILL OF 300MM IS ALLOWED IN DOMESTIC & FIRE TANK

NOTE: ADDED GRID LINES AS PER ARCH. DRAWING & MEP SLEEVES AS PER BUILDER WORK DRAWING.

LINK BEAM SCHEDULE

LABEL	SIZE (MM)	REMARK
LB1	300 x 1200	TOP OF BEAM +450
LB2	300 x 1200	TOP OF BEAM +450
LB3	250 x 600	
LB4	250 x 600	
LB5	250 x 900	TOP OF BEAM +1525
LB6	450 x 600	
LB7	250 x 750	TOP OF BEAM +50
LB8, LB8A	600 x 1500	ALTERNATE FLOORS
LB9	250 x 900	TOP OF BEAM +1525
LB11	250 x 1075	TOP OF BEAM +1475

COLUMN SCHEDULE

LABEL	SIZE (MM)
C1	300 x 1990
C2	350 x 1990
C3	400 x 1265
C4	300 x 1575

SLAB SCHEDULE

LABEL	THICKNESS	SUNK FROM REF. ELEV.
S1	150	-450
S2	150	-450
S3	150	-450
S4	150	-450
S5	150	+1475

BEAM SCHEDULE

LABEL	SIZE (MM)	REMARK
B1, B1A, B1B	200 x 450	150 x 450 UPSTAND PARDI
B2, B2A	200 x 450	
B3	200 x 1050	TOP OF BEAM +500
B5	200 x 1050	TOP OF BEAM +500
B6	200 x 350	
B7	200 x 375	
B8	200 x 600	
B12A	200 x 600	150 x 450 UPSTAND PARDI
B11, B12	200 x 600	
B13	150 x 375	
B14, B15	250 x 450	
B16	600 x 800	TOP OF BEAM +50
B17	400 x 600	TOP OF BEAM +50
B12B	DELETED	
B18	200 x 525	

LERA

Leslie E. Robertson Associates
Consulting Engineers (India), Pvt. Ltd.
The Ruby, North Wing, 23rd Floor,
29 Senapati Bapat Marg,
Dadar West, Mumbai – 400 028 India
Tel: 91 22 2437 6001 and 91 22 2437 6003

Client
Oberoi Realty Limited
Commerz, 3rd Floor, International Business Park,
Oberoi Garden City, Mumbai – 400 063 India
Tel: +91 22 6677 3333 Fax: +91 22 6677 3334

No.	Revision/Issue	Date
R5	REVISED AS MARKED	27 JAN 23
R4	REVISED AS MARKED	14 FEB 22
R3	REVISED AS MARKED	03 FEB 22
R2	REVISED AS MARKED	06 SEP 21
R1	REVISED AS MARKED	28 JUL 21
R0	ISSUED FOR CONSTRUCTION	21 JUL 21

Warning:
© Copyright LESLIE E. ROBERTSON ASSOCIATES, CONSULTING ENGINEERS (INDIA), PVT. LTD. IT IS A VIOLATION OF LAW FOR ANY PERSON, UNLESS ACTING UNDER THE DIRECTION OF A PROFESSIONAL, LICENSED IN THE STATE OF THIS PROJECT, TO ALTER IN ANY WAY THESE DRAWINGS. WHERE ANY ITEM IS ALTERED, THE SUPERVISING PROFESSIONAL SHALL AFFIX TO THE ITEM HIS SEAL AND THE INSCRIPTION "ALTERED BY" FOLLOWED BY HIS SIGNATURE, THE DATE, AND A SPECIFIC DESCRIPTION OF THE ALTERATION.

Professional Stamp:

Phase:
GOOD FOR CONSTRUCTION

Project Title:
MAXIMA

Drawing Title:
FLOOR PLAN
29TH LEVEL

Drawn: LERA	Design: LERA
Check: LERA	Date: 21 JULY 2021
Scale: 1:100	Project Number: P 992

Sheet:
S-129