



DOUBLE HEIGHT SKYLIGHT V1

SKYLIGHT SCHEDULE

Home Story Name	Space	Nomenclature	Glass Length (mm)	Glass Width (mm)	Glass Area (SQ.FT.)	Quantity
Terrace Floor (UFTFL), Horizontal Skylight						
	TERRACE SKYLIGHT	SK - 05	5,000	610	33	1
	TERRACE SKYLIGHT	SK - 06	5,000	610	33	1
	TERRACE SKYLIGHT	SK - 07	3100	1500	50	1

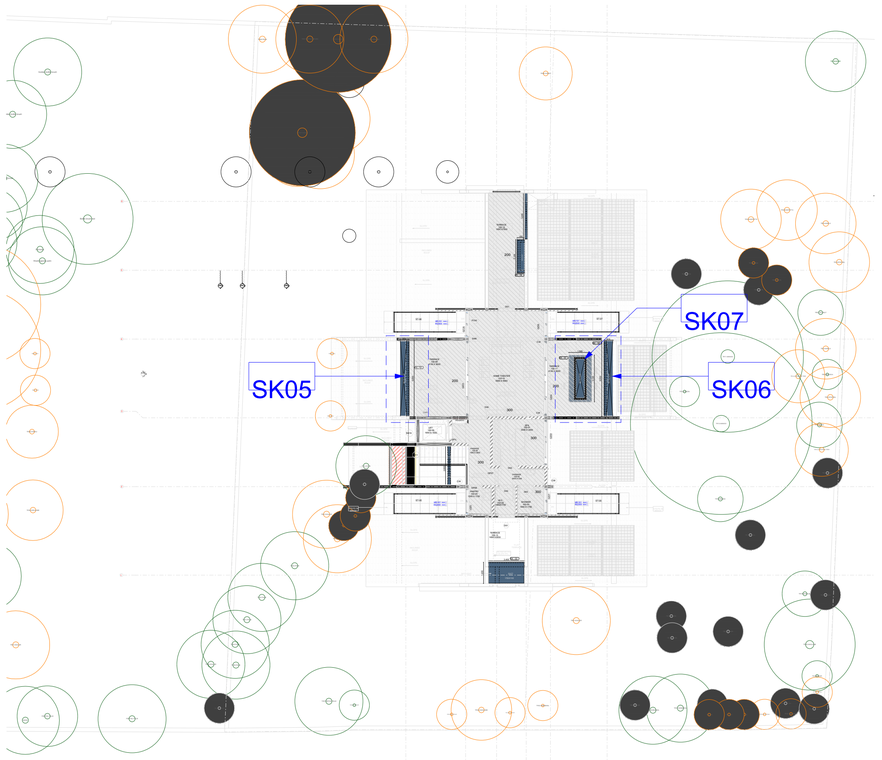

3. Terrace Floor (UFTFL) 1:50

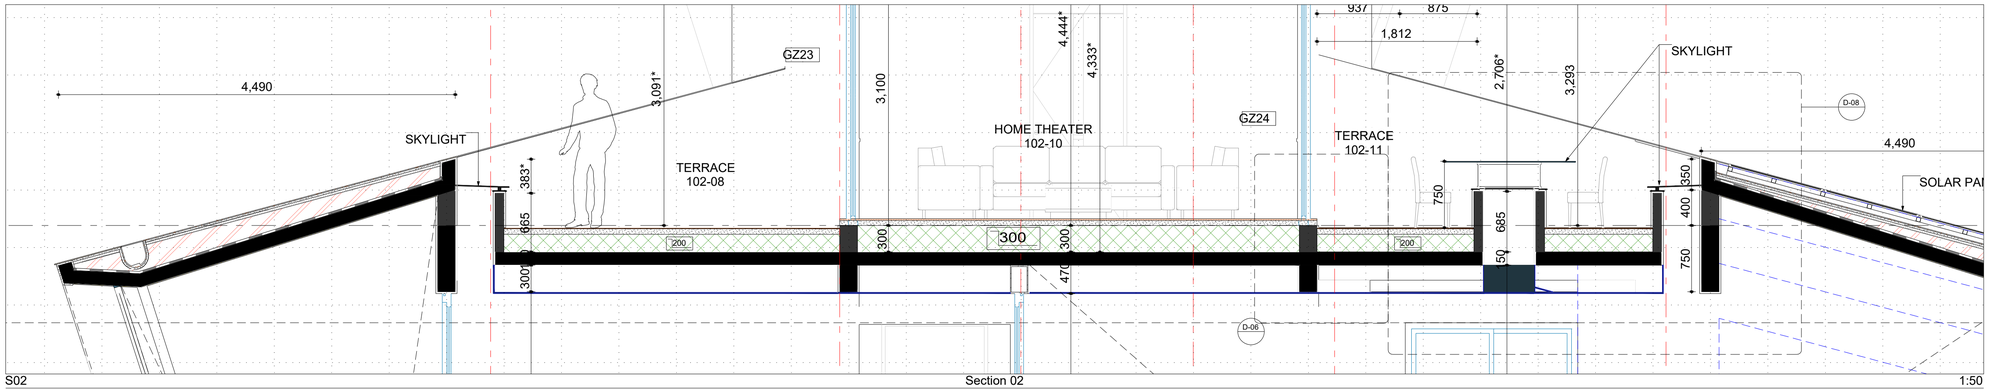

S02 Section 02 1:50

NOTES: GENERAL

- ALL DIMENSIONS AREA IN mm (MILLIMETER).
- DRAWING SHALL NOT BE SCALED AND ONLY WRITTEN DIMENSIONS SHALL BE FOLLOWED.
- IN CASE OF ANY DISCREPANCY FOUND IN DRAWINGS AND DETAILS, IT SHALL BE BROUGHT TO THE NOTICE OF THE ARCHITECT AND RECTIFIED PRIOR TO ITS EXECUTION.
- THIS DRAWING IS ISSUED STRICTLY WITH AN UNDERSTANDING THAT IT WILL BE USED ONLY FOR THE PURPOSE MENTIONED AND SHALL NOT BE RETURNED AFTER COMPLETION.
- LARGER SCALE DRAWINGS AND DETAILS SUPERSEDE THE SMALLER SCALE DRAWINGS AND DETAILS.
- THIS DRAWING SHALL BE REFERRED ONLY FOR THE PURPOSE MENTIONED IN ITS TITLE (FLOORING PATTERN, FALSE CEILING, SHUTTERING PATTERN, ELECTRICAL, PLUMBING ETC.)

NOTES: CONTENT

- ARCHITECT TO APPROVE CRITICAL SIDE MARGINS.
- ARCHITECT TO CHECK BUILDING LINE DIMENSIONS.
- ARCHITECT TO APPROVE DATUM LEVEL FOR BUILDING PLINTH.
- APPLY ANTI TERMITE TREATMENT BEFORE BACKFILL.
- READ IN CONJUNCTION WITH STRUCTURAL CONSULTANTS' DRAWINGS.
- CONTRACTOR SHALL GUARANTEE PERFORMANCE OF WATERPROOFING FOR TERRACE, TOILETS, LIFT PIT, BASEMENT, WATER STORAGE TANKS ETC.
- READ IN CUNJUNCTION WITH STRUCTURAL & MEP CONSULTANTS DRAWINGS.

A	07.01.2026	PMC	01	FOR STUDY PURPOSE
#	DATE	ISSUED TO	COPIES	PURPOSE

SUFFIX

01.	07.01.2026	R0	ABRAR / KAVISH
#	DATE	REVISION	CHECKED

REVISIONS

