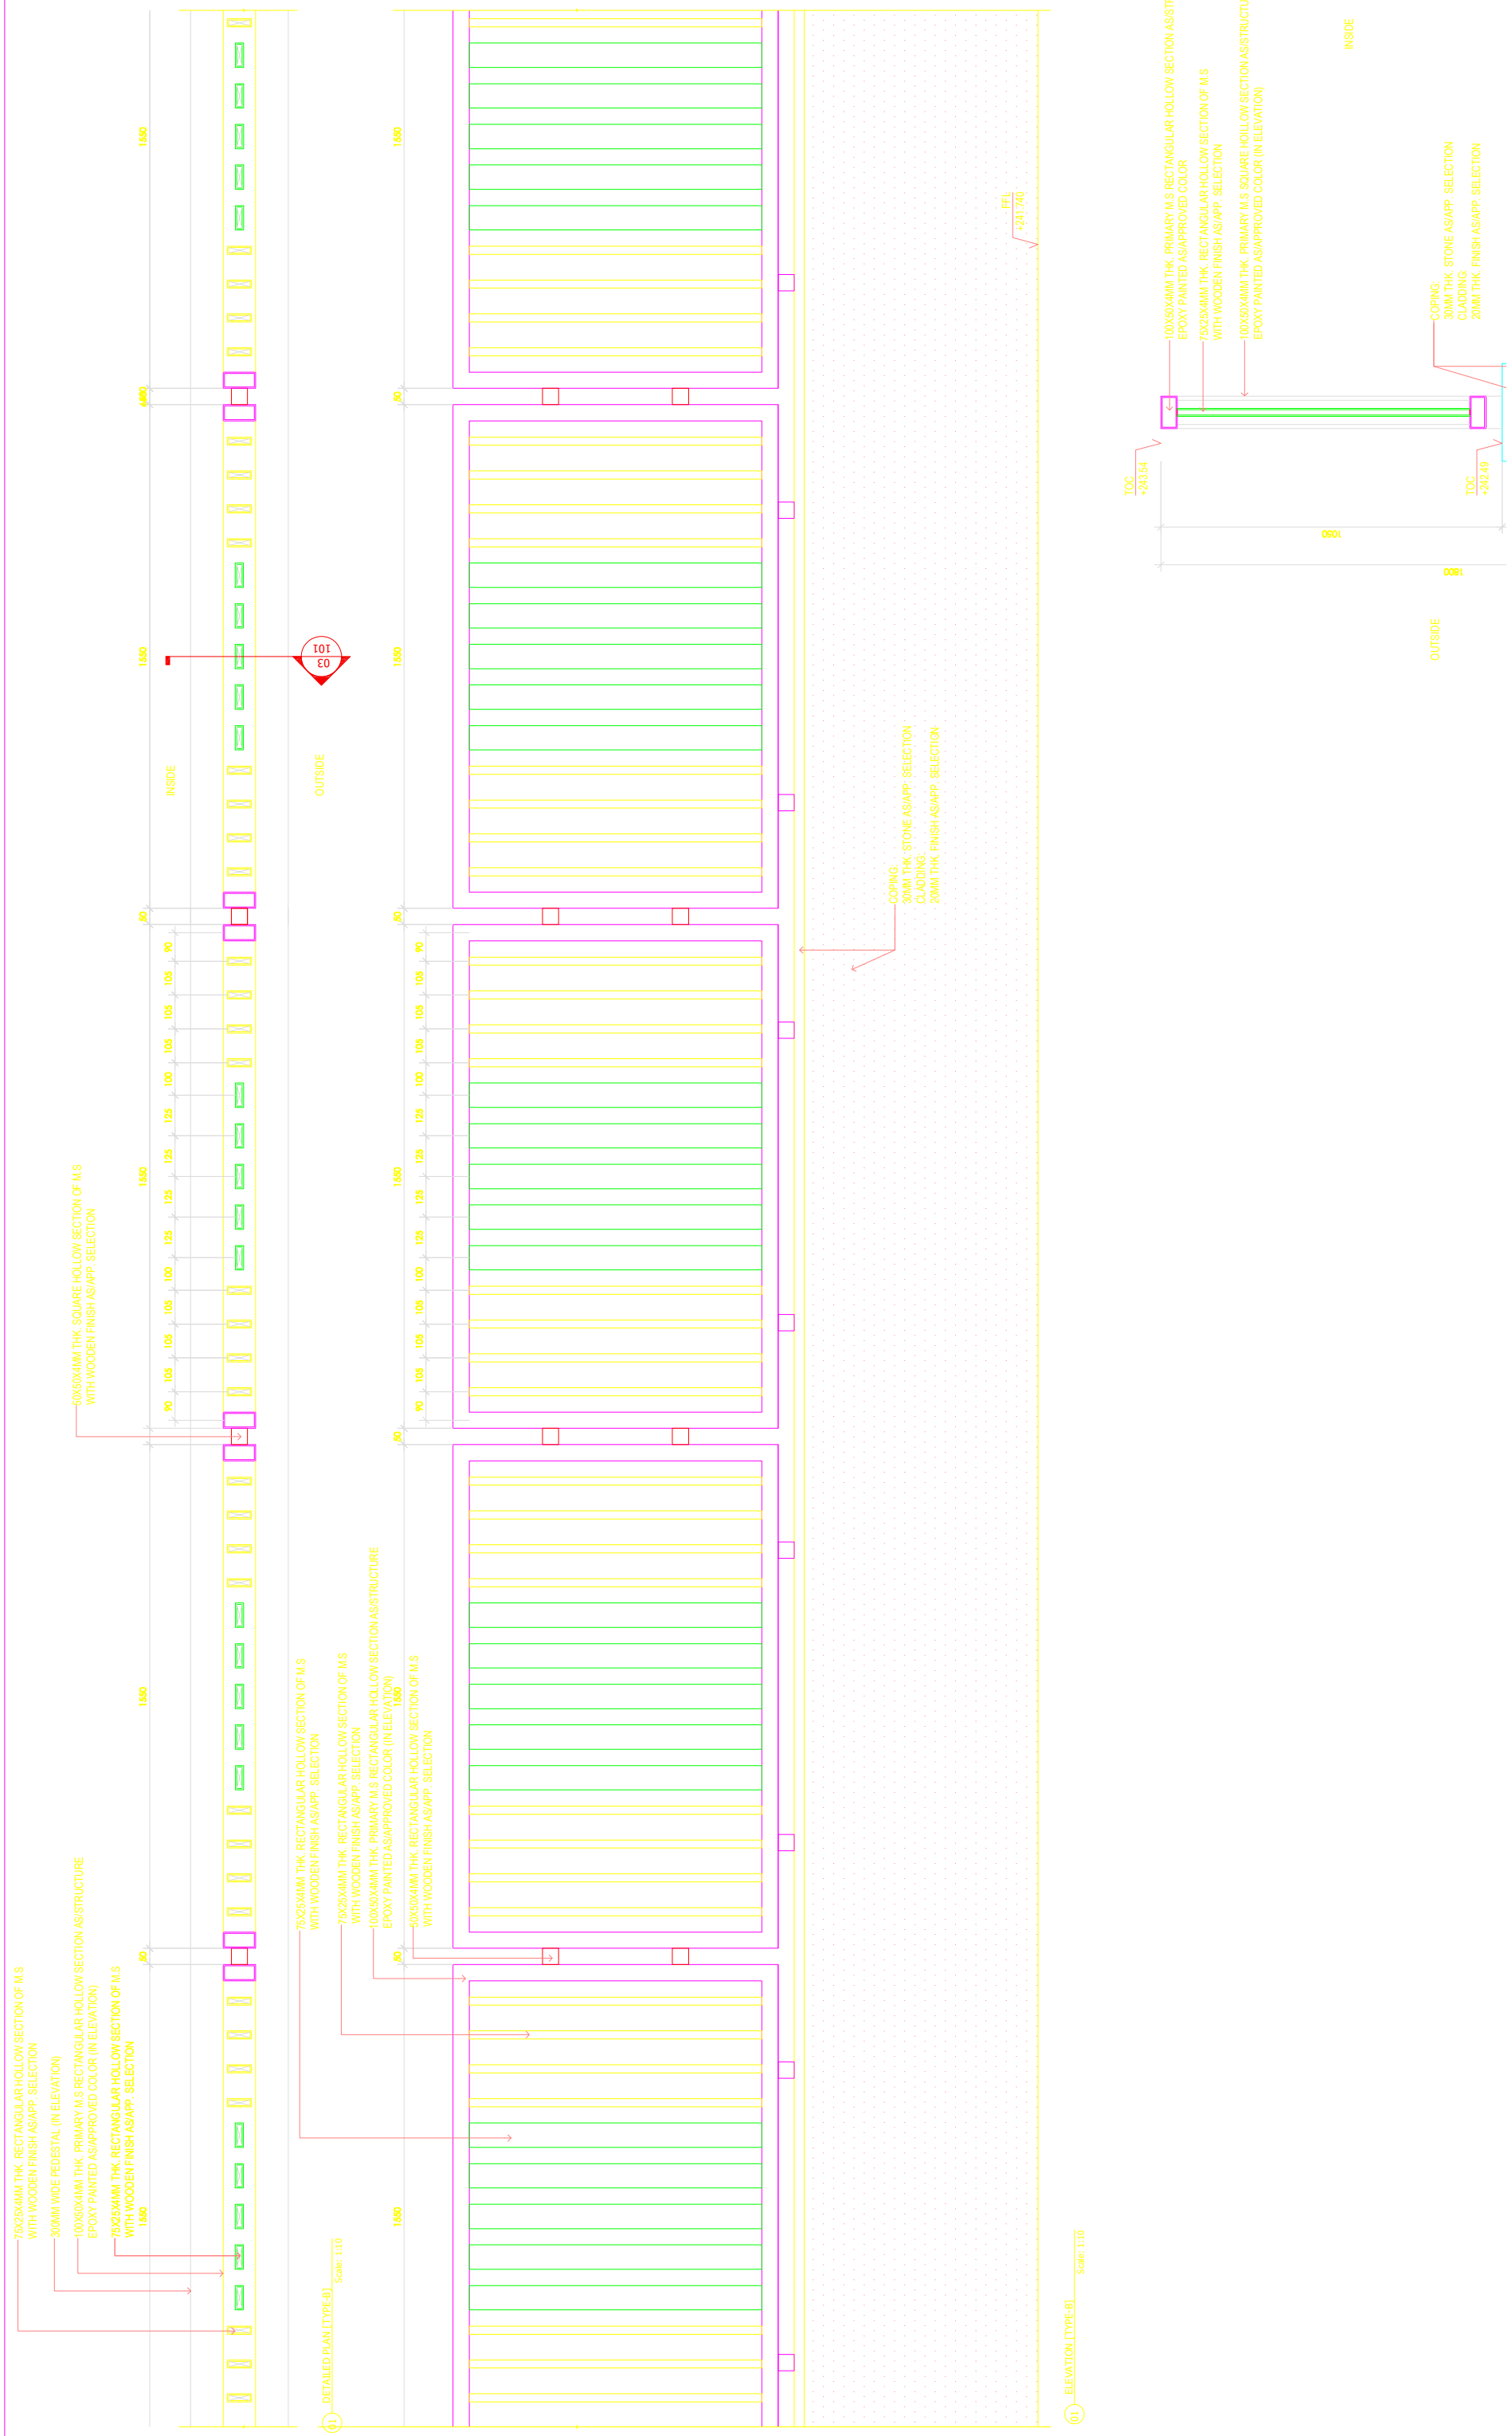

1550
4660
50
1550
1550
03
101
INSIDE
OUTSIDE
FFL
+241.740
100X50X4MM THK. PRIMARY M.S RECTANGULAR HOLLOW SECTION AS/STRUCTURE
EPOXY PAINTED AS/APPROVED COLOR
75X25X4MM THK. RECTANGULAR HOLLOW SECTION OF M.S
WITH WOODEN FINISH AS/APP. SELECTION
100X50X4MM THK. PRIMARY M.S SQUARE HOLLOW SECTION AS/STRUCTURE
EPOXY PAINTED AS/APPROVED COLOR (IN ELEVATION)
COPING:
30MM THK. STONE AS/APP. SELECTION
CLADDING:
20MM THK. FINISH AS/APP. SELECTION
TOC
+243.64
TOC
+242.49
1050
1800
50X50X4MM THK. SQUARE HOLLOW SECTION OF M.S
WITH WOODEN FINISH AS/APP. SELECTION
90
105
100
125
300MM WIDE PEDESTAL (IN ELEVATION)
75X25X4MM THK. RECTANGULAR HOLLOW SECTION AS/STRUCTURE
75X25X4MM THK. RECTANGULAR HOLLOW SECTION OF M.S
WITH WOODEN FINISH AS/APP. SELECTION
01
DETAILED PLAN [TYPE-B]
Scale: 1:10
01
ELEVATION [TYPE-B]
Scale: 1:10