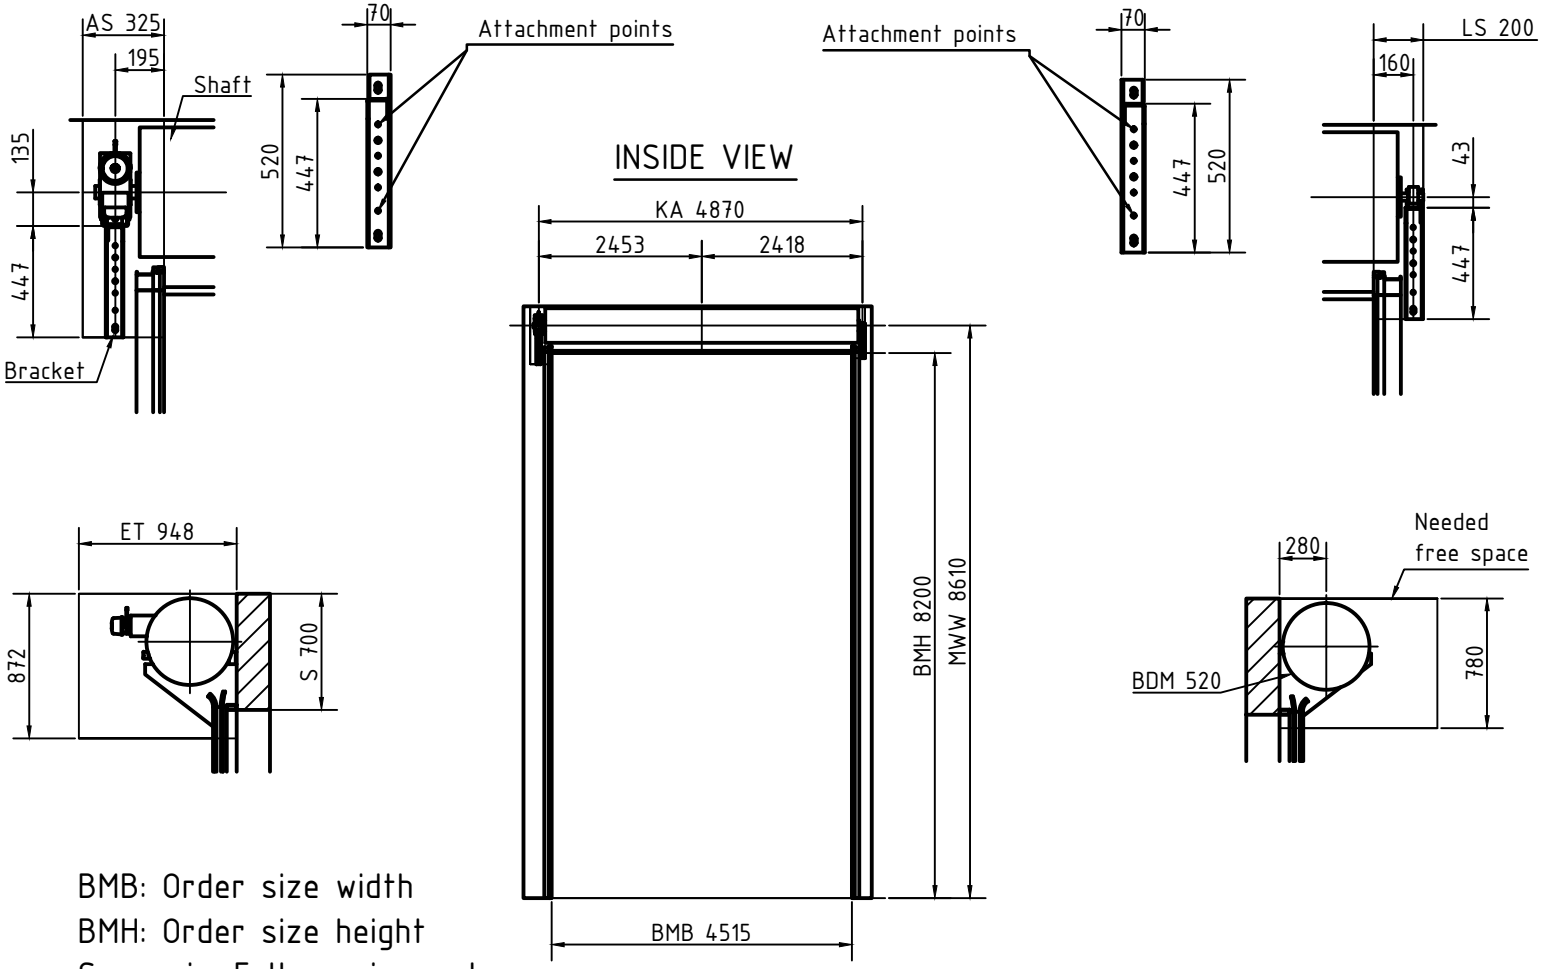

BMB: Order size width
BMH: Order size height
S: min. Fall requirement
AS: min. Stop drive side
LS: min. Stop bearing side
ET: Insertion depth
BDM: Bale diameter
MWW: Middle of winding shaft
KA: Console Spacing

DIMENSION :

CLEAR WIDTH	CLEAR HEIGHT	QUANTITY
4515 mm	8200 mm	
2500 mm	3000 mm	

MATERIAL :

THICKNESS :

NOTE:-
1. All dimensions are in mm.
2. This drawing is a schematic diagram.
3. An onsite substructure required for installing the gate taking into account the specified free spaces.

NIHVA
NIHVA TECHNOLOGIES PVT. LTD.
NIHVA TECHNOLOGIES PVT. LTD. PUNE
Email:- info@nihva.com
Website:- www.nihva.com

TITLE:

DOUBLE WALL ROLLING SHUTTER

CLIENT'S APPROVAL :

CLIENT - SEZ BIOTECH

PROJECT -

SITE LOCATION - PUNE

DWG. NO. : NIHVA/20-21/0205

SCALE: NTS	WT:	SHEET:1 OF 1
DRAWN BY: G.P.		DATE: 12-08-2021
CHECKED BY: A.K.		DATE: 12-08-2021
APPROVED BY : V.T.		DATE: 12-08-2021

If any queries contact : design@nihva.com

NOTE: ALL DIMENSIONS ARE IN mm

THIS DRAWING & DESIGN IS THE PROPERTY OF NIHVA TECHNOLOGIES. NOT TO BE SOLD OR COPIED TO ANY OTHER CONCERN.