


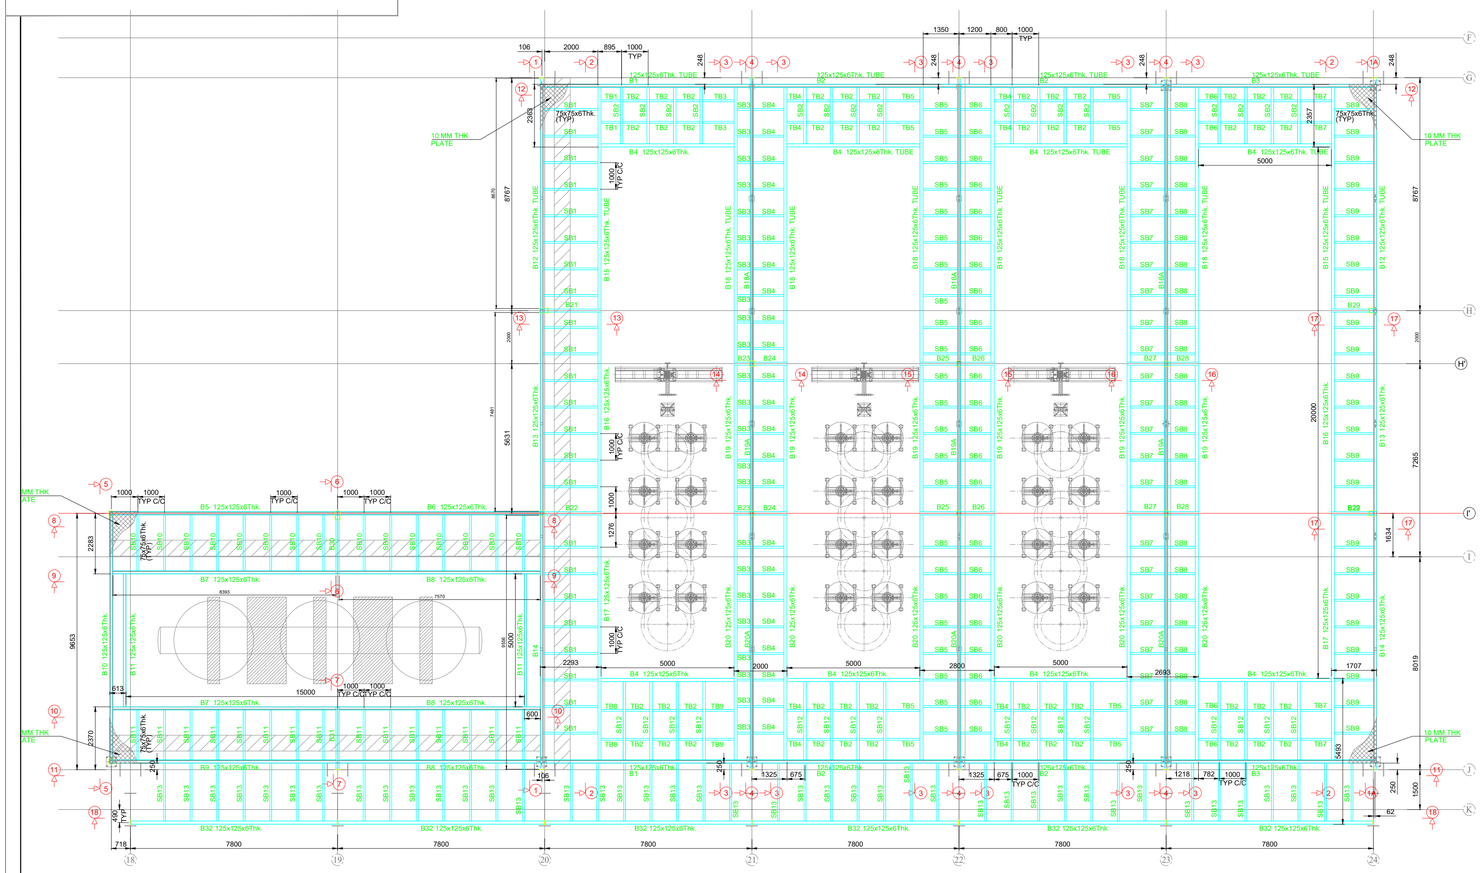


LAYOUT PLAN AT +5.00M LEVEL

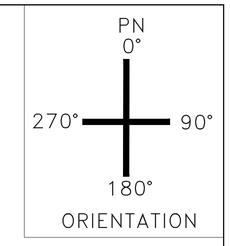

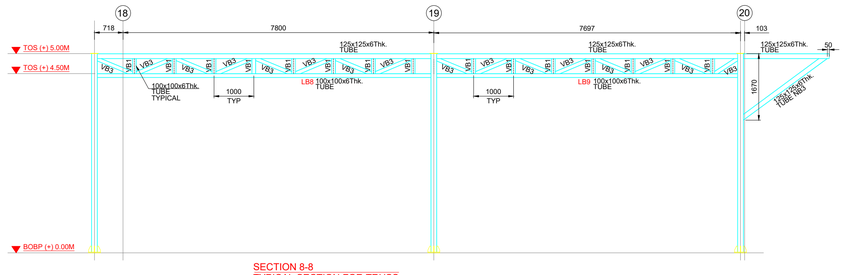


SECTION 8-8
TYPICAL SECTION FOR TRUSS & COLUMN
ELEVATION ON GRID- I'

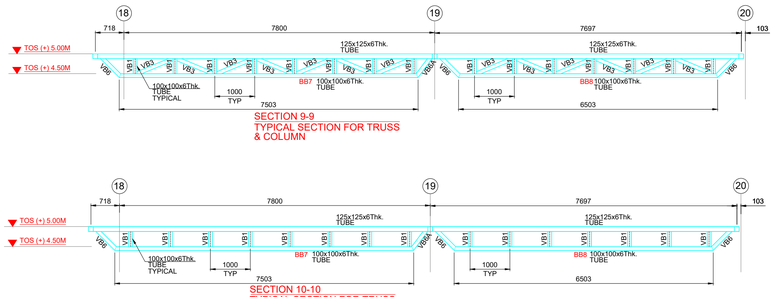


SECTION 9-9
TYPICAL SECTION FOR TRUSS & COLUMN


SECTION 10-10
TYPICAL SECTION FOR TRUSS & COLUMN

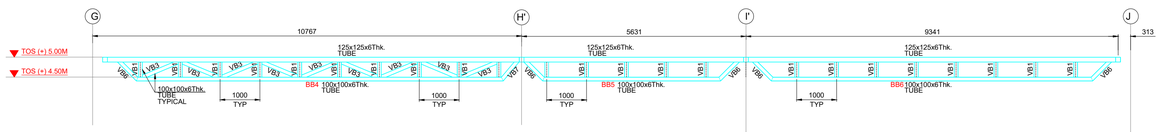


SECTION 3-3
TYPICAL SECTION FOR TRUSS & COLUMN

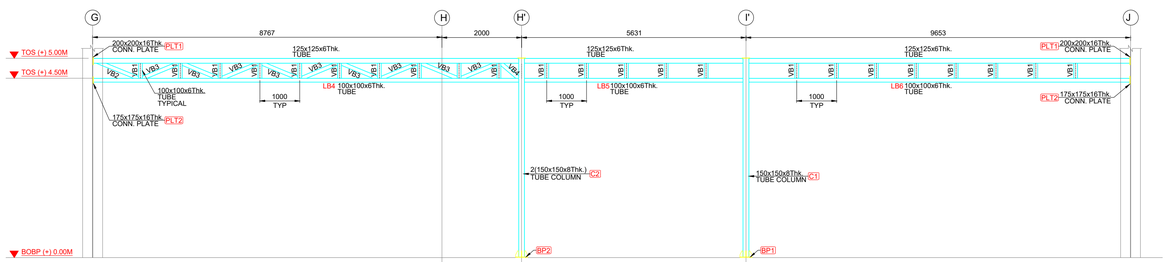

SECTION 4-4
TYPICAL SECTION FOR TRUSS & COLUMN
ELEVATION ON GRID- 21, 22, 23

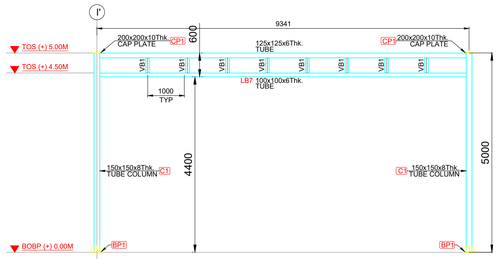

SECTION 5-5
TYPICAL SECTION FOR TRUSS & COLUMN
ELEVATION ON GRID- 18

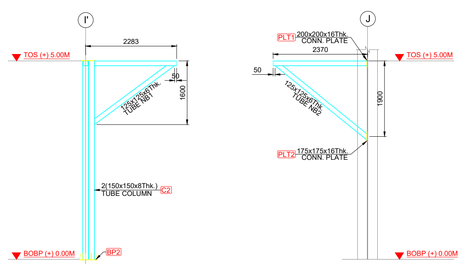

SECTION 6-6
TYPICAL SECTION FOR TRUSS & COLUMN
ELEVATION ON GRID- 19

SECTION 7-7
TYPICAL SECTION FOR TRUSS & COLUMN
ELEVATION ON GRID- 19

STEEL NOTES:-

1. ALL DIMENSIONS ARE IN MILLIMETRES & LEVELS ARE IN METRES.
2. ALL STRUCTURAL STEEL AS PER IS:2062.
3. PROVIDE WELDING AS PER IS:816.
4. PROVIDE MIN. 6MM WELD.
5. USE ELECTRODS AS PER IS:814 (PT.-I).
6. FILLET/ BUTT WELD SHALL BE OF 6MM SIZE AND SHALL BE CONTINUOUS.
7. FABRICATION AND ERECTION SHALL BE AS PER IS:800 AND IS:803.
8. WELD SHALL BE GROUND SMOOTH.
9. ALL GUSSET PLATES SHALL BE MIN. 8 THK.
10. ALL M.S. BLACK BOLTS AND NUTS SHALL CONFORM TO IS:1363(PT. 1 TO 3).
11. ALL STRUCTURE WILL BE PROVIDED WITH MIN. ONE COAT OF EPOXY PRIMER AND ONE COATS OF PU PAINT.
12. ALL CONNECTIONS SHALL BE FULLY WELDED AFTER BOLTING.

REV.NO.	DESCRIPTION.	REV.DATE	DRAWN.	CHKD.	APPD.
1	RELEASE FOR APPROVAL.	01.08.26	MHS	HAB	HAB
0	RELEASE FOR APPROVAL.	20.07.26	MHS	HAB	HAB

DWG.TITLE :- FABRICATION DRAWING FOR NEOTRAFO - VM-HM

CLIENT	NEOTRAFO SOLUTIONS PVT.LTD. HYDERABAD, INDIA.
PROJECT NIHVA Technologies Pvt. Ltd.	NIHVA TECHNOLOGIES PVT.LTD. WEBSITE - www.nihva.com
LOCATION :	HYDERABAD
SALT Design Services	SALT DESIGN SERVICES 4-PUSHKAR NIRZAR, SBI COLONY, NEAR ICICI BANK, KOTHRUD, PUNE-411038.

DRAWN : MHS	CHECKED : HAB	SCALE: NTS
APPROVED : HAB		DATE: 20.07.26
DWG.NO: SALT_2041_STR_0001	(SH-3 OF 5)	REV. - R1 SIZE. - A0