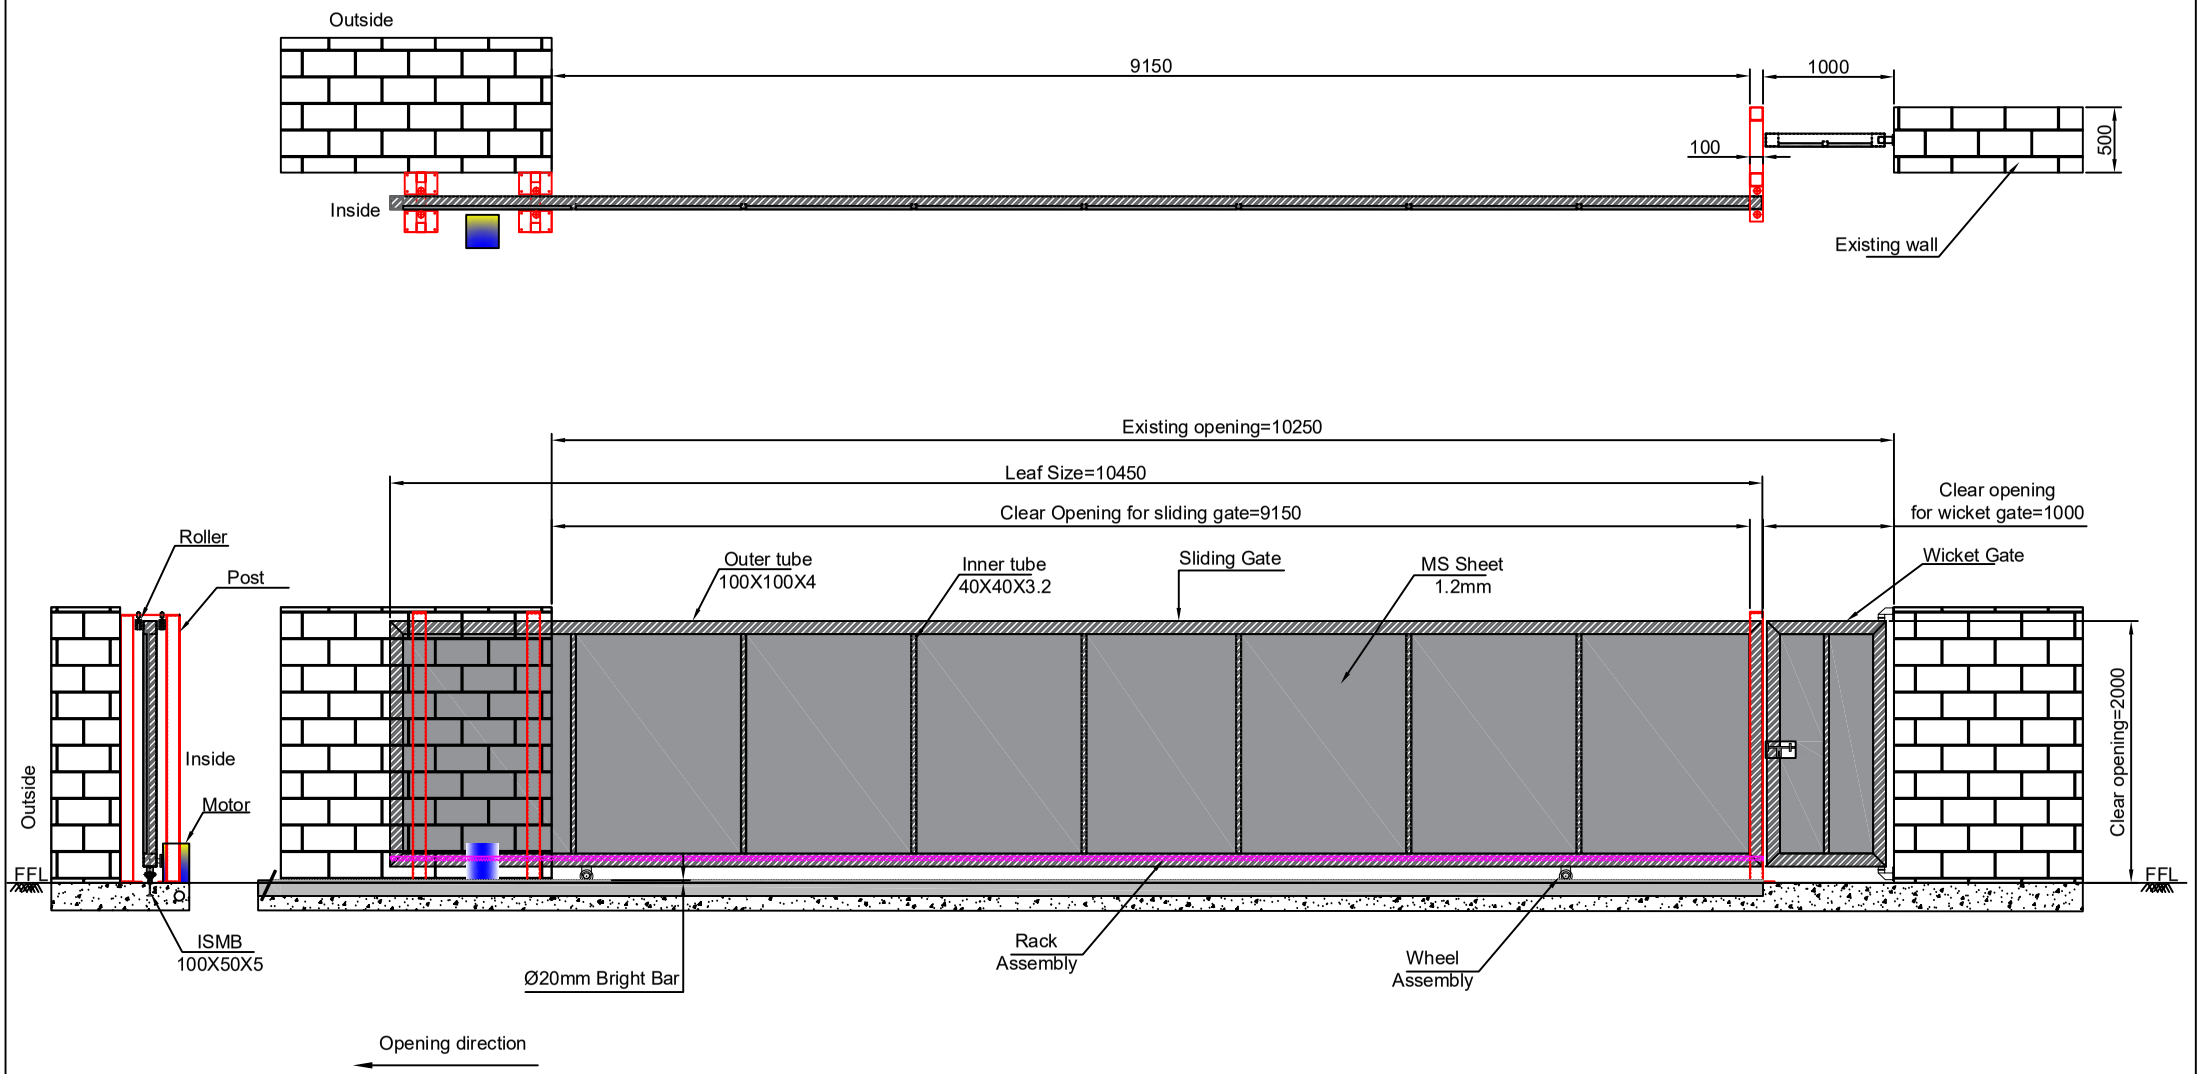


Note:-

1.All Dimension are in MM.

2.Given Above GA drawing is only for the Client Understanding purpose.

3.All Civil work will be in Client scope

4.Civil,Installation and Fabrication Tolerance will be ±20mm

5.Reuired Parking will be 10550mm

This drawing & design is the property of NIHVA TECHNOLOGIES. Not to be sold or copied to any other concern.

TITLE:- Sliding Gate and Wicket Gate(E22,Main Gate)

	NAME	DATE	SIGN
DRAWN	SUJATA	10/05/2022	
CHECK	P.Jain	10/05/2022	
APPRD.	M.Sutar	10/05/2022	

If any queries contact : design@nihva.com

ALL DIMENSION ARE IN mm

NIHVA TECHNOLOGIES PVT. LTD.

NIHVA TECHNOLOGIES PVT. LTD. PUNE
Tel : 020 66304033
Email:- info@nihva.com
Website:- www.nihva.com

CLIENT - OC Specialities

LOCATION - Solapur

PRODUCT - Sliding gate/Wicket gate | QTY-

DWG NO:- NIHVA/22-23/CLT/0030 | REV- 0

SCALE: NTS | SCALE:-- 1:1 | SHEET: 01 OF 01

Rev No.	Revision	Date	Revised By