


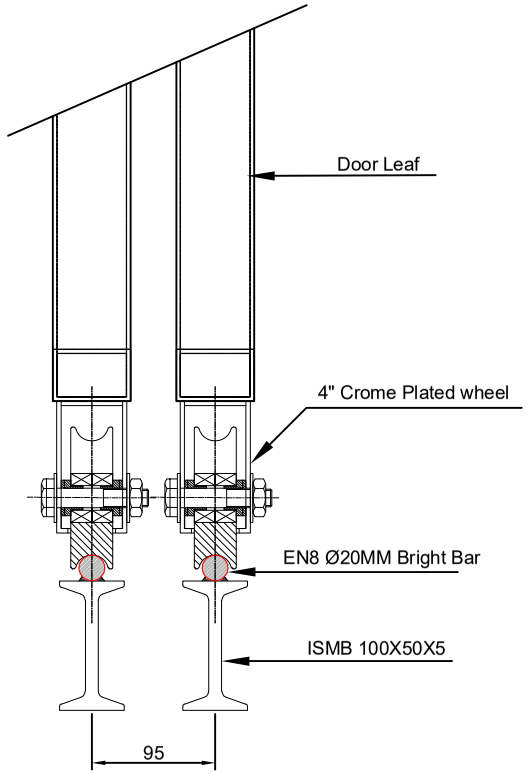

This drawing & design is the property of NIHVA TECHNOLOGIES. Not to be sold or copied to any other concern.

TITLE:- 4LEAF BOTH SIDE SLIDING CRM DOOR-10/Gate 24				NIHVA TECHNOLOGIES PVT. LTD. PUNE Tel : 020 66304033 Email:- info@nihva.com Website:- www.nihva.com
	NAME	DATE	SIGN	
DRAWN	SUJATA	05/05/2022		CLIENT - LESTECH
CHECK	M.SUTAR	05/05/2022		LOCATION - POSCO MANGAON
APPRD.				PRODUCT - SLIDING DOOR
If any queries contact : design@nihva.com				DWG NO:-NIHVA/22-23/MFG/0006 REV- 0
ALL DIMENSION ARE IN mm				SCALE: NTS SCALE:-- 1:1 SHEET: 01 OF 01

Rev No.	Revision	Date	Revised By