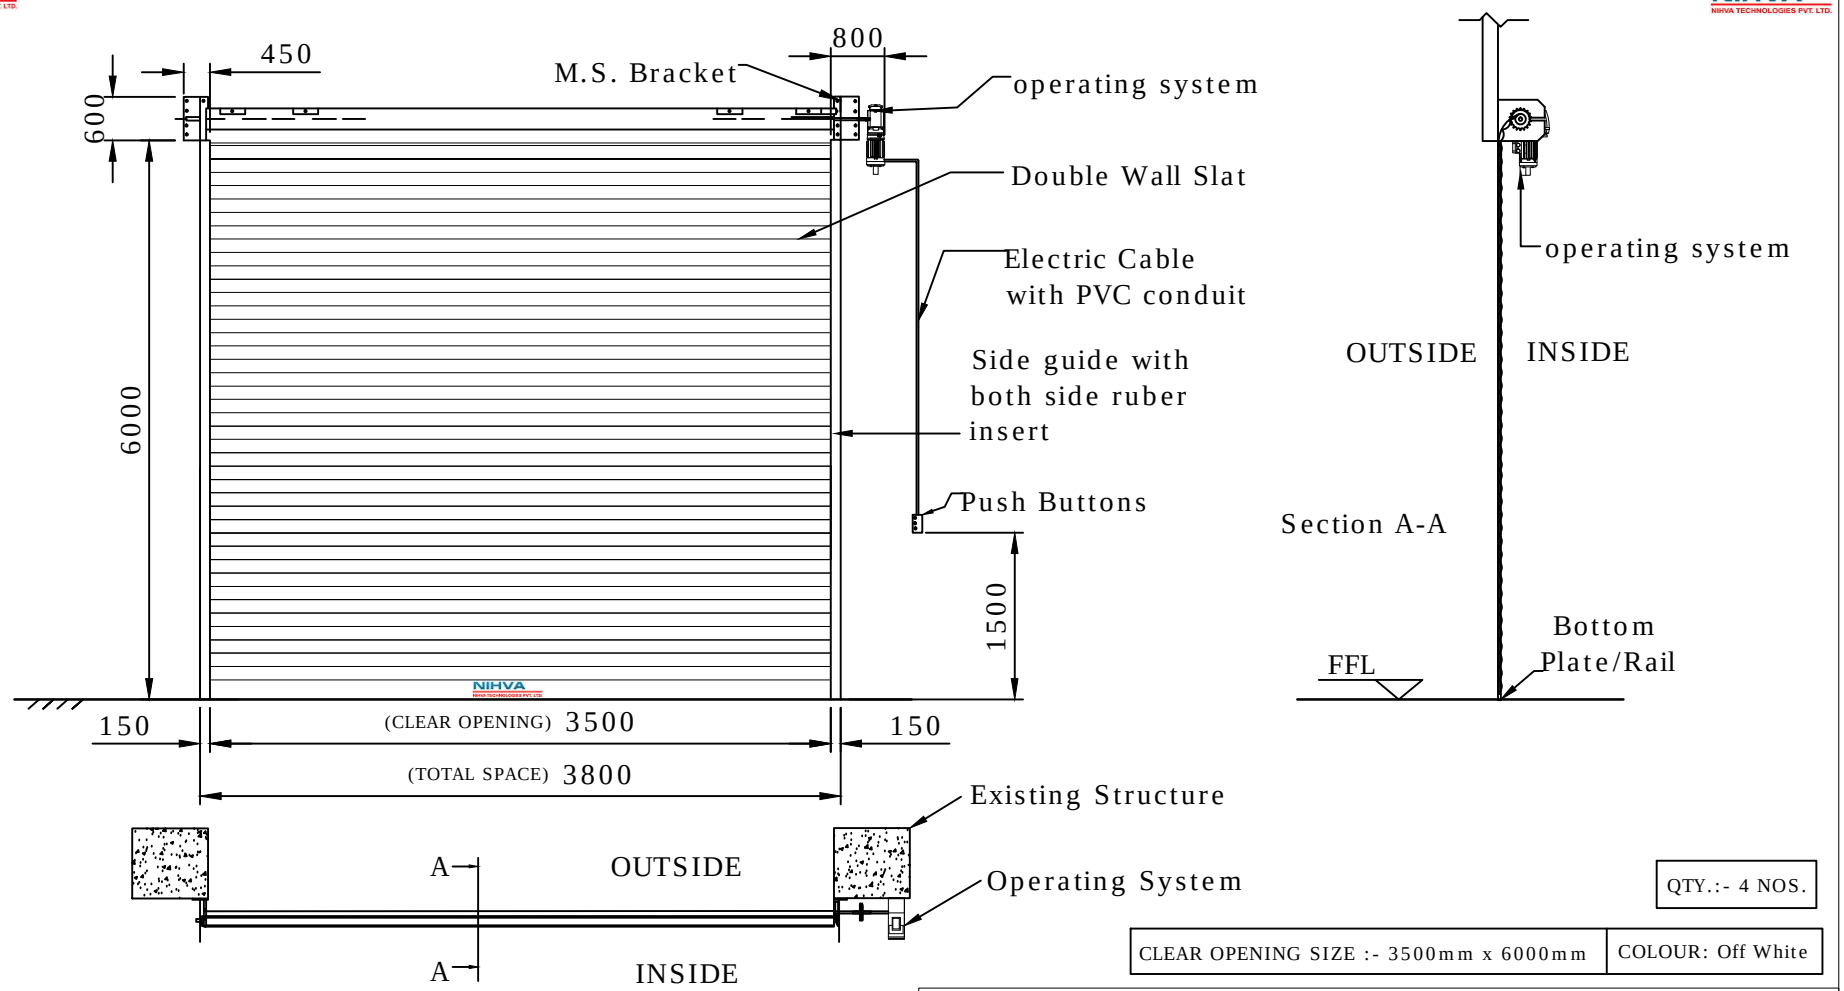


QTY.:- 4 NOS.

CLEAR OPENING SIZE :- 3500mm x 6000mm	COLOUR: Off White

Sr. No.	Details	Specification
1)	Slats Profile	95mm x 19mm with PU filled inside (w/operforation)
2)	Guide Channel	150mm x 40mm
3)	Shaft	160mm OD with heavy duty flanges and hardware
4)	Bottom Rail	125mm x 15mm with extra angle support. Locking arrangement provides
5)	Brackets	600mmx450mmx3mm thickness

This drawing & designing is the property of NIHVA TECHNOLOGIES. Not be sold or copy to any other concern.

TITLE:

DOUBLE WALL
ROLLING SHUTTER

CLIENT APPROVAL

ALL DIMENSION ARE IN mm

	SIGN	DATE
DRAWN	ABHIJIT	21/07/15
CHECK	ANIL	21/07/15
REV.	01	
APPRD.		
MFG		
Ref. No.		

NIHVA TECHNOLOGY
PVT. LTD. PUNE
Tel : 020 66304033
Email:- info@nihva.com
Website:- www.nihva.com

CLIENT - PHENIX

PROJECT - INGERSOLL RAND

SITE - AHAMADABAD

DWG. NO. -NIHVA/15-16/077

SCALE: 01 | WT: | SHEET: 01 OF 01

If any queries contact : projects@nihva.com