




SIDE VIEW

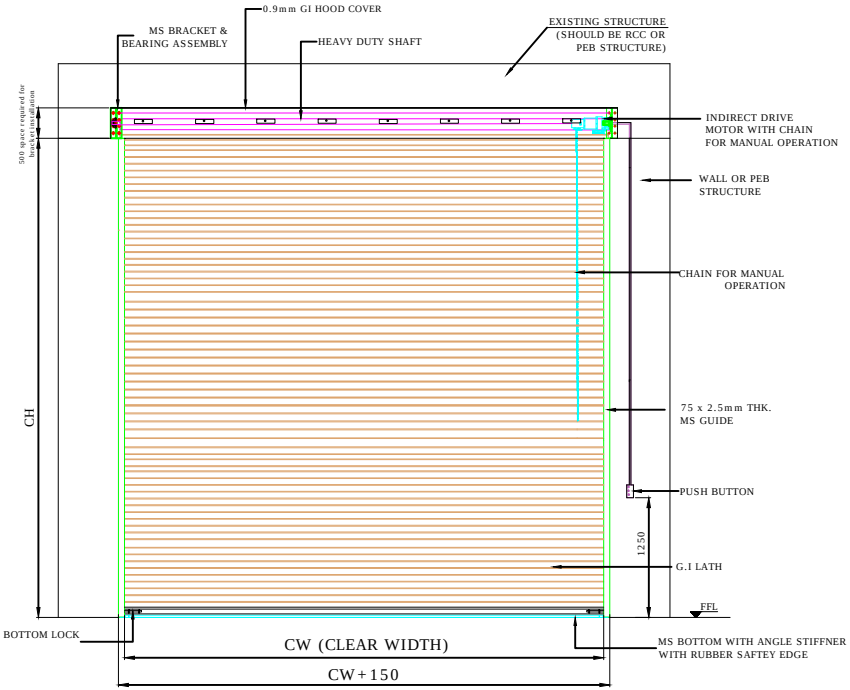


ELEVATION

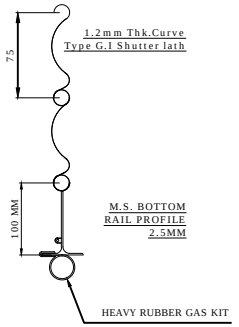

M.S. BOTTOM RAIL PROFILE 2.5MM

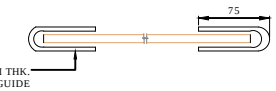

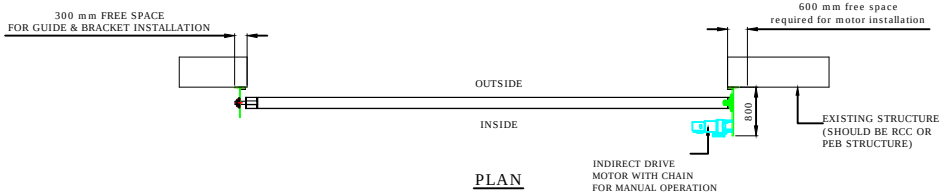

PLAN

NOTE:
1 REQUIRED STRUCTURE FOR SHUTTER SHALL BE IN CLIENT SCOPE.
2.ONE COAT OF RED OXIDE PRIMER WILL BE GIVEN TO THE SHUTTER.
3.SINGLE PHASE. 3CORE 1.2SQ. CABLE REQUIRED AT SITE (CLIENT'S SCOPE)
4COLOUR OF SHUTTER WILL BE RL 5002ULTERMARINE BLUE.

TOLERANCE - ±10mm

CLEAR WIDTH	CLEAR HEIGHT	QTY.
3000mm	3000mm	01NOS

This drawing & design is the property of NIHVA TECHNOLOGIES. Not to be sold or copied to any other concern.

TITLE: MOTORISED ROLLING SHUTTER

	NAME	SIGN	DATE
DRAWN	SURAJ		11-05-2018
CHECK	OMKAR		11-05-2018
APPRD.	PRADEEP		11-05-2018

If any queries contact : design@nihva.com

ALL DIMENSION ARE IN mm

NIHVA TECHNOLOGIES PVT. LTD.
NIHVA TECHNOLOGIES PVT. LTD. PUNE
Tel : 020 66304033
Email:- info@nihva.com
Website:- www.nihva.com

CLIENT -GBRN

PROJECT - CNH

SITE LOCATION - CHAKAN

DWG. NO. : NIHVA/18-19/0034 | REV- 0

SCALE: NTS | WT: | SHEET: 01 OF 01