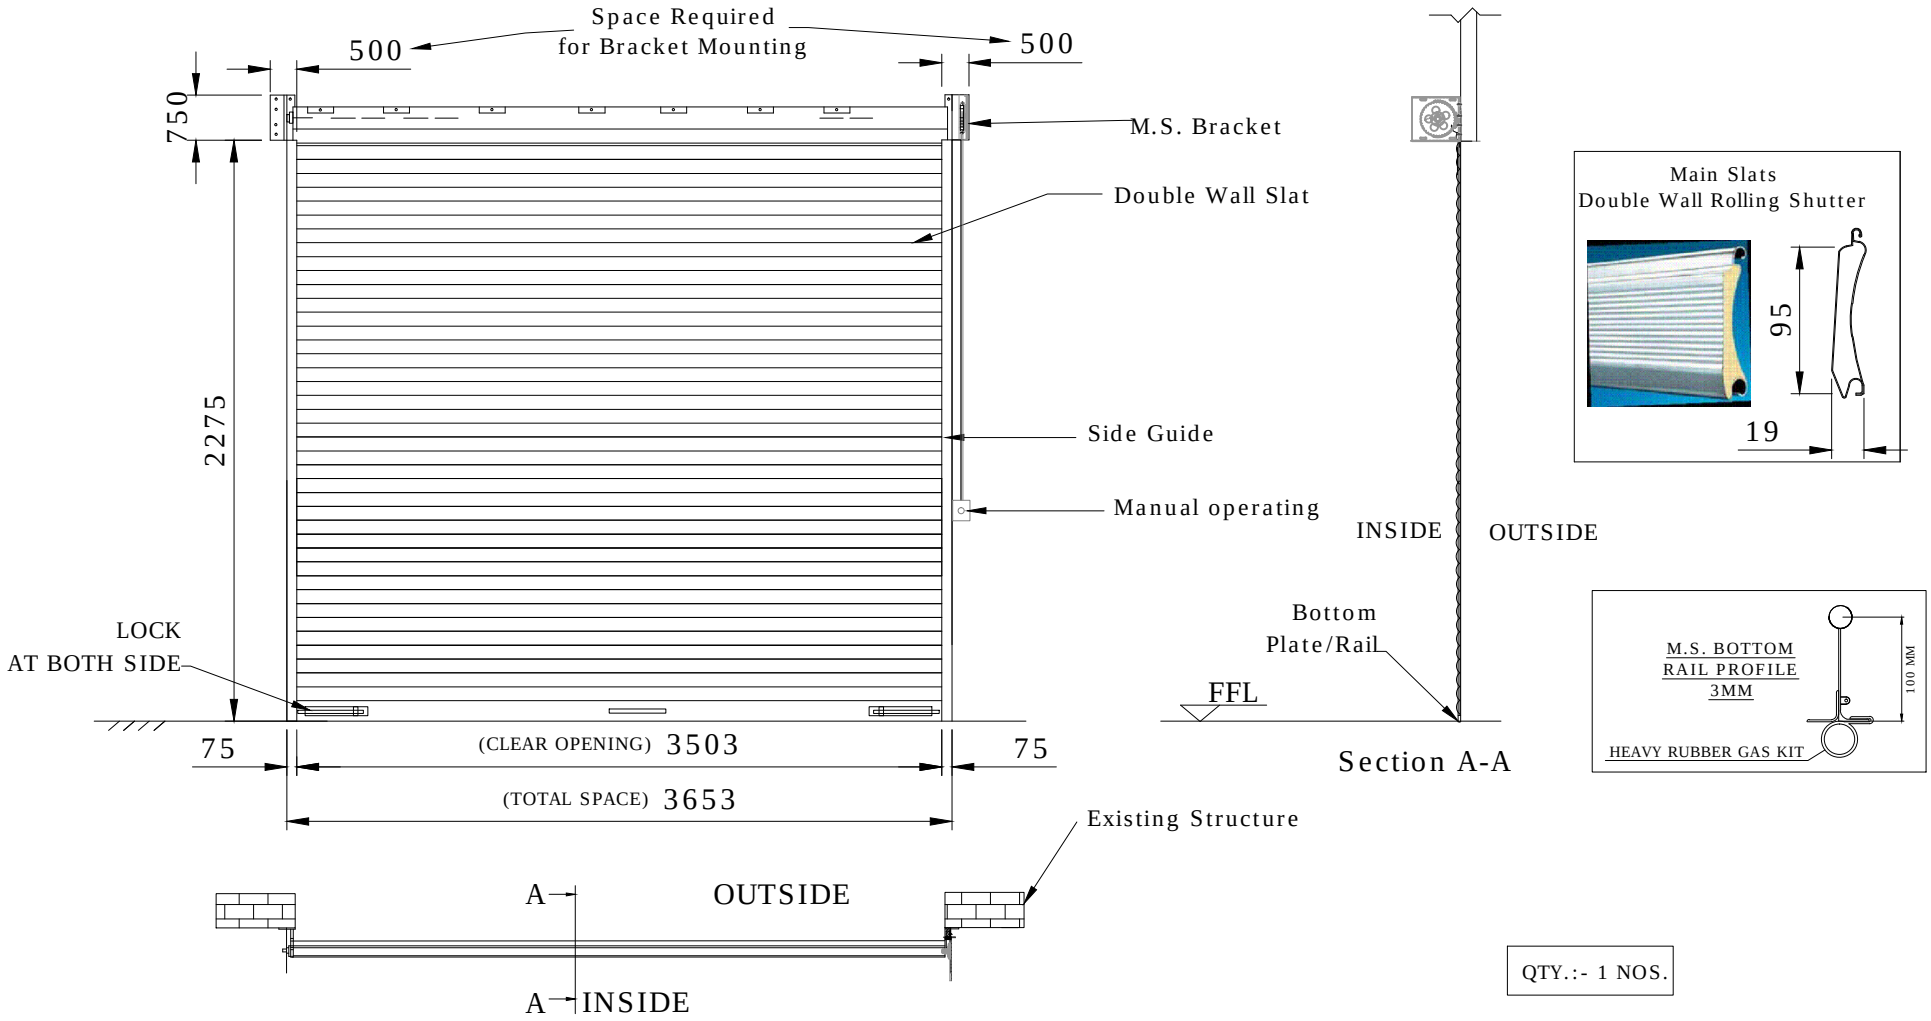


CLEAR OPENING SIZE :- 3503mm x 2275mm

QTY.:- 1 NOS.

This drawing & designing is the property of NIHVA TECHNOLOGIES. Not be sold or copy to any other concern.

TITLE: GEAR OPERATED DOUBLE WALL ROLLING SHUTTER	NIHVA TECHNOLOGIES PVT. LTD.	NIHVA TECHNOLOGY PVT. LTD. PUNE Tel : 020 66304033 Email:- info@nihva.com Website:- www.nihva.com
	SIGN	DATE
DRAWN	ANIL KHOT	08/07/16
CHECK	ANIL	08/07/16
REV.	01	
APPROVAL		
If any queries contact : projects@nihva.com		
ALL DIMENSION ARE IN mm		

CLIENT-PROJECT & SITE MANAGEMENT PVT. LTD		
PROJECT -MERCEDES-BENZ		
SITE -		
DWG. NO. : NIHVA/16-17/0035		
SCALE: NTS	WT:	SHEET: 01 OF 01