

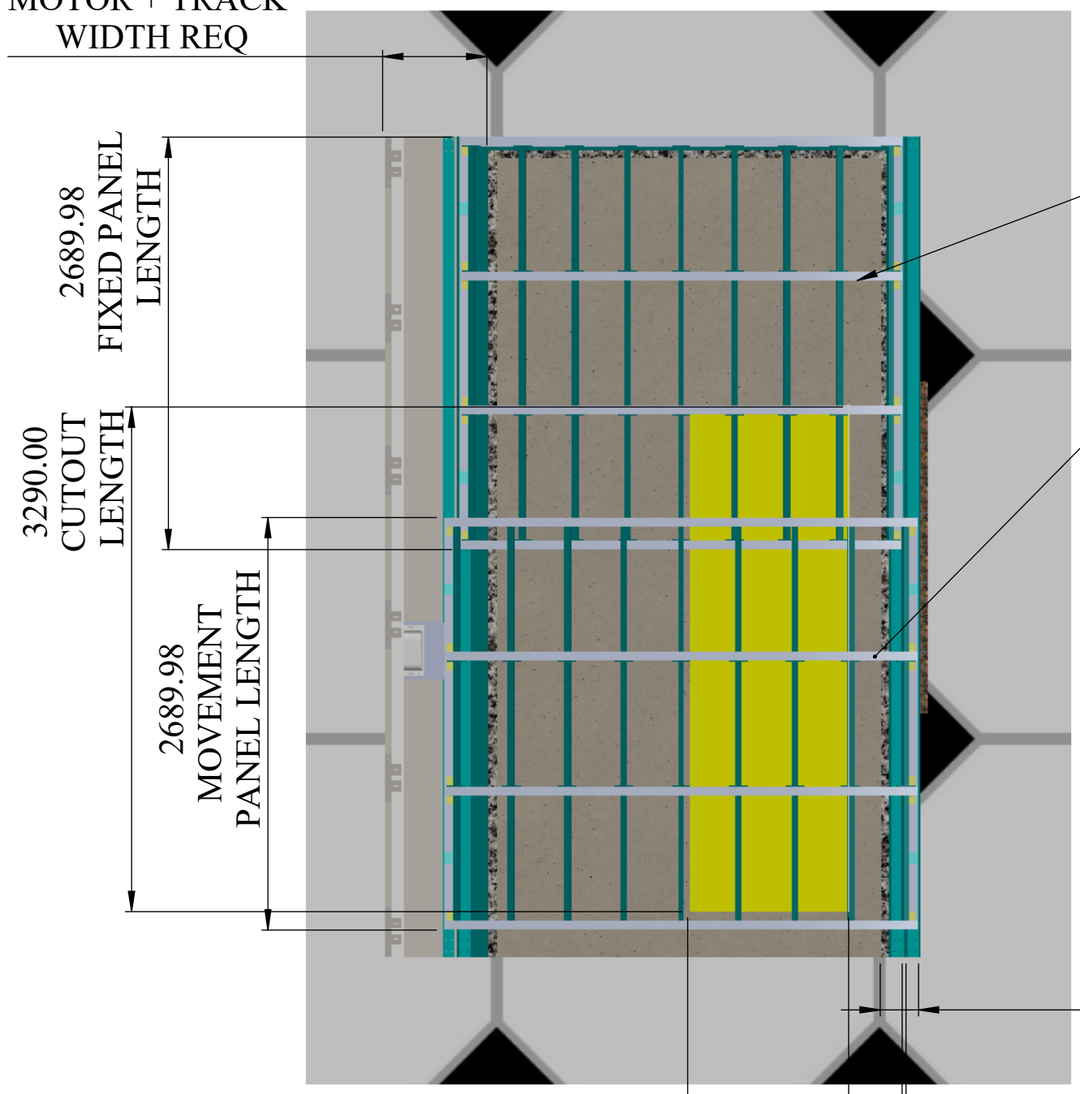


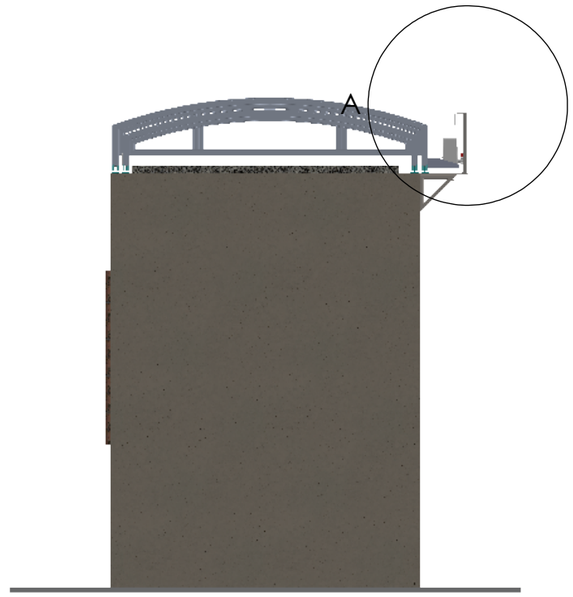

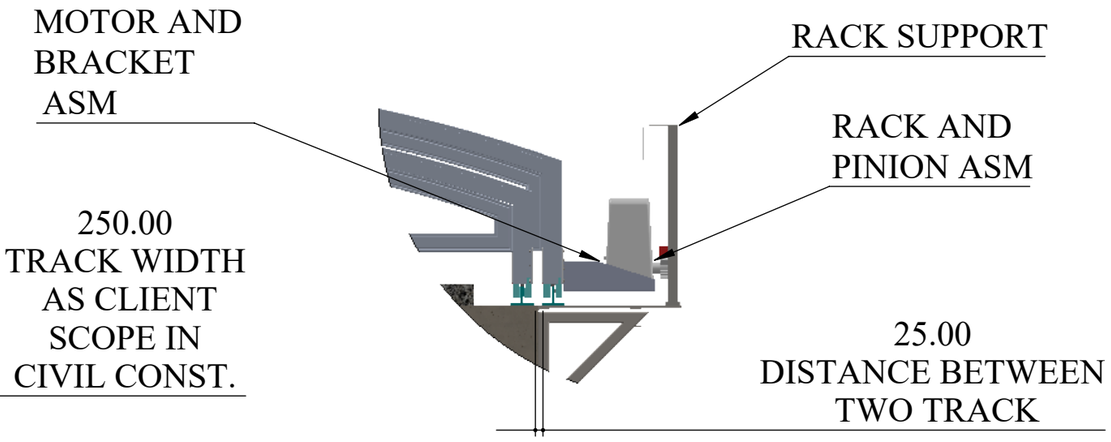

DETAIL A
SCALE 1 : 20


NOTE 01:-


1) IF YOU DO CIVIL WORK FOR TRACK THEN REQUIRED THICKNESS OF CONCERT 200 MM


NOTE 02:-

2) IF YOU DO FABRICATION WORK FOR MOTOR AND TRACK MOUNTING THEN MS PLATE IS REQUIRED,THICKNESS OF PLATE 12 MM IS REQUIRED AT CLIENT SCOPE

TITLE - RETRACTABLE ROOF				NIHVA TECHNOLOGIES PVT.LTD.PUNE Website - www.nihva.com
DWG NO - NTPL			QTY - 1	
	NAME	SIGNATURE	DATE	PROJECT NO - NTPL
DRAWN	V.B.		16-03-2025	PRODUCT - RETRACTABLE ROOF
CHK'D	S.W.		16-03-2025	SITE LOCATION - LUCKNOW
APPV'D	V.T.		16-03-2025	
if any queries contact - supportautomation@nihva.com				REVISION -
ALL DIMENSION ARE IN mm			A3	SCALE - SHEET 1 OF 2

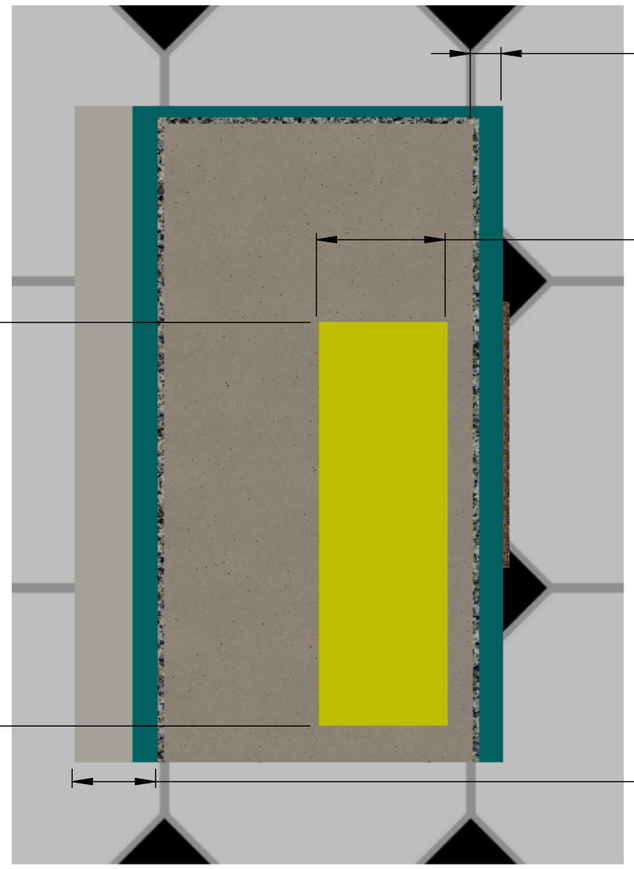

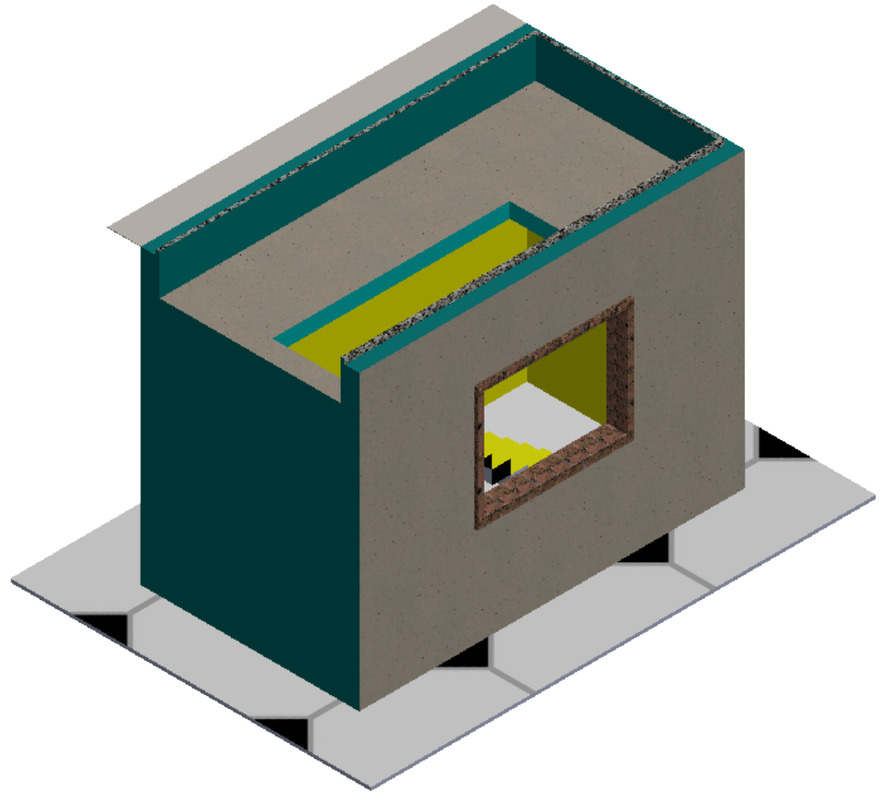

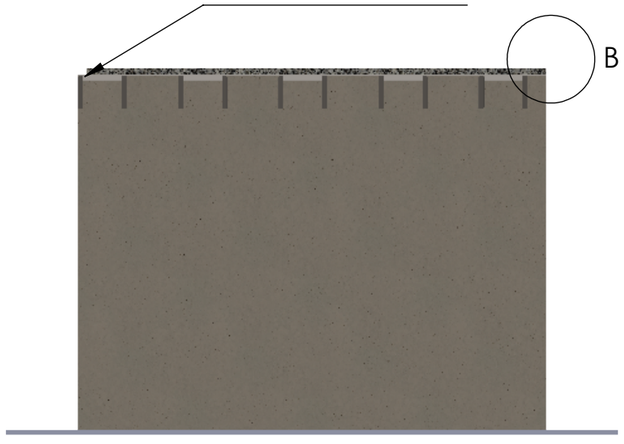

NOTE:-

THE PRESENT WALL WIDTH IS 155MM AND PRESENT COLOUMN SIZE IS FRONT COLOUMN SIDE SIZE 540X250MM AND COLOUMN BACK SIDE SIZE 460X250 MM

I NEED 250 MM WALL WIDTH FOR PROPER PANEL MOUNTING AND ITS MOVEMENT SO ITS NEED TO INCREASE A WALL WIDTH 155 MM TO SAME AS COLOUMN WIDTH 250MM



DETAIL B
SCALE 1 : 10

TITLE - RETRACTABLE ROOF				NIHVA TECHNOLOGIES PVT.LTD.PUNE
DWG NO - NTPL			QTY - 1	Website - www.nihva.com
	NAME	SIGNATURE	DATE	PROJECT NO - NTPL268
DRAWN	V.B.		16-05-25	PRODUCT - RETRACTABLE ROOF
CHK'D	S.W.		16-05-25	SITE LOCATION - LUCKNOW
APPV'D	V.T.		16-05-25	
if any queries contact - supportautomation@nihva.com				REVISION -
ALL DIMENSION ARE IN mm			A3	SCALE - SHEET 2 OF 2