


PROPOSED PLAN LAYOUT

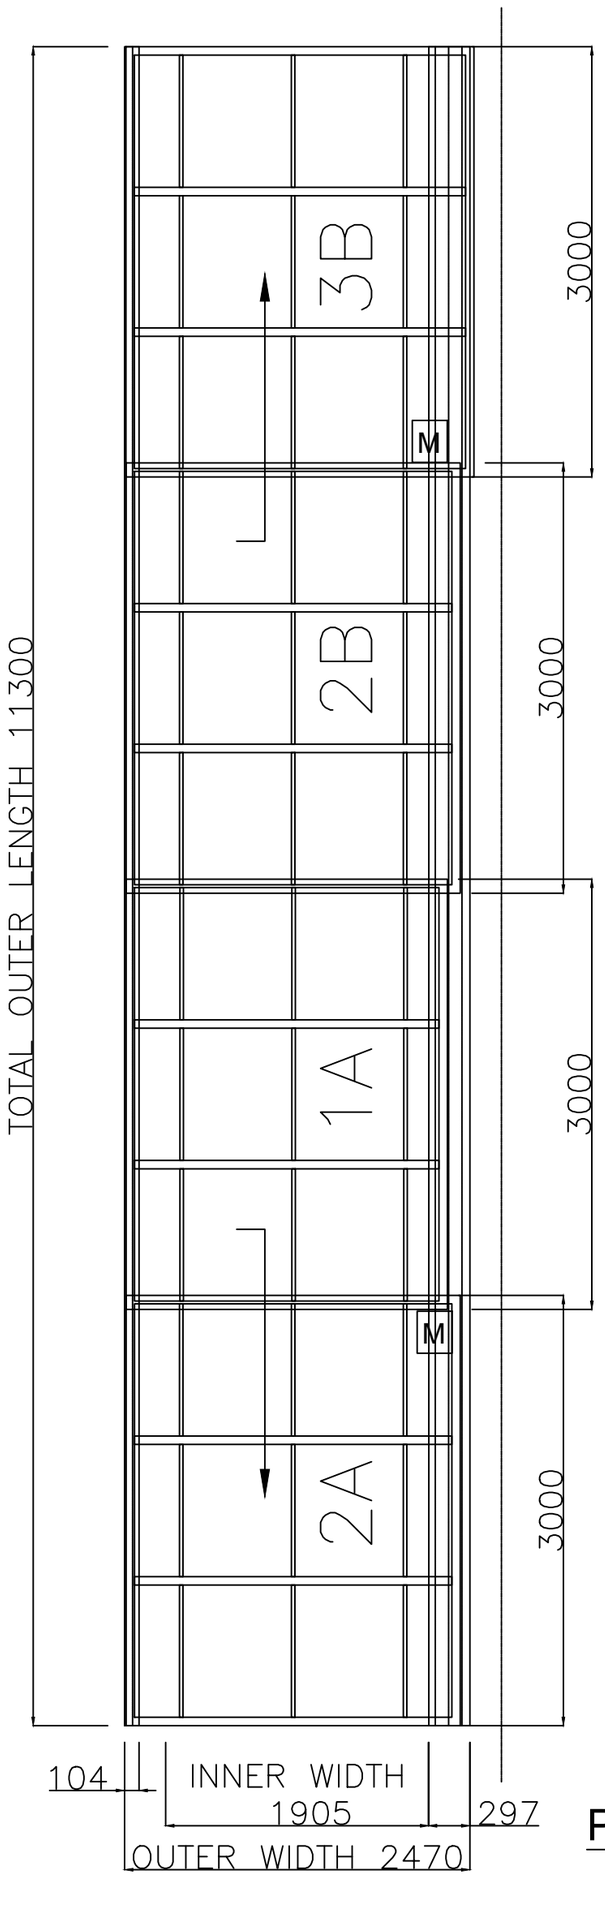

PLAN

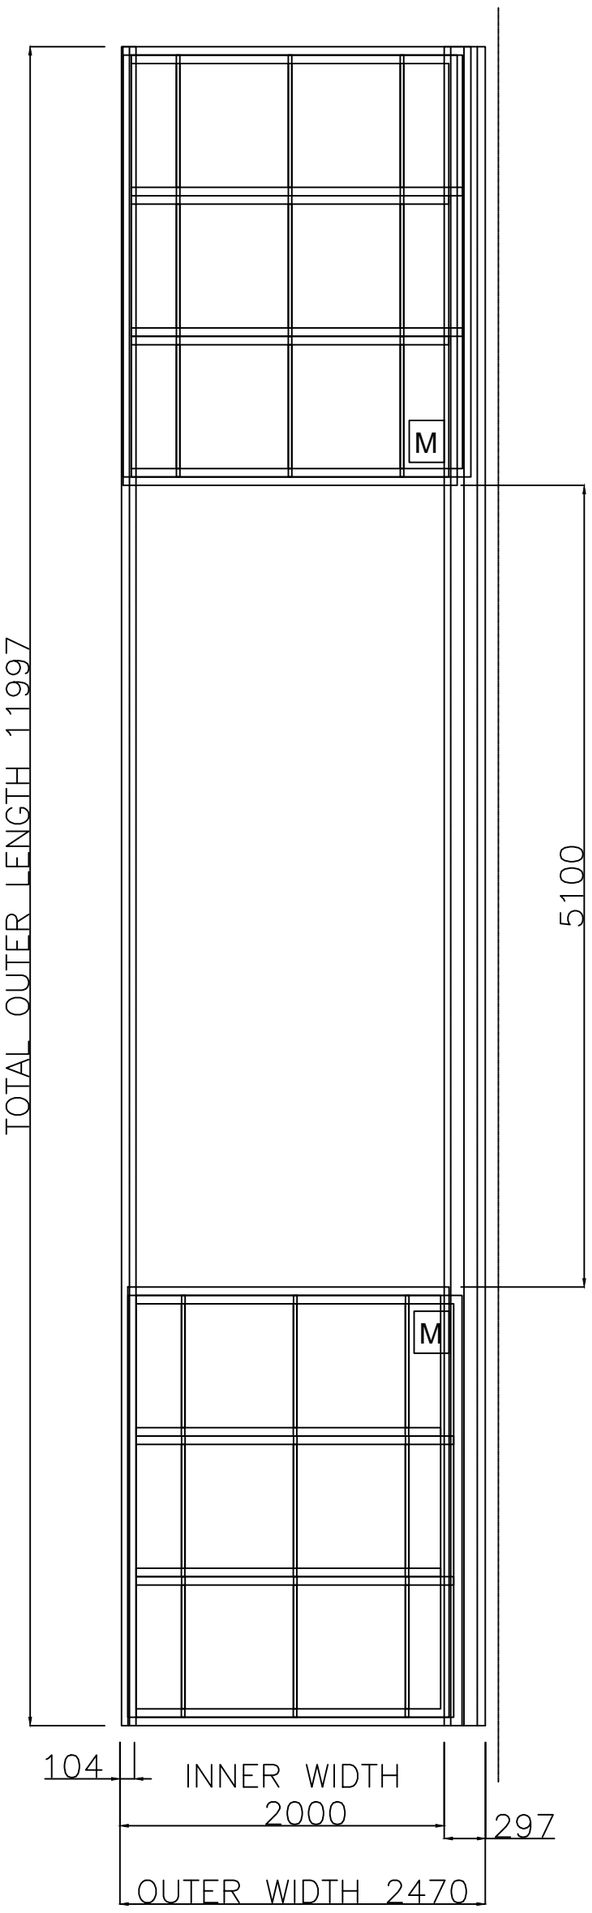

PLAN

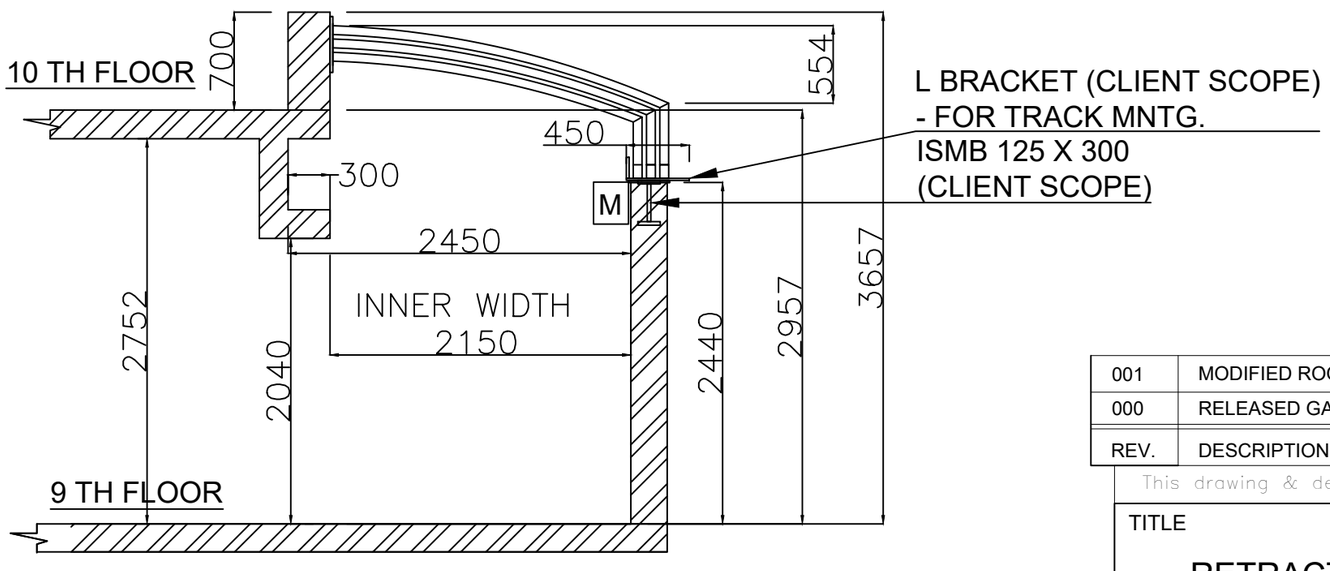

SECTION VIEW

REV.	DESCRIPTION.	REVISED BY	SIGN	DATE
001	MODIFIED ROOF PER SITE VISIT CHANGES & STRUCTURE	MAHESH S.		24.11.22
000	RELEASED GA DWG FOR APPROVAL	MAHESH S.		19.11.22

This drawing & design is the property of NIHVA TECHNOLOGIES. Not to be sold or copied to any other concern.

TITLE

RETRACTABLE ROOF

	NAME	SIGN	DATE
DRAWN	MAHESH S.		19.11.22
CHECK	MAHESH S.		19.11.22
APPRD.	VIJAY T.		19.11.22

NIHVA TECHNOLOGIES PVT. LTD.

NIHVA TECHNOLOGIES PVT. LTD. PUNE
Tel : 020 66304033
Email:- info@nihva.com
Website:- www.nihva.com

CLIENT - MR. SAMEER MEHTA

PROJECT - RETRACTABLE ROOF

SITE LOCATION- JAMUNA NIKETAN

If any queries contact : projectsautomation@nihva.com

NIHVA\22-23\00XX

REV- 0

ALL DIMENSION ARE IN mm

SCALE: NTS

SHEET: 01 OF 01