

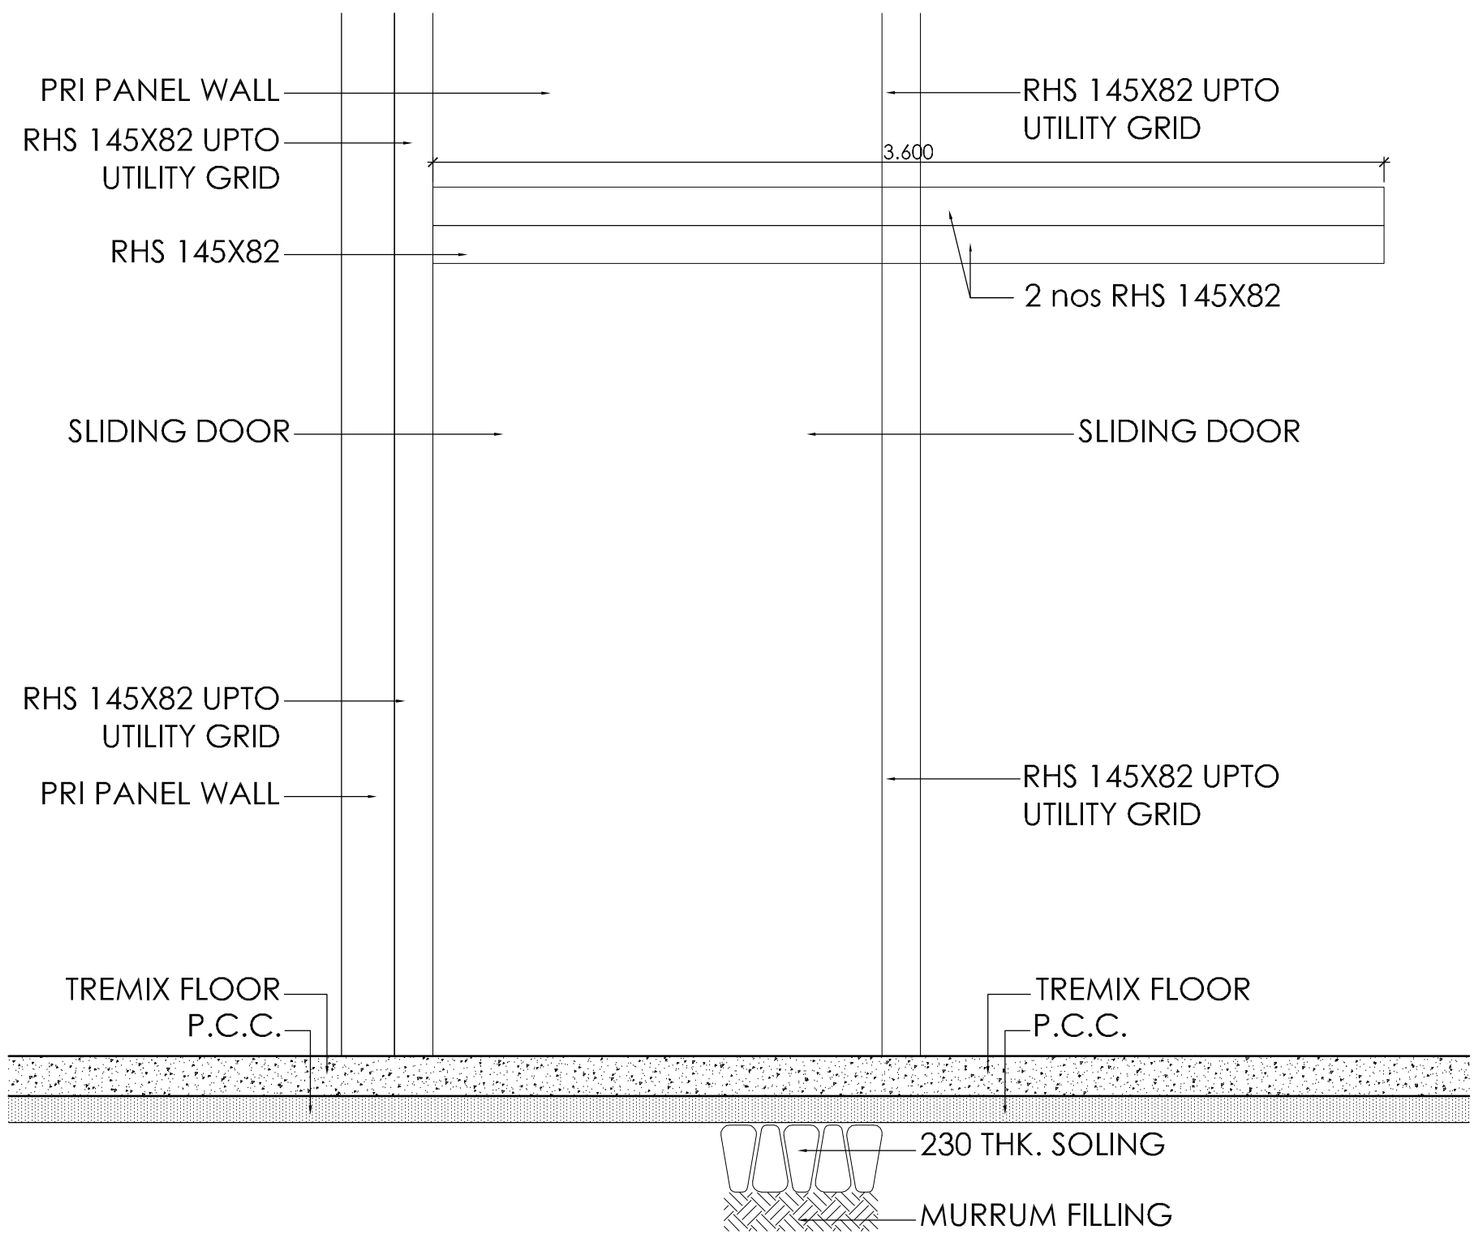



SLIDING DOOR FARMING ELEVATION

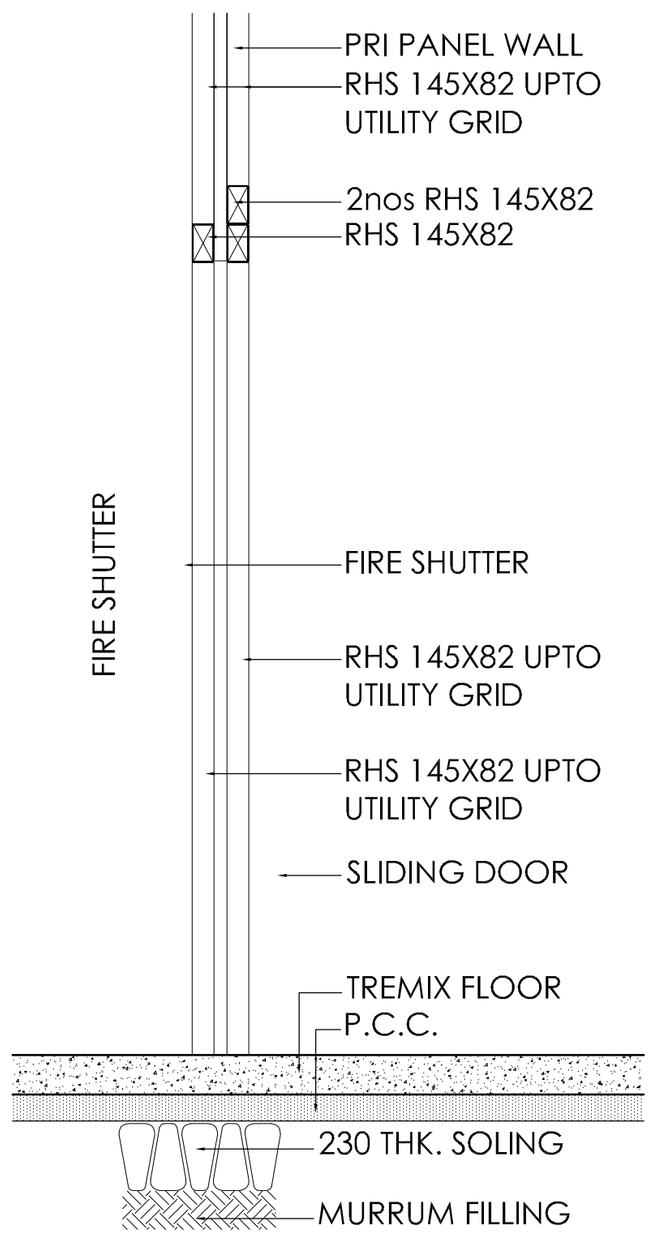

CROSS SECTION

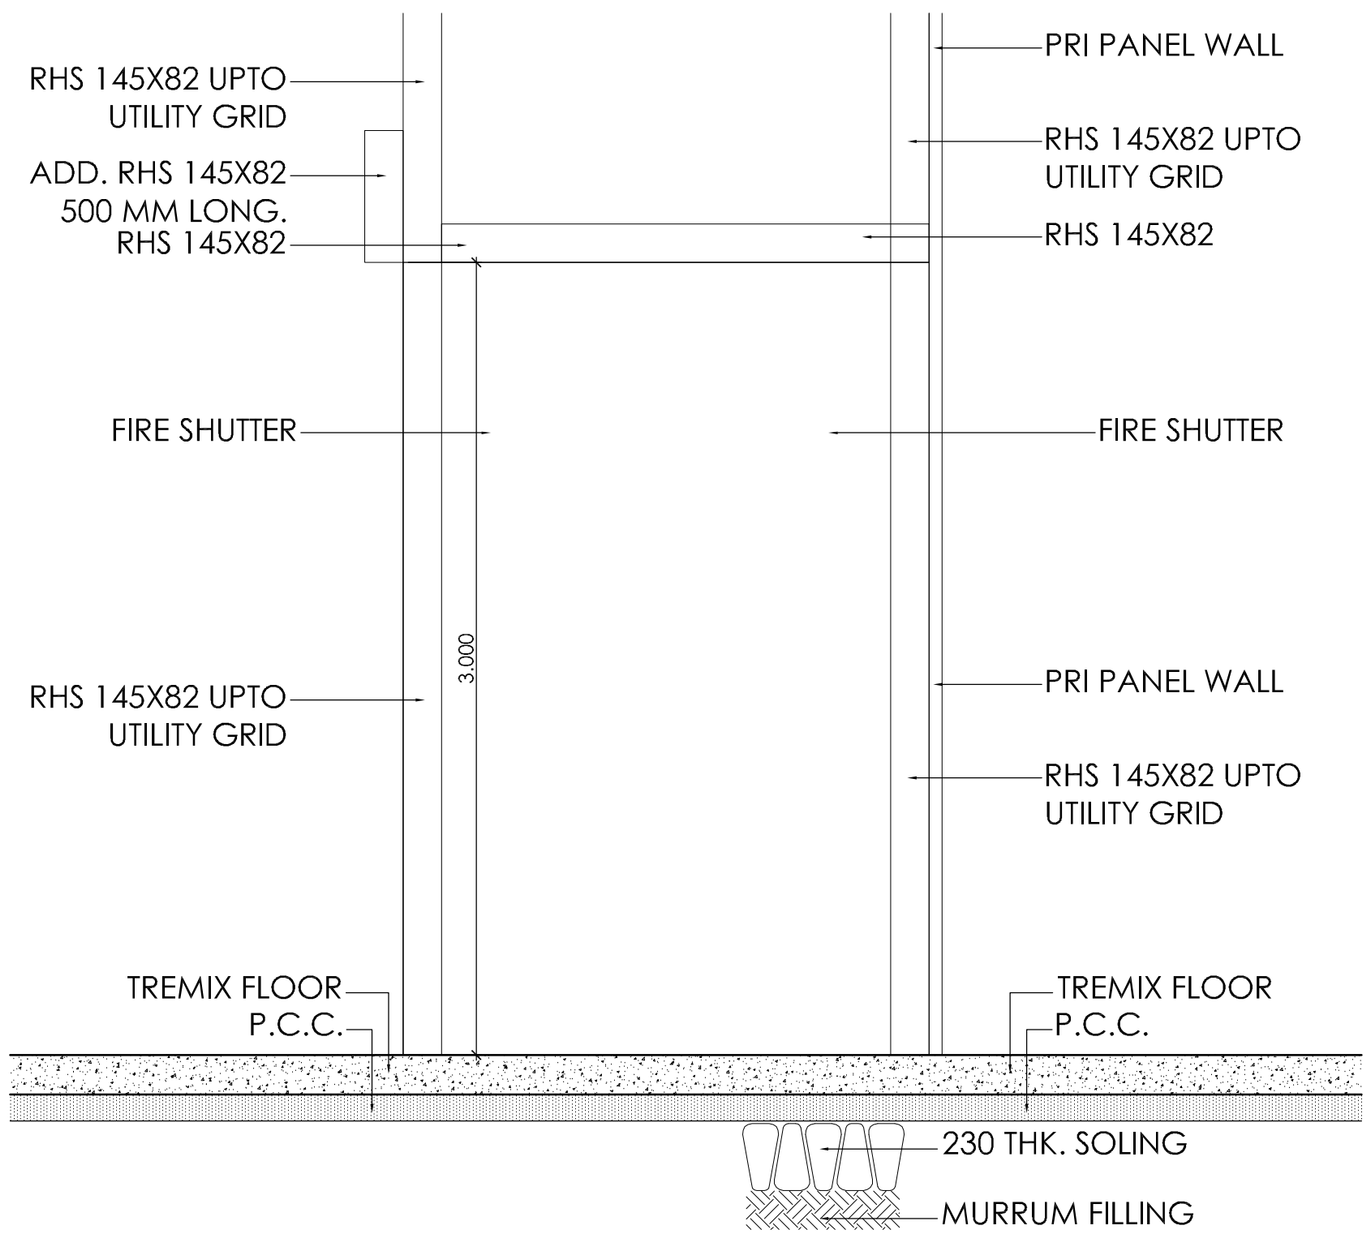

FIRE SHUTTER FARMING ELEVATION

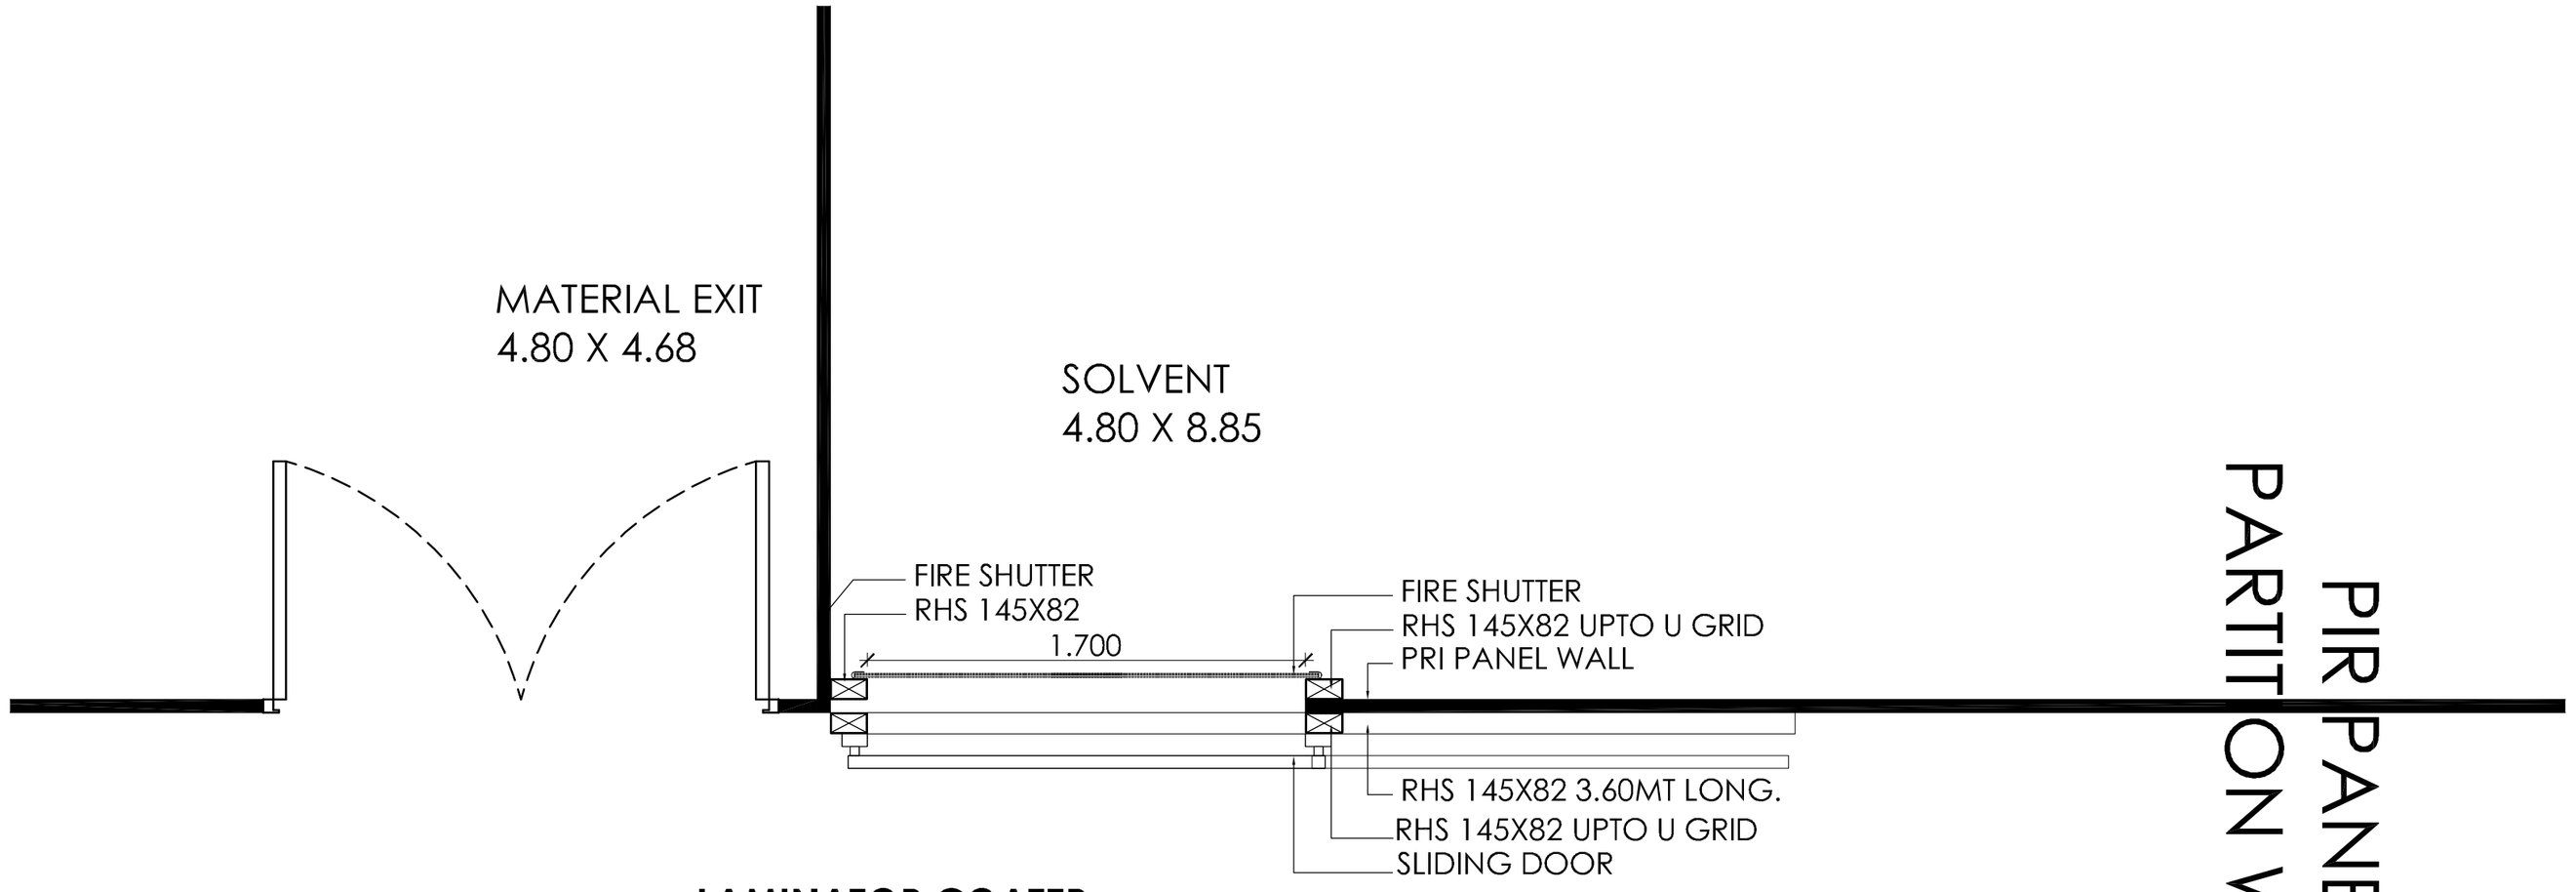

LAMINATOR COATER

SLIDING DOOR & FIRE SHUTTER FARMING PLAN

PROJECT

PROPOSED PLANT AT PLOT NO. B-38/1, CHAKAN INDUSTRIAL AREA, PH-II, VASULI, KHED, PUNE.
FOR PACK TIME INNOVATIONS PVT LTD.

TITLE

GROUND FLOOR SOLVENT MIX ROOM DOOR FARMING DETAILS

G.A. DRAWING :- ☐		REFERENCE DRG :- ☐	
APPROVAL DRG :- ☑		GFC. DRAWING :- ☐	
DATE	SCALE	DRG. NO	JOB. NO	NORTH
04.10.2017	1 : 30	S.MIX - 01	PTI-1508	
	Drn :Motiram	Chd :RSS		

Dandekar and Associates
ARCHITECTS - ENGINEERS
FLAT NO 4, AVIVA APT. LANE NO. 3 PRABHAT RD, ERANDWANA
PUNE-411004.PH.25667050/4358 Email- dandekar.pti@gmail.com

\\Main-pc\ad\AD\PTI\DRAWING\WD\3001.dwg Nihva Door