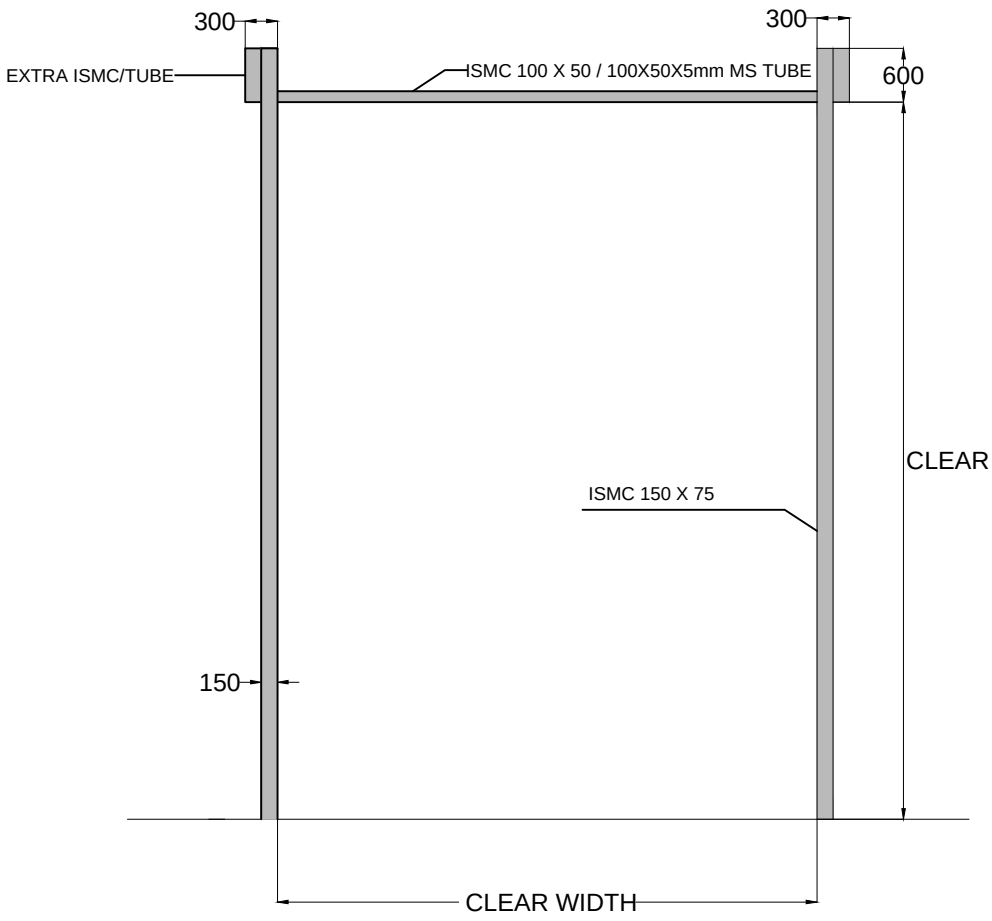


STRUCTURE FOR MOTORIZED ROLLING SHUTTER. (SIZE 4 X 5)

NOTE :

1. MATERIAL FOR ALL STRUCTURE = M.S
2. ALL CIVIL WORK WILL BE IN CLIENT SCOPE.
3. REQUIRED STEEL STRUCTURE IN CLIENT SCOPE.

CLEAR WIDTH	CLEAR HEIGHT	QTY.
4000mm	5000mm	01 NO

TOLERANCE - ±10mm

This drawing & design is the property of NIHVA TECHNOLOGIES. Not to be sold or copied to any other concern.

TITLE
STRUCTURE FOR GEAR OPERATED ROLLING SHUTTER

	NAME	SIGN	DATE
DRAWN	P.A		21.01.19
CHECK	V.T		21.01.19
APPRD.			

If any queries contact : design@nihva.com

ALL DIMENSION ARE IN mm

NIHVA
NIHVA TECHNOLOGIES PVT. LTD.
NIHVA TECHNOLOGIES PVT. LTD. PUNE
Tel : 020 66304033
Email:- info@nihva.com
Website:- www.nihva.com

CLIENT - ESR, PUNE

PROJECT- BMW

SITE LOCATION - CHAKAN

DWG. NO. : NIHVA/18-19/0253 | REV- 00

SCALE: NTS | WT: | SHEET: 01 OF 01