



SECTION-X

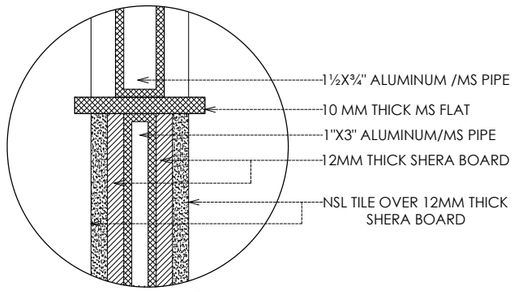


DETAIL-2

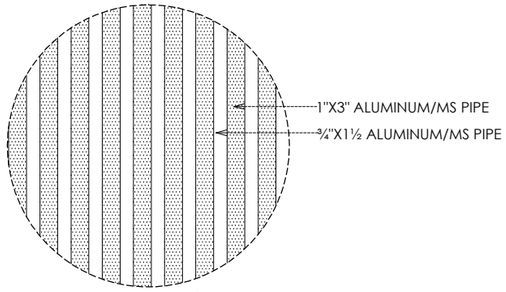


DETAIL-3




REFERENCE IMAGE

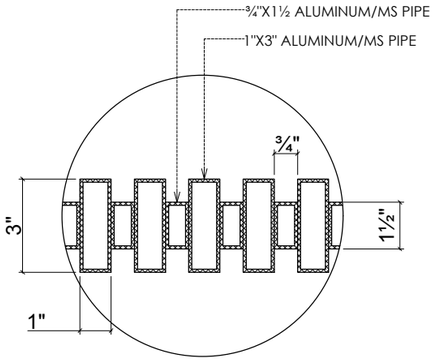


DETAIL-1

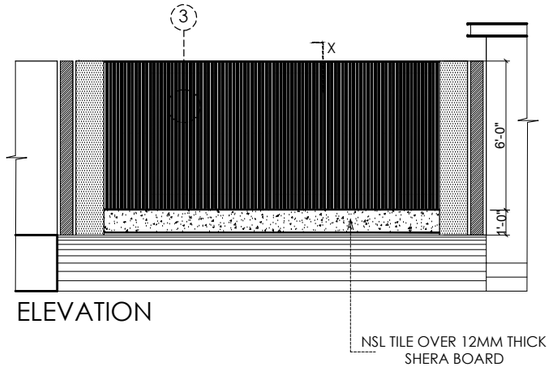

ELEVATION

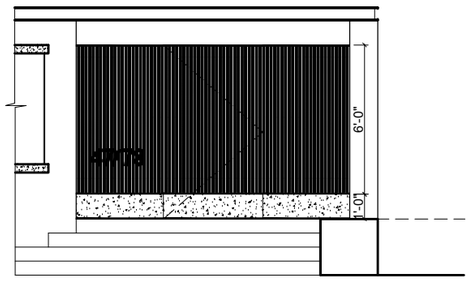

ELEVATION

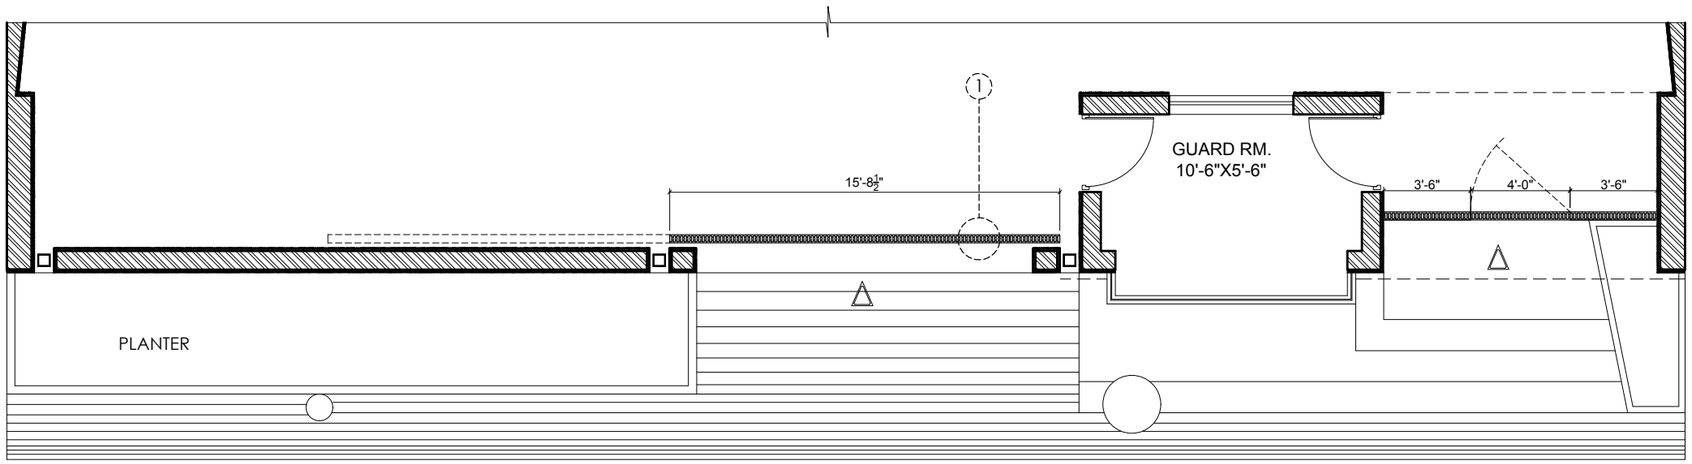

PLAN

THE DESIGN FORUM
ARCHITECTS, PLANNERS, INTERIOR DESIGNERS
B-179, GREATER KAILASH-1, NEW DELHI-110048
PH. NOS.: 011-46516807, 011-46015363
Email:- thedesignforum@gmail.com
Instagram:- thdedesignforum_1988

NOTE:
1. THIS DRAWING IS THE PROPERTY AND COPYRIGHT OF M/S THE DESIGN FORUM AND IS NOT TO BE COPIED OR USED IN ANY WAY WITHOUT THEIR PRIOR WRITTEN PERMISSION.
2. ALL DIMENSIONS TO BE READ AND NOT TO BE MEASURED.

REVISIONS:

00.00.00	XYZ
00.00.00	XYZ
00.00.00	XYZ
00.00.00	XYZ

ORIENTATION:

SITE ADDRESS:
47/78
PUNJABI BAGH

CLIENT:
MR. SANJAY SINGHLA

DESCRIPTION:
STILT FLOOR

DRAWING TITLE:
GATE DETAIL

DRAWING NO.:	**DATE:**
TDF/PL-03/5	31-05-2022
DRAWN BY:	**CHECKED BY:**
MOHD. RAFIK	