


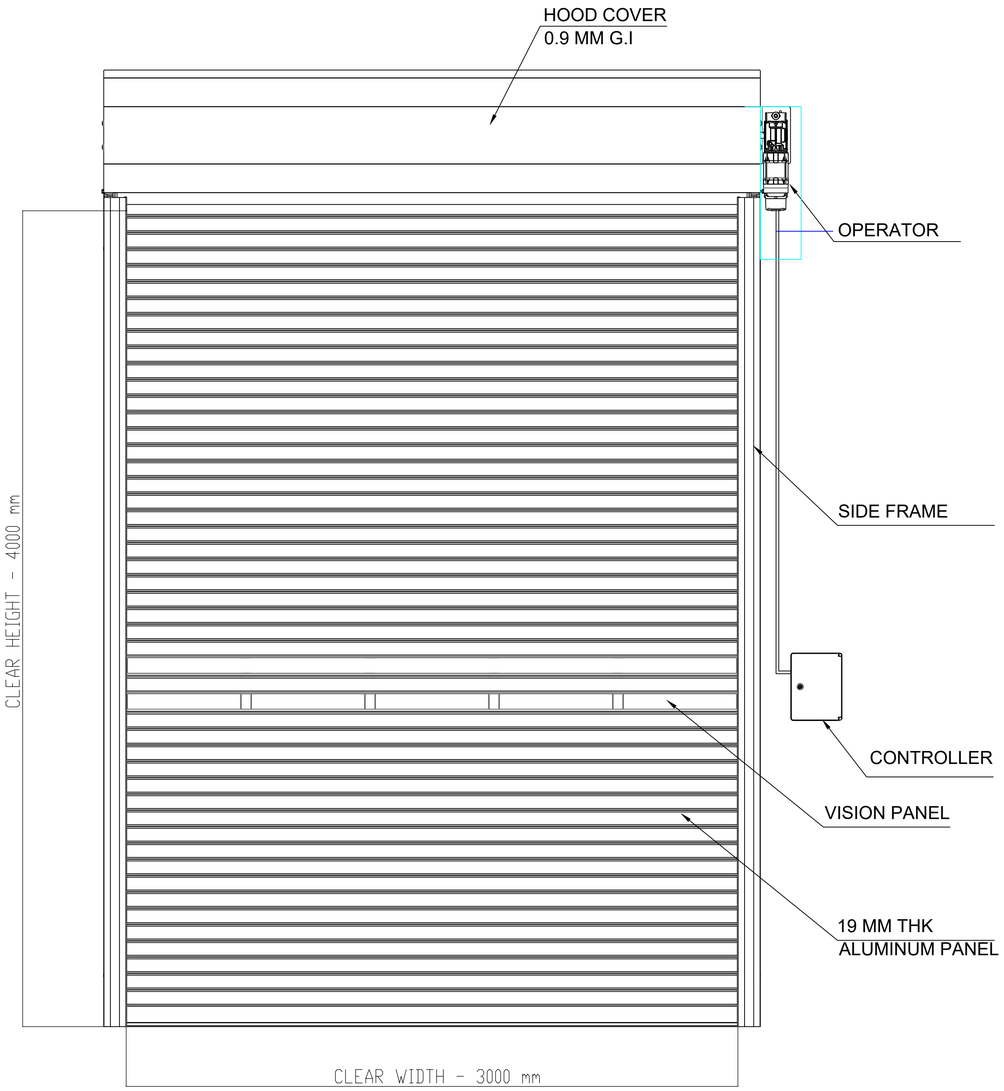


ELEVATION

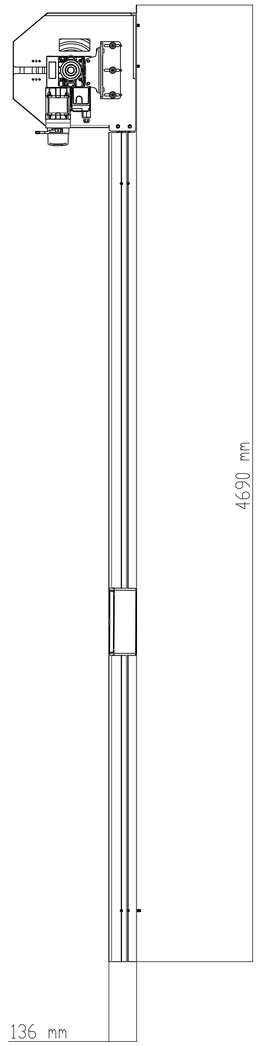

SIDE VIEW

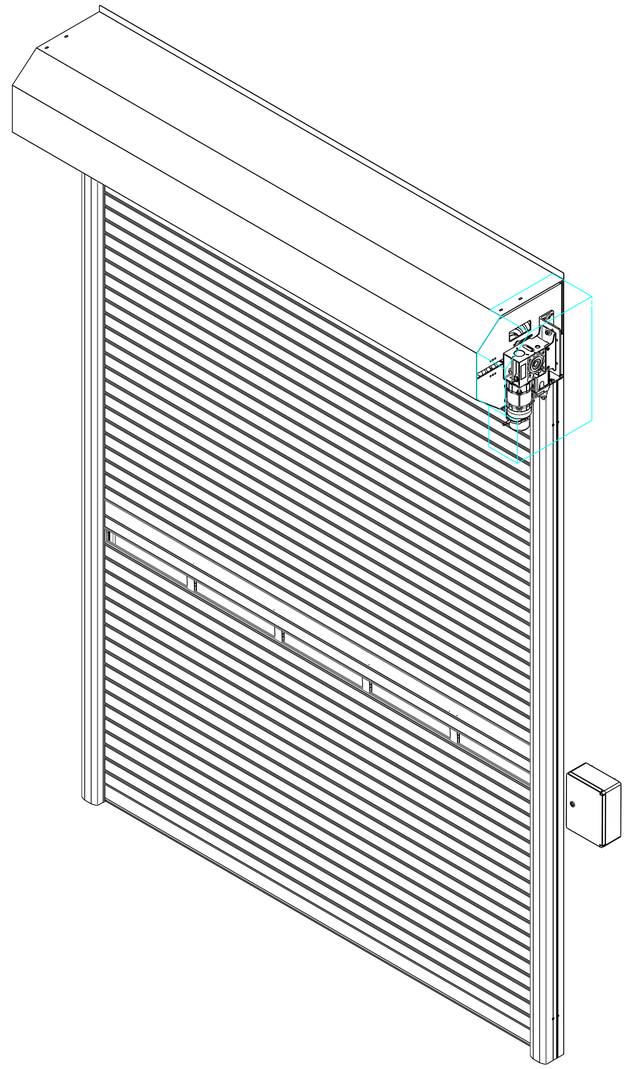

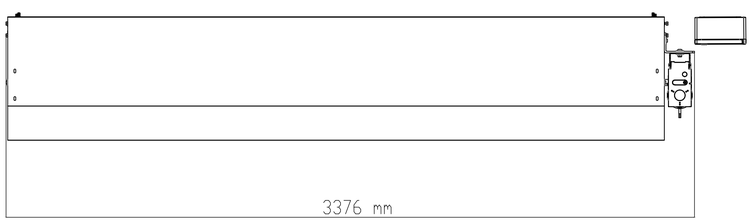

TOP VIEW

NOTES:
1. COLOR : RAL 9006
2. SAFETY DEVICE : PHOTOCELL & SAFETY EDGE
3. RADAR : PAIR OF RADAR SENSOR & LOOP DETECTOR - 02 NOS.
4. MANUAL ACTIVATION : CRANK HANDLE

DOOR QTY : 2 NOS.

This drawing & design is the property of NIHVA TECHNOLOGIES. Not to be sold or copied to any other concern.

TITLE
ALUMINUM HIGH SPEED ROLLING SHUTTER

NIHVA TECHNOLOGIES PVT. LTD.

NIHVA TECHNOLOGIES PVT. LTD. PUNE
Tel : 020 66304033
Email:- info@nihva.com
Website:- www.nihva.com

	NAME	SIGN	DATE
DRAWN	MAHESH S.		24.08.2022
CHECK	MAHESH S.		24.08.2022
APPRD.	AMIT K.		24.08.2022

CLIENT - AMULYA TRADERS
PROJECT - JOHN DEERE
SITE LOCATION - PUNE.

If any queries contact : sales@nihva.com | DWG. NO. : NIHVA/22-23/CLT/0114 | REV- 0

ALL DIMENSION ARE IN mm | SCALE: NTS | WT: | SHEET: 01 OF 01