ROOF PLAN

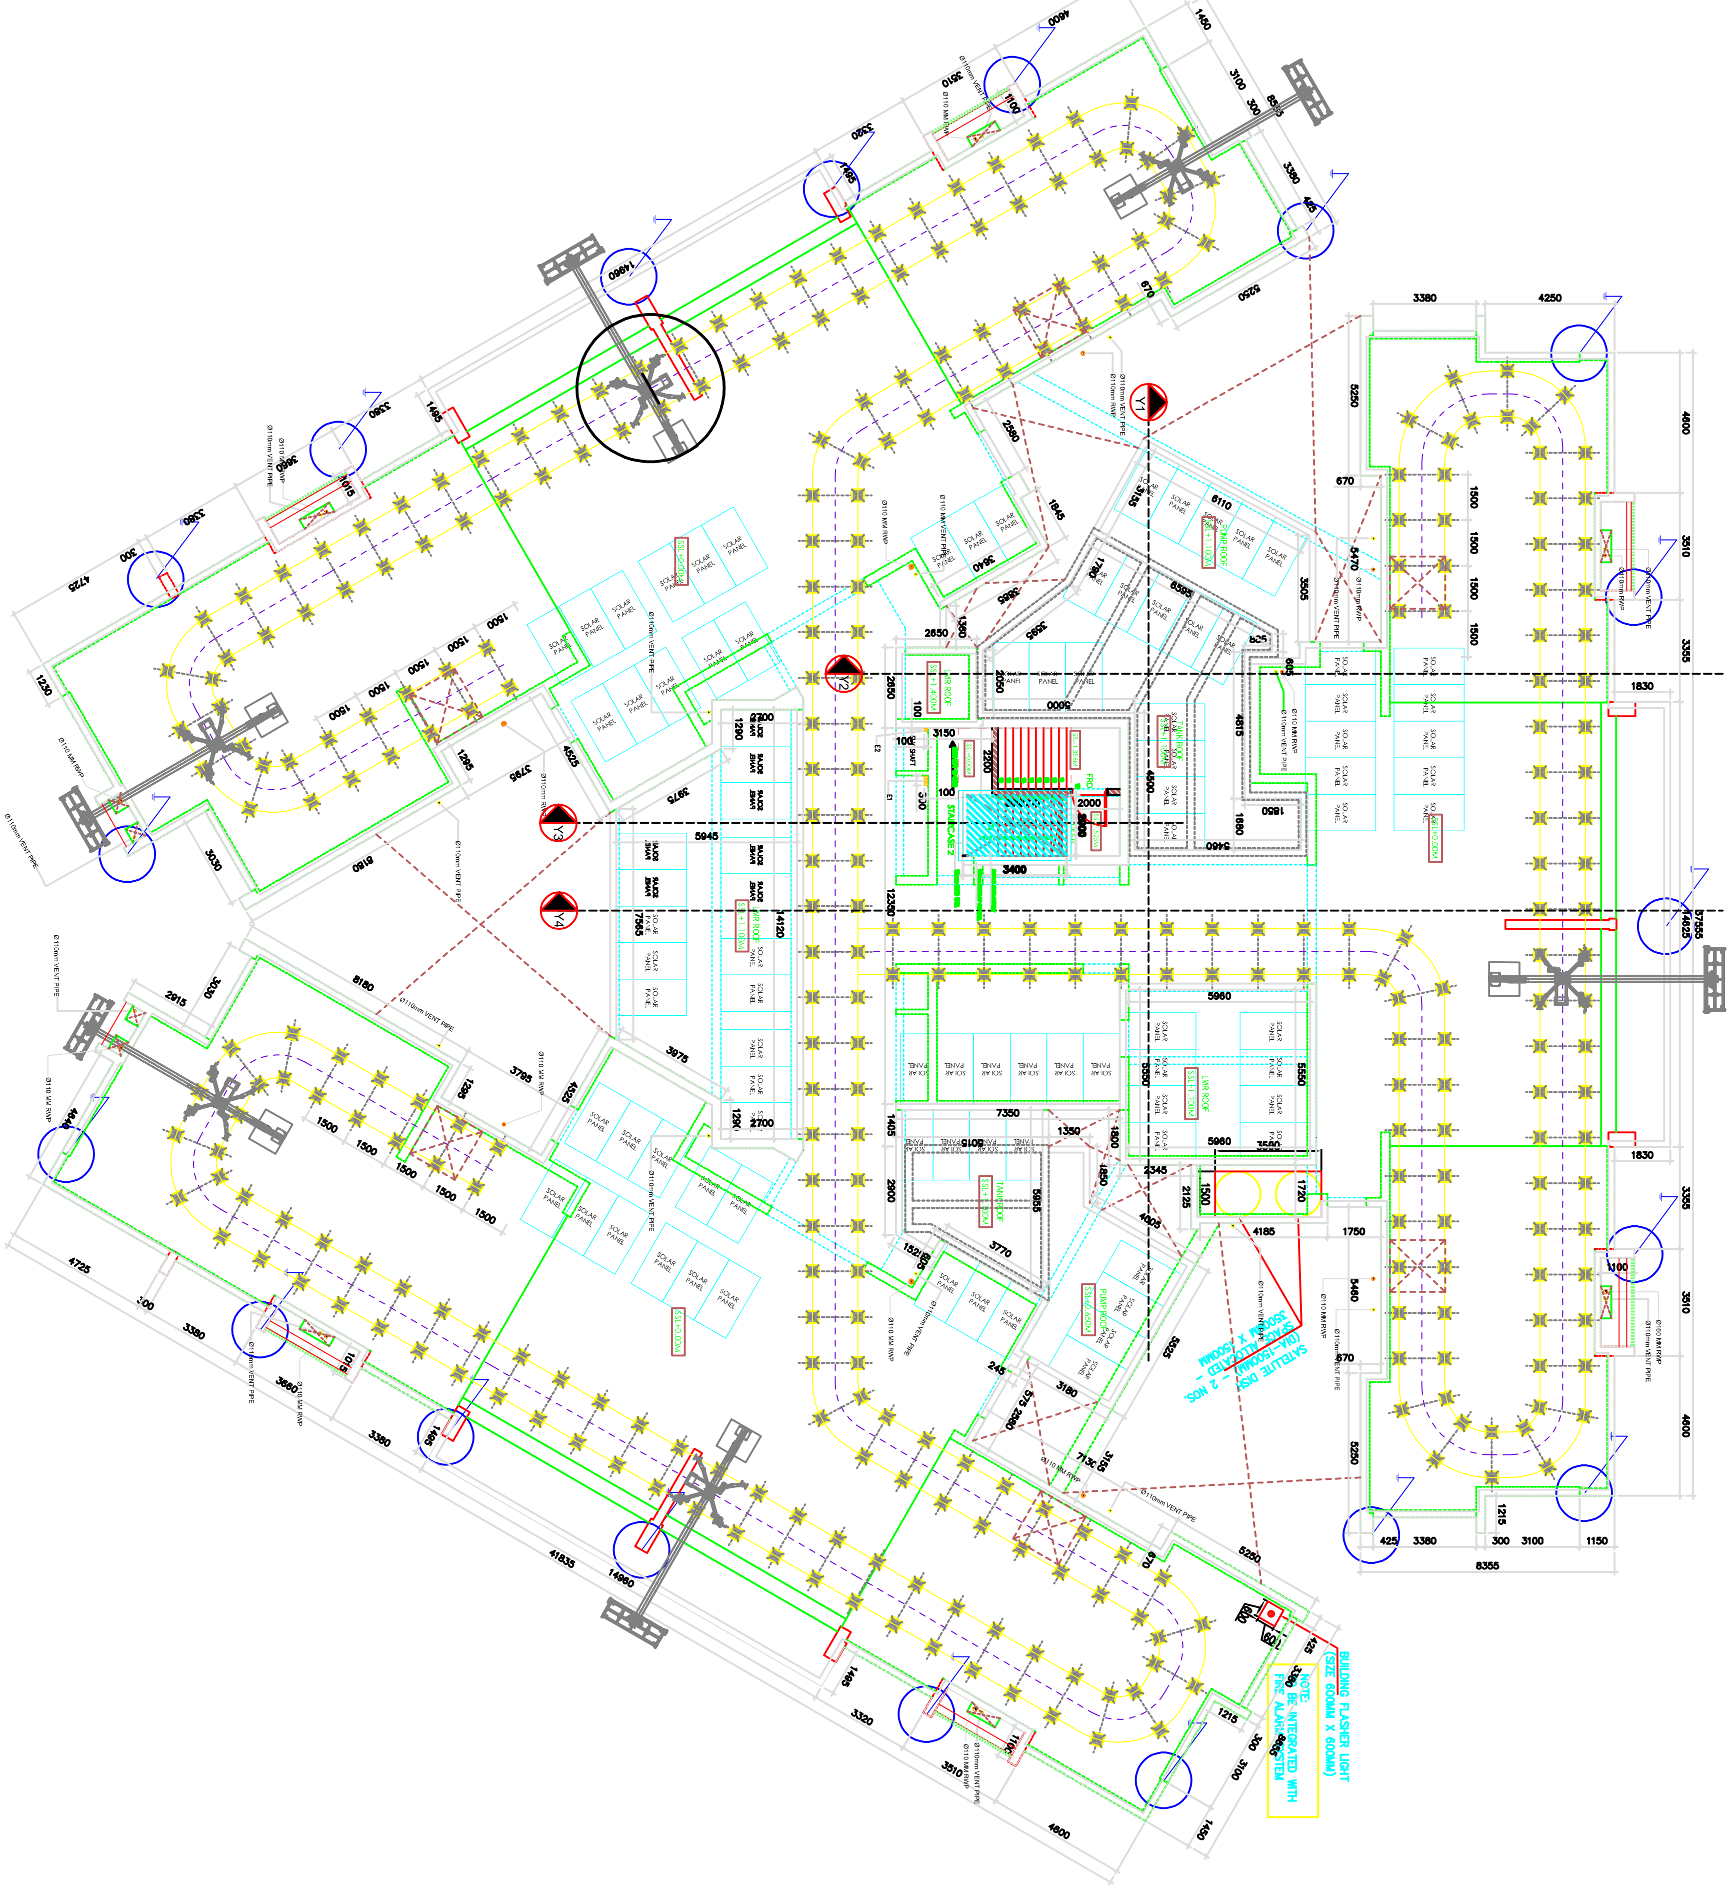
SATELLITE DISH (DIA-1500MM) - 2 NOS.
SPACE ALLOCATED - 3500MM X 1500MM
BUILDING FLASHER LIGHT (SIZE 600MM X 600MM)
NOTE: TO BE INTEGRATED WITH FIRE ALARM SYSTEM
LMR ROOF
SOLAR PANEL
Ø110mm VENT PIPE
Ø110 MM RWP
Y1
Y2
Y3
Y4
41835
14690
8355
5960
4185
1750
5250
5460
3380
4250
4600
3510
3355
1830
4725
3030

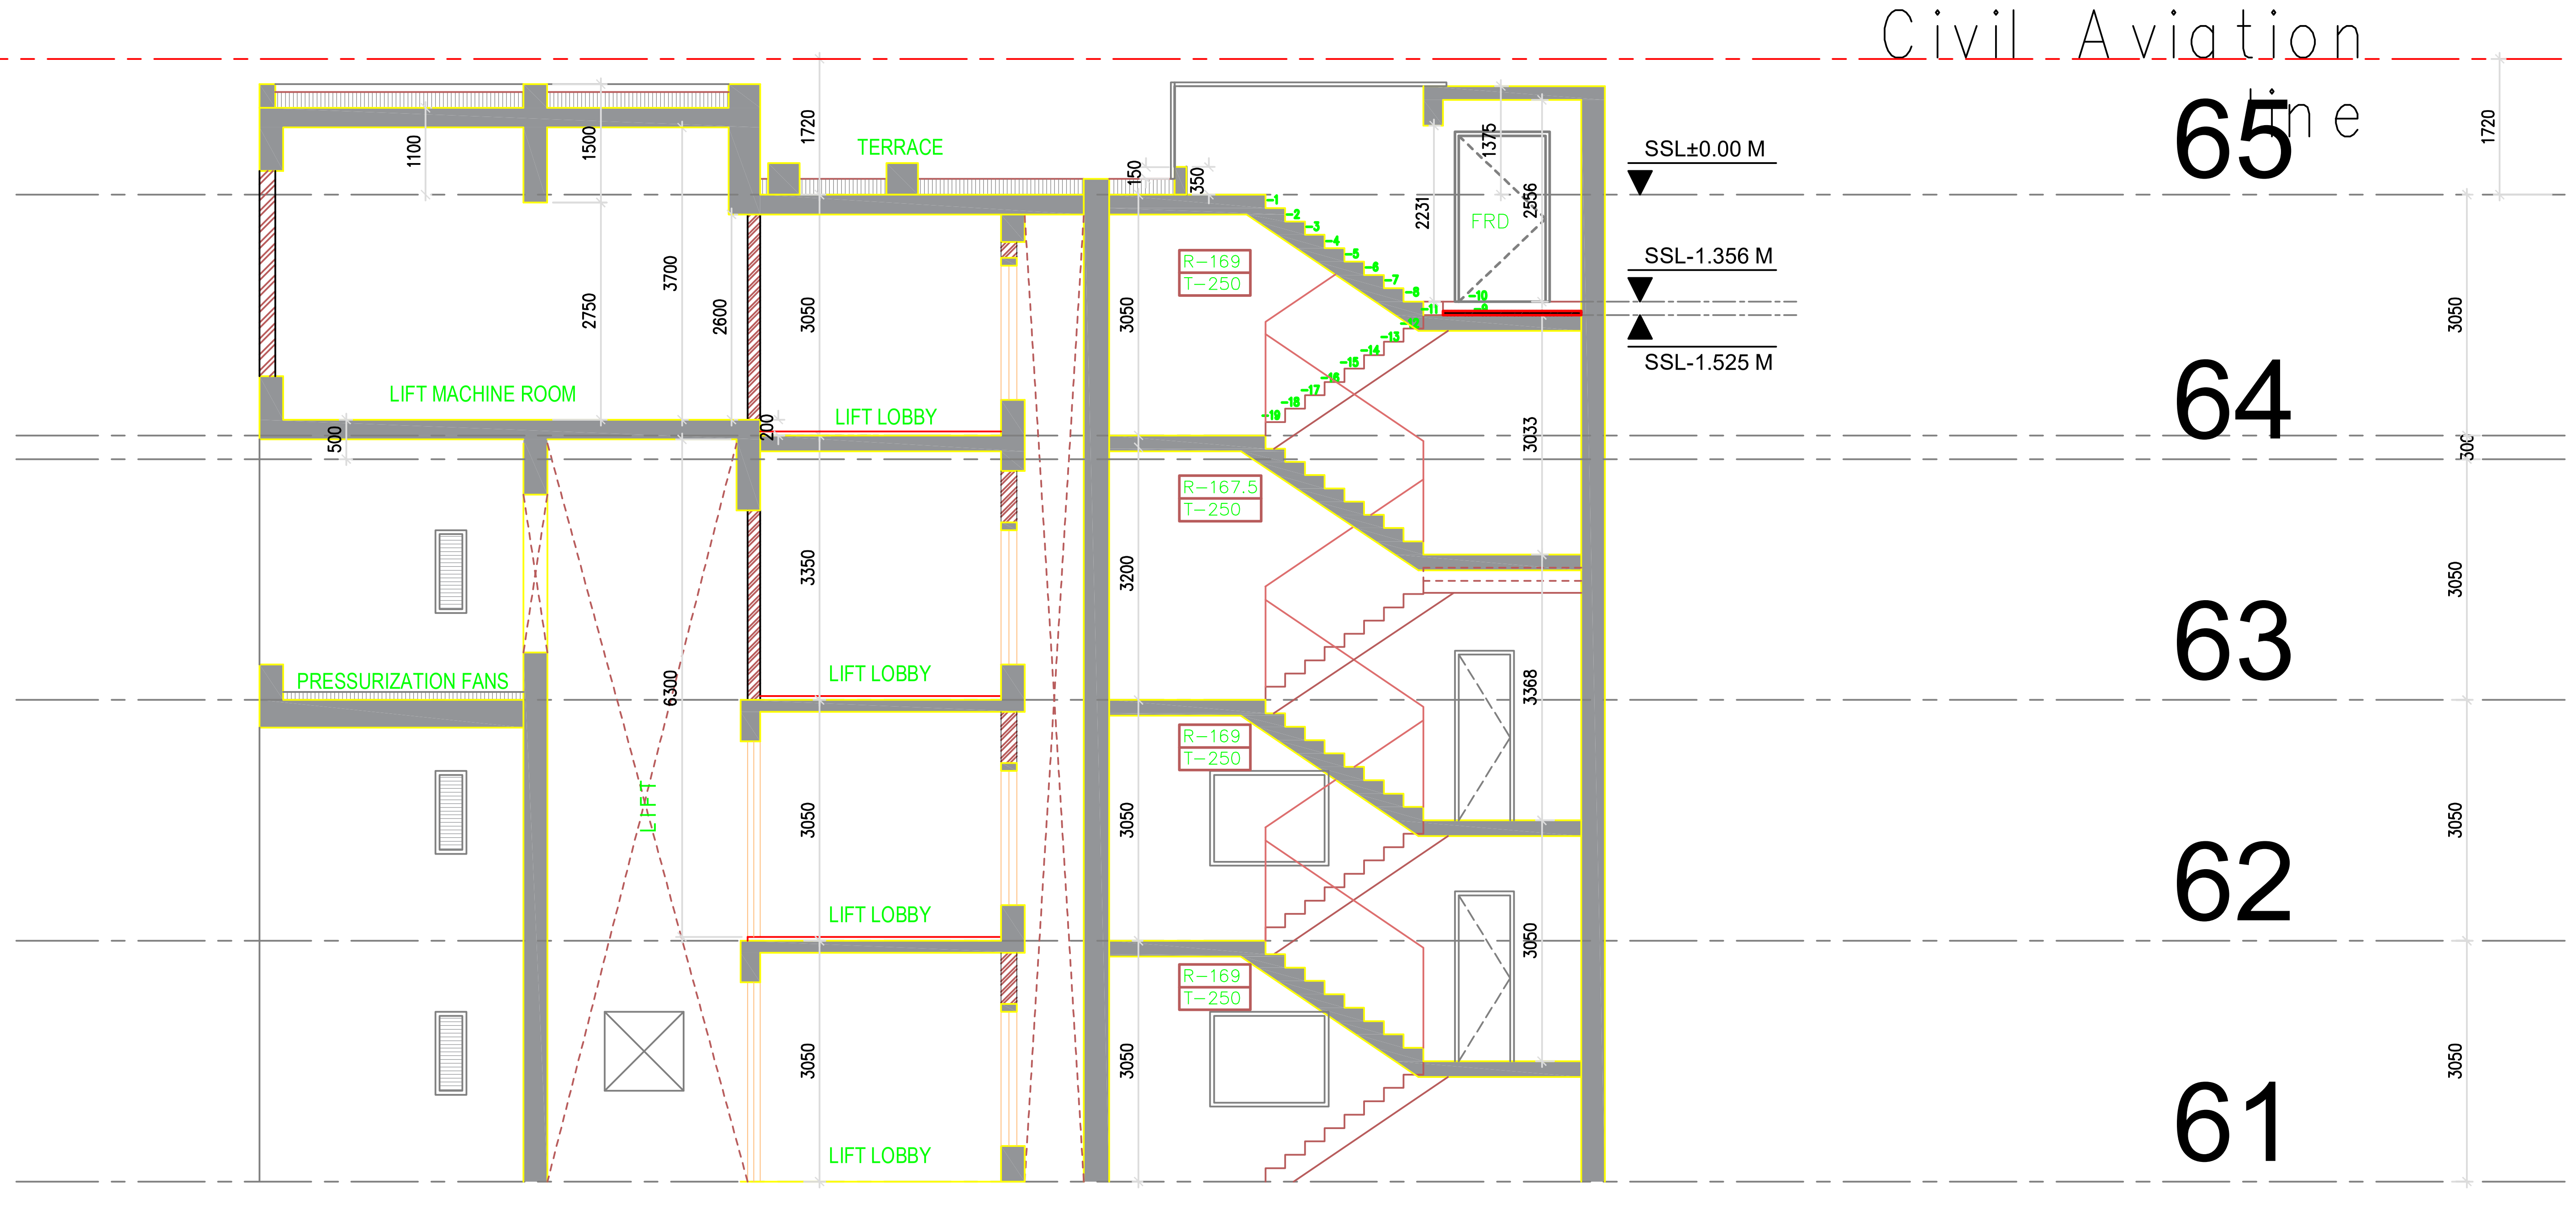
Civil Aviation Line
65
64
63
62
61
SSL±0.00 M
SSL-1.356 M
SSL-1.525 M
LIFT MACHINE ROOM
PRESSURIZATION FANS
LIFT
TERRACE
LIFT LOBBY
LIFT LOBBY
LIFT LOBBY
LIFT LOBBY
FRD
R-169
T-250
R-167.5
T-250
R-169
T-250
R-169
T-250
1100
1500
2750
3700
2600
6300
500
200
1720
3050
3350
3050
3050
3200
150
350
2231
1375
2556
3033
3368
3050
300
1720

SECTION-Y3