

PRODUCED BY AN AUTODESK EDUCATIONAL PRODUCT

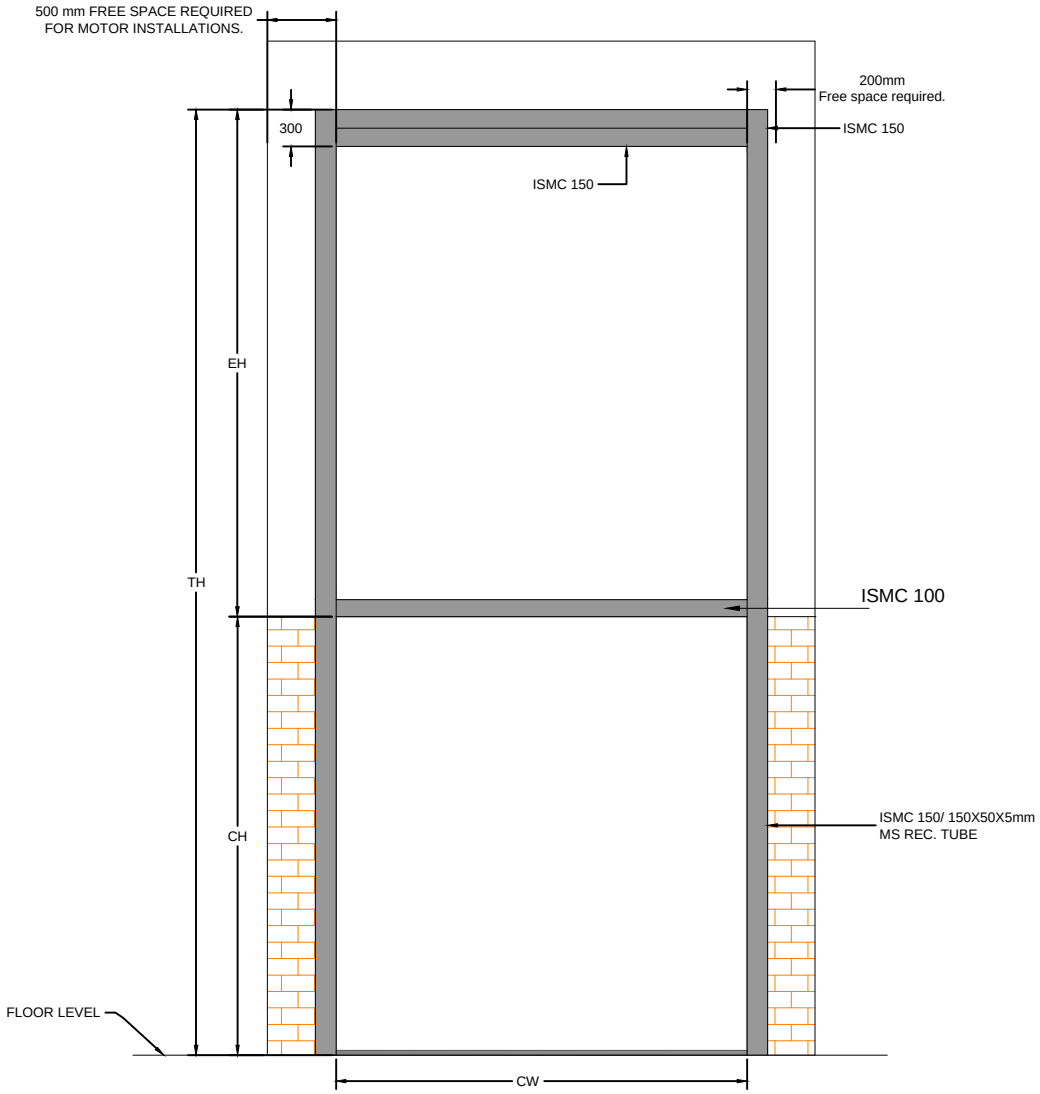

INSIDE ELEVATION

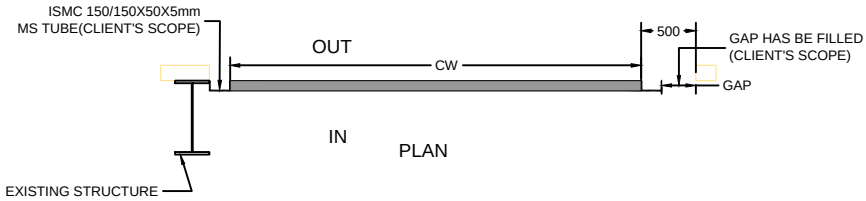

PLAN

NOTE- STRUCTURE FOR SECTIONAL DOOR WILL BE IN CLIENTS SCOPE.

SR NO	CLEAR WIDTH	CLEAR HEIGHT	QTY	TH	EH	LOCATION (w.r.t PDF TPL-3452-X9100-EC-AC-6200_R1)	MOTOR POSITION
1	3350mm	6000mm	1	12300	6300	7-B	RIGHT SIDE

This drawing & design is the property of NIHVA TECHNOLOGIES. Not to be sold or copied to any other concern.

TITLE

STRUCTURE FOR SECTIONAL DOOR

CLIENT APPROVAL

ALL DIMENSION ARE IN mm

NIHVA TECHNOLOGIES PVT. LTD.
NIHVA TECHNOLOGIES PVT. LTD. PUNE
Tel : 020 66304033
Email:- info@nihva.com
Website:- www.nihva.com

	SIGN	DATE	
DRAWN	OMKAR	28/04/17	CLIENT - TATA PROJECTS
CHECK	SAGAR P.	28/04/17	PROJECT - MADHEPURA ELECTRIC LOCOMOTIVE PVT. LTD.
REV.			SITE - MADHEPURA,BIHAR
APPRD.			DWG. NO. - NIHVA/17-18/0044
MFG			SCALE: NTS | WT: | SHEET: 01 OF 01
Ref. No.			If any queries contact : projects@nihva.com

PRODUCED BY AN AUTODESK EDUCATIONAL PRODUCT
PRODUCED BY AN AUTODESK EDUCATIONAL PRODUCT
PRODUCED BY AN AUTODESK EDUCATIONAL PRODUCT