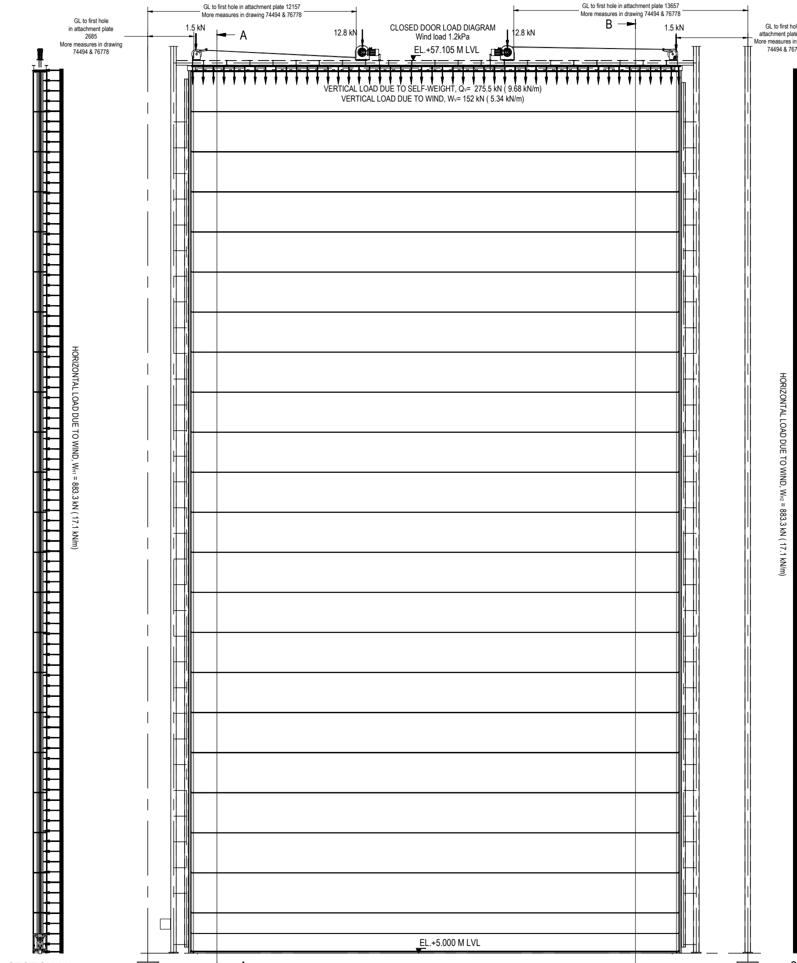
GL to first hole
in attachment plate
2685
More measures in drawing
74494 & 76778
GL to first hole in attachment plate 12157
More measures in drawing 74494 & 76778
GL to first hole in attachment plate 13657
More measures in drawing 74494 & 76778
GL to first hole in
attachment plate 4185
More measures in drawing
74494 & 76778
1.5 kN
A
12.8 kN
CLOSED DOOR LOAD DIAGRAM
Wind load 1.2kPa
EL.+57.105 M LVL
12.8 kN
B
1.5 kN
VERTICAL LOAD DUE TO SELF-WEIGHT, Qv= 275.5 kN (9.68 kN/m)
VERTICAL LOAD DUE TO WIND, Wv= 152 kN (5.34 kN/m)
HORIZONTAL LOAD DUE TO WIND, Wh = 883.3 kN (17.1 kN/m)
HORIZONTAL LOAD DUE TO WIND, Wh = 883.3 kN (17.1 kN/m)
EL.+5.000 M LVL
GRID
A
B
GRID

SECTION A-A

ELEVATION VIEW - WEST SIDE MEGA DOOR ARRANGEMENT
(SCALE 1:100)

SECTION B-B


OPEN DOOR LOAD DIAGRAM
Nominal static vertical loads are indicated. Values within brackets { }
include dynamic surload factor 1.25 for door leaf loads in open position.
134.0 kN
{167.5 kN}
12.8 kN
EL.+57.105 M LVL
12.8 kN
134.0 kN
{167.5 kN}
VERTICAL LOAD DUE TO SELF-WEIGHT, Qv= 10.52 kN (0.37 kN/m)
Working load 127.8 kN
Working load √2 x 127.8 kN
Working load 127.8 kN
EL.+5.000 M LVL
GRID
GRID

ELEVATION VIEW - WEST SIDE MEGA DOOR ARRANGEMENT
(SCALE 1:100)

Revision		Date	By
A	Costumer steel and measures added.	2022-01-14	FV
B	Clear height was 47500.	2022-01-20	FV
C	Clear height was 47264. Right motor adjusted to avoid clash.	2022-02-28	FV
D	Top attachment adjusted.	2022-03-14	FV

NOT INCLUDED IN DOOR SUPPLY:

1. Design and supply of all door supporting structural components.
2. Design and supply of all closure between door and adjacent steel.
3. Design and supply of coverage, such as roofing or enclosure, for door components at door head.
4. Door jambs adjustable for overall door width and true to plumb.
5. Paint job after completed door installation.
6. Any frameworks being provided by ASSA ABLOY will be clearly indicated as "by ASSA ABLOY".

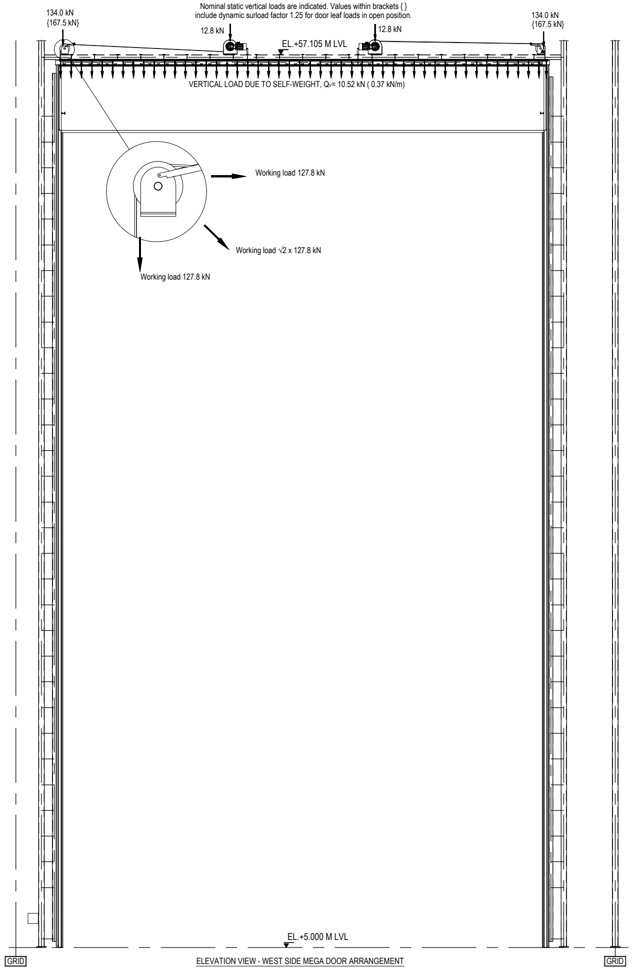REQUIREMENTS ON BUILDING:

7. Door head support must be straight within 1/600 of span in the in/out direction and free from protrusions of any kind.
8. For a single door leaf, door head support should be horizontal and straight within 1/600 of span at distributed full door load.
9. Door side jambs must be smooth, straight and parallel, out of plumb must not exceed 2mm/m (total deviation at full length 5 mm) in any direction.
10. Any footings at bottom of jamb columns must not interfere with installation of guide rails at floor level.
11. At time of installation, finished floor, free from obstructions, out to a distance of 2 m on each side of door centreline must be available.
12. Bracket/attachment plate for hoist should be flat within 5mm/m.

DOOR PROPERTIES:

13. The door is designed to withstand a differential pressure of 1.2kPa.
14. Guide rails, top- and intermediate beams in extruded aluminium with natural finish.
15. Environmental category: C5 according to ISO 12944-2
16. Bottom beam in carbon steel painted: Light grey (RAL7047)
17. Colored clamp strips on both sides: Grey
18. The door fabric is a UV stabilized, flame retardant, self-extinguishing, PVC coated polyester fabric with fire technical properties Euroclass B-s2, d0 (according to EN 13501-1:2007).
19. Colour of fabric: GREY (NCS 3500, RAL 7004)

ELECTRICAL:

20. One main control panel provided of PLC type.
21. Control mode : Impulse up / Constant contact down.
22. Cables are included.
23. Back-up power socket & switch.
24. Audible & visual alarm.
25. Wind-lock indication.
26. Approx. size of main control panel: WxHxD (600x600x210 mm),
27. Location of main control panel: Please specify location.
28. Aux. Voltage 24VDC
29. Power supply: 415V /3Ph /50Hz
30. Power: 50.4kW
31. Nom. current: 94A
32. Start. current: 624A
33. (max. allowed voltage drop at start: 5%)

DOOR IDENTITY NUMBER: 84704001-004

INTERFACE, ref. to drwng. no. 74494

DESIGNED
FV
SIZE
A1F
SCALE
1:100
CODE
84704
ITEM NO
DATE
2021-11-03

If not otherwise stated:
Tolerances
ISO 2768-m
EN ISO 13920-B
Cutting class
ISO 9013-442
Weld class
ISO 5817-C
Surface finish
Smooth raw surface

ASSA ABLOY

Seabird Karwar
India
Megadoor 28000 x 47500
Load diagram & Notes

DRAWING NO
74495
REVISION
D
PLOT DATE

This document is the property of ASSA ABLOY Entrance Systems AB and shall not without our written permission be copied, imparted to a third party or used for any other unauthorized purpose.