


INSIDE

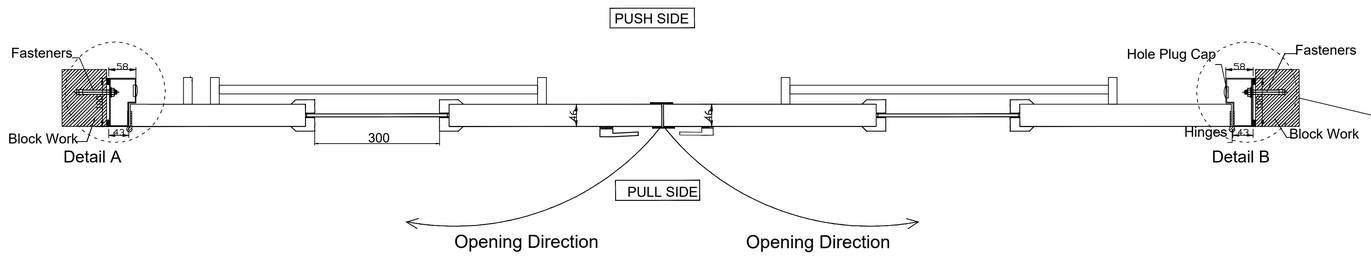


SECTION 'X'-'X'

OUT SIDE

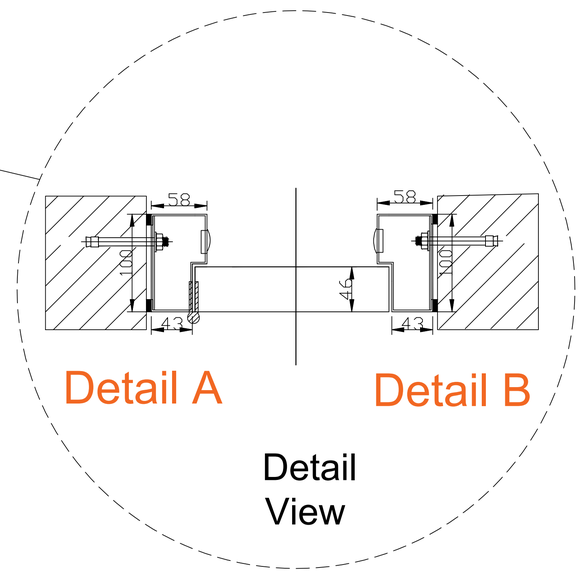

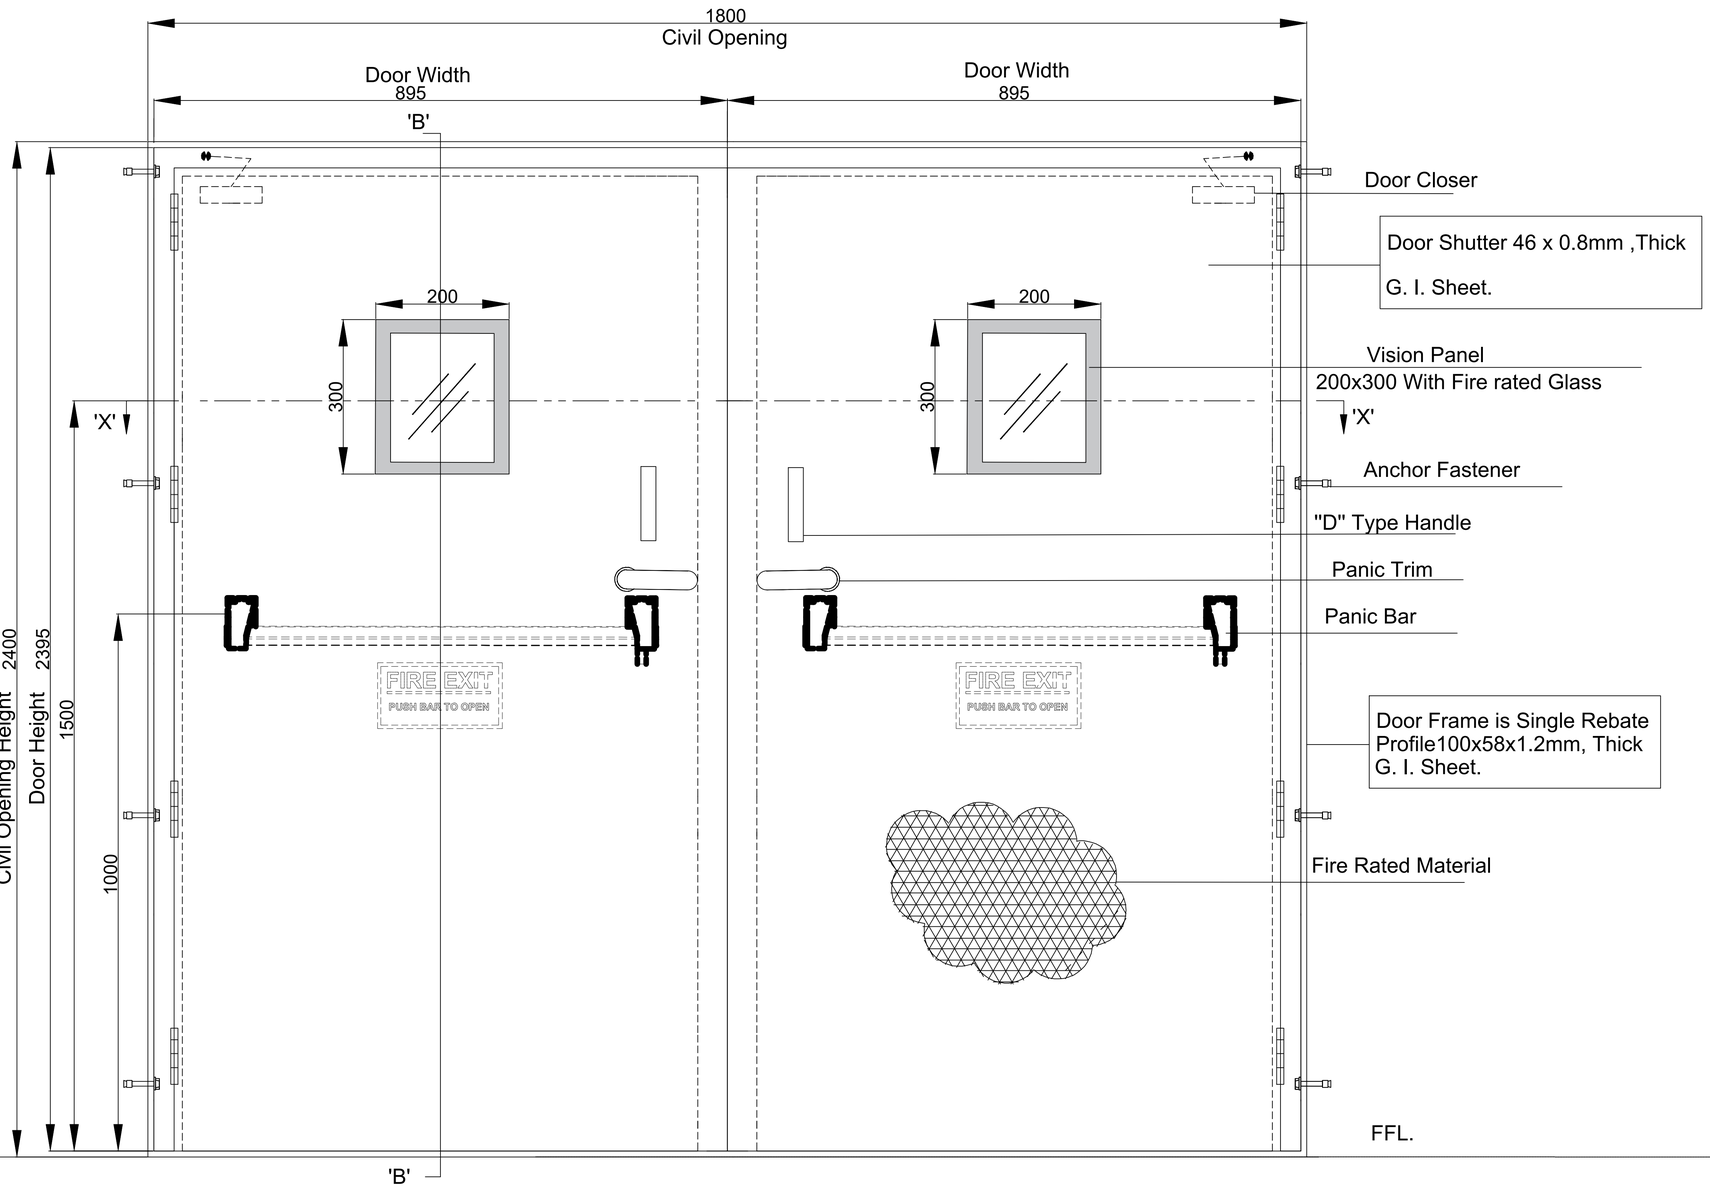

ELEVATION

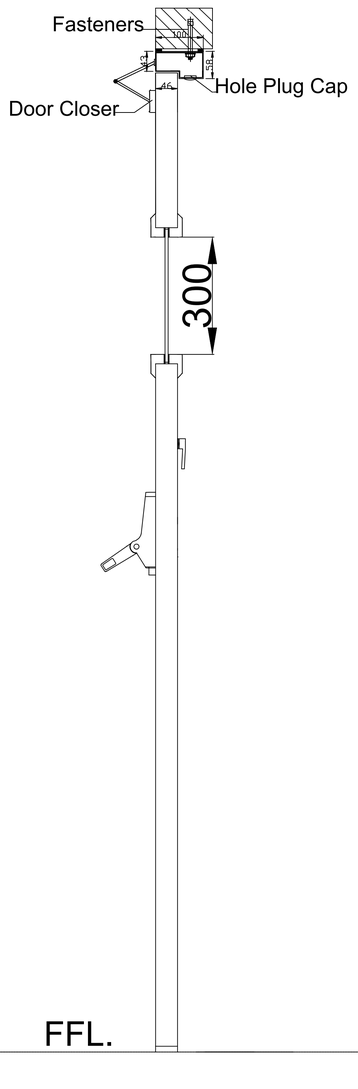

SECTION B-B

FRONT VIEW

TECHNICAL SPECIFICATION :

Sr.	DESCRIPTION & DETAILS
01	Door frame - 100X58 mm x1.2mm thick G.I. Sheet
02	Door Shutter - 46 mm x0.8mm thick G.I. Sheet
03	SS Ball Bearing Hinges 4"x3"x3mm
04	Single Leaf Panic Bar (1 Point) With silverfinish ASSA ABLOY Make
05	External " D " Type Handle With silverfinish ASSA ABLOY Make
06	Anchor Fasteners CSK Type With GI Plating Size : 8mmx80mm With PVC Sleve
07	Door Closer With Standard arm silverfinish ASSA ABLOY Make
08	Vision Window 200x300 With fire Rated Glass
09	Fire Rating - 120 Minutes
10	Surface Finish - As per Client Requirement

SIZE:

Sr.	Clear Width	Clear Height	Qty
01	1800	2400	01

This Drawing & Design is the property of NIHVA TECHNOLOGIES. Not to be sold or copied to any other concern.

TITLE :- FIRE DOOR

NAME	DATE	SIGN
S.J	16/05/2024	
A.K	16/05/2024	
V.T	16/05/2024	

If any queries contact : design1@nihva.com

All dimensions are in MM

NIHVA TECHNOLOGIES PVT. LTD.
NIHVA TECHNOLOGIES PVT. LTD. PUNE
Tel : 020 66304033
Email:- info@nihva.com
Website:- www.nihva.com

LOCATION -

PRODUCT - FIRE DOOR | QTY-01 No's

DWG NO - NIHVA/23-24/00XX | REV- 01

SCALE : NTS | SHEET : 01 OF 01