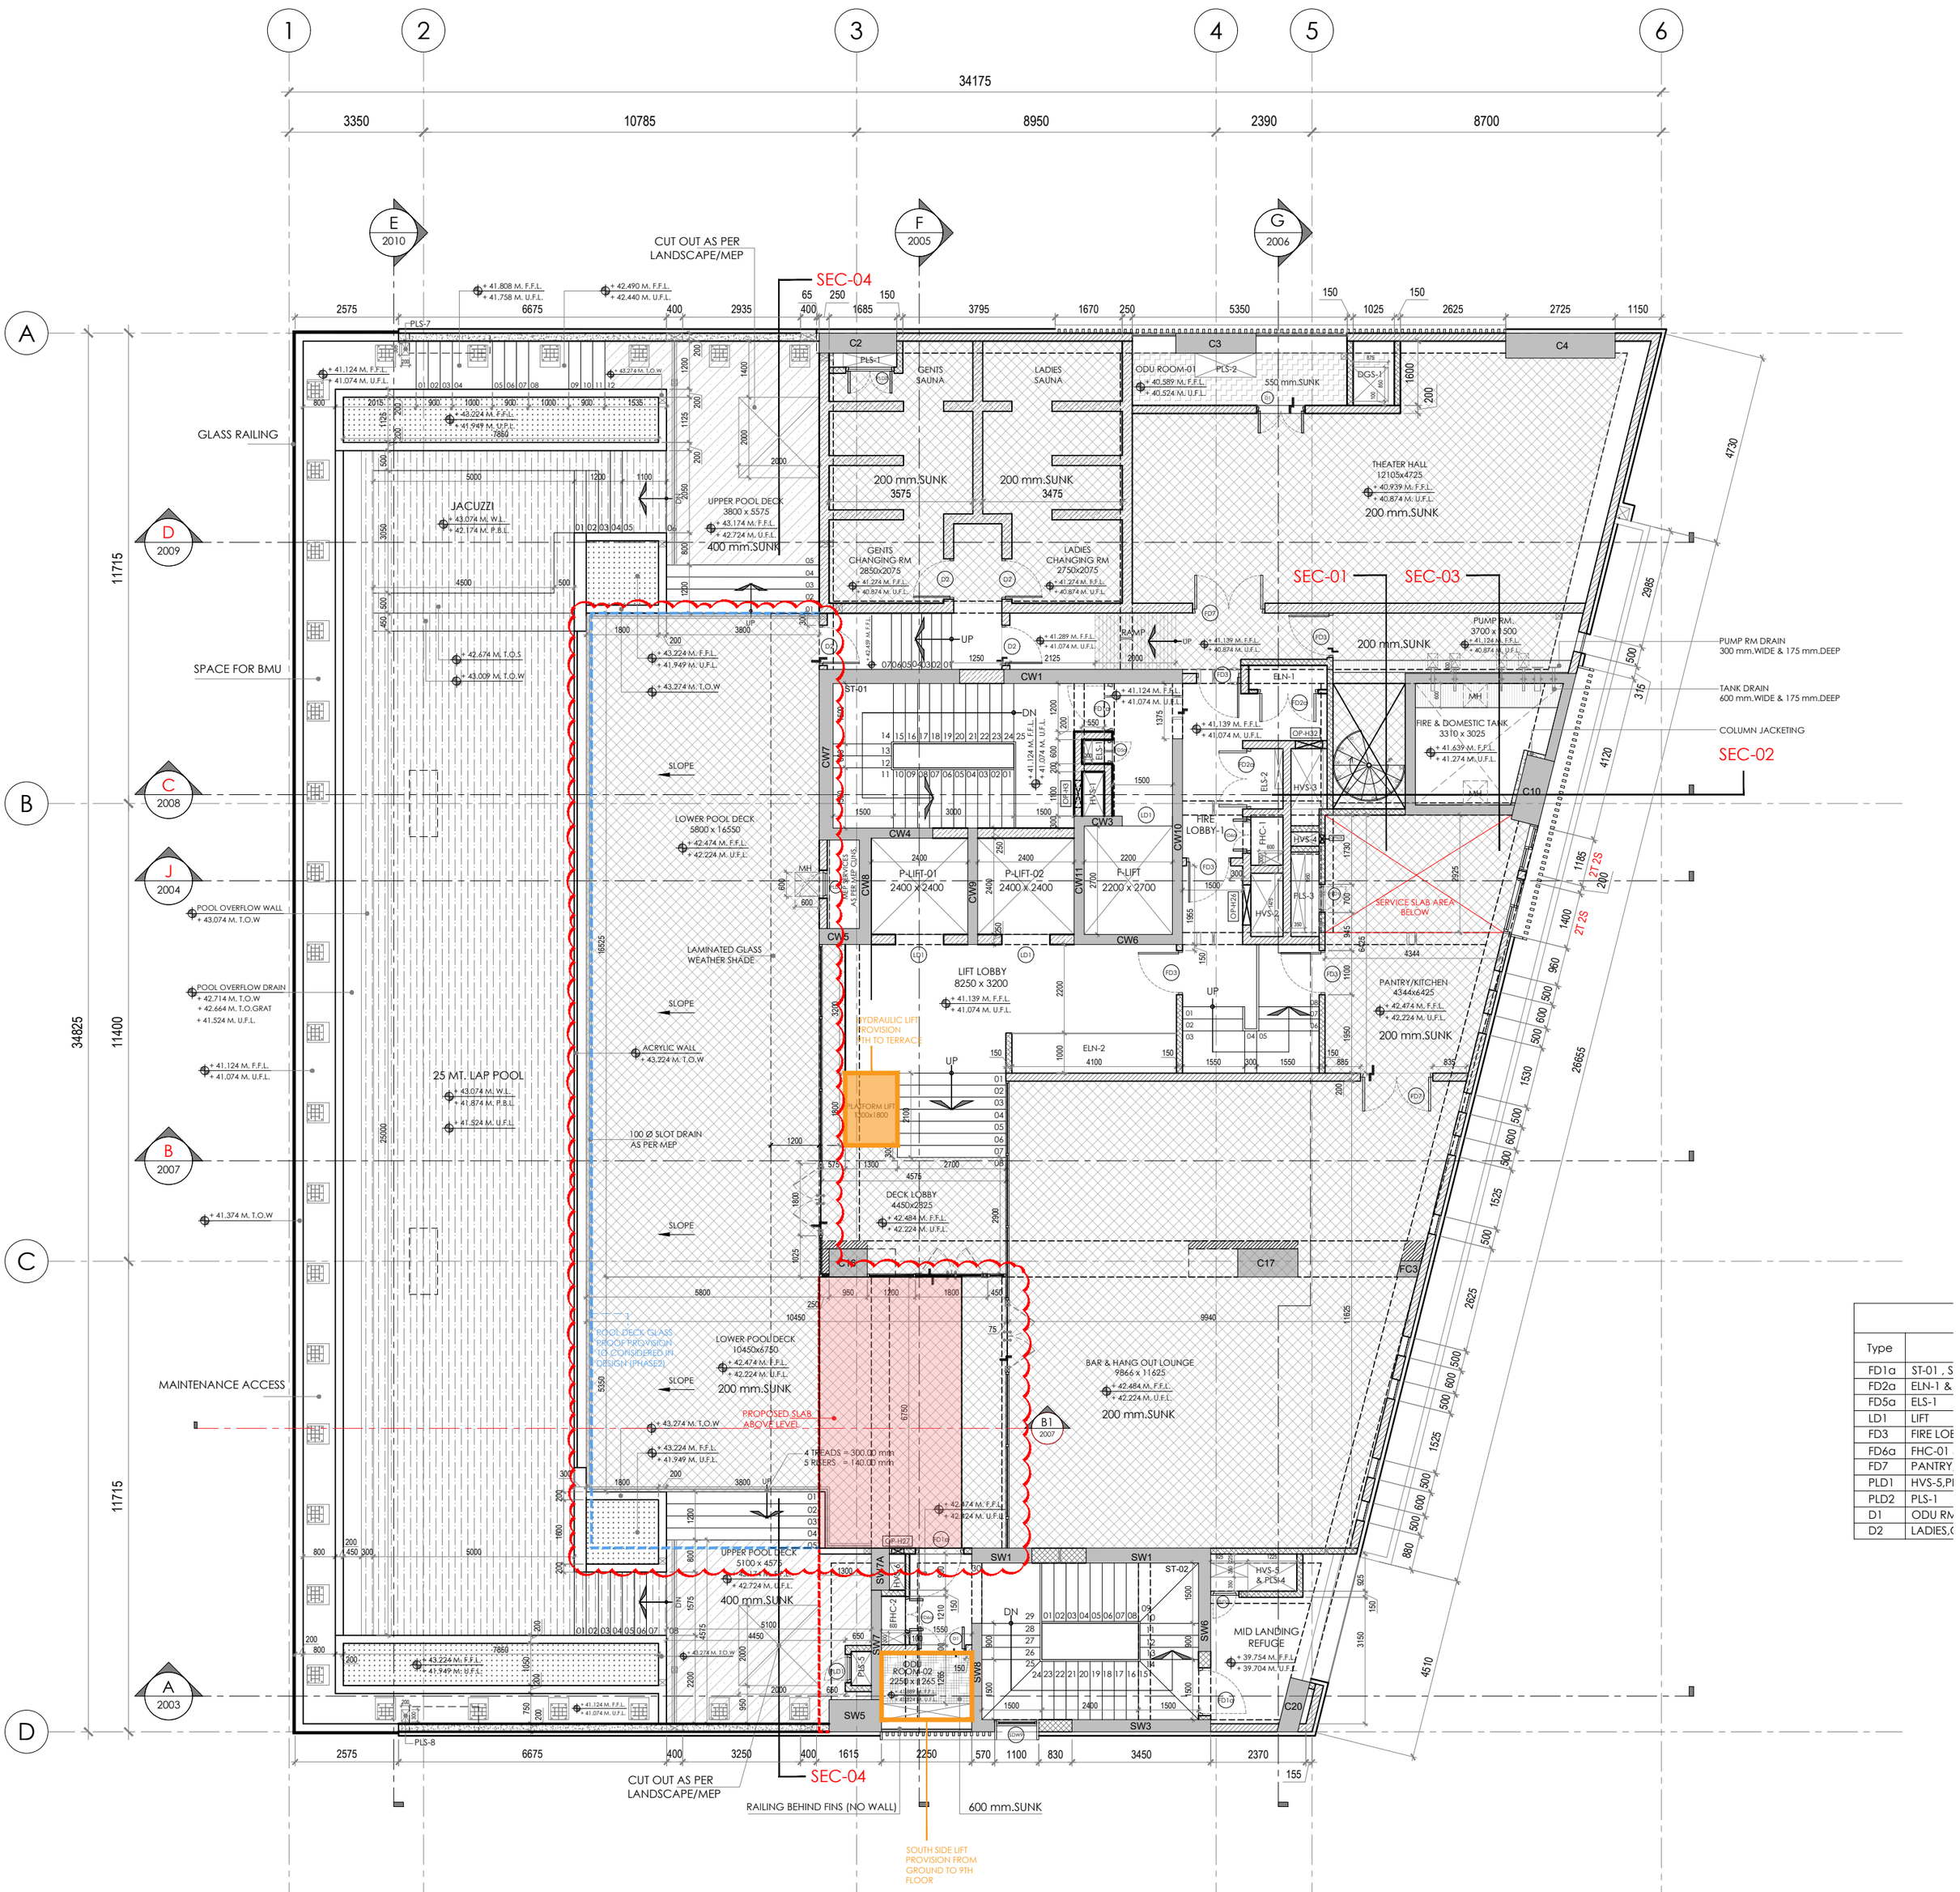


Type	
FD1a	ST-01 , S
FD2a	ELN-1 &
FD5a	ELS-1
LD1	LIFT
FD3	FIRE LOE
FD6a	FHC-01
FD7	PANTRY
PLD1	HVS-5,PI
PLD2	PLS-1
D1	ODU RM
D2	LADIES,C

9TH FLOOR PLAN

1 / 1015

SCALE 1:100