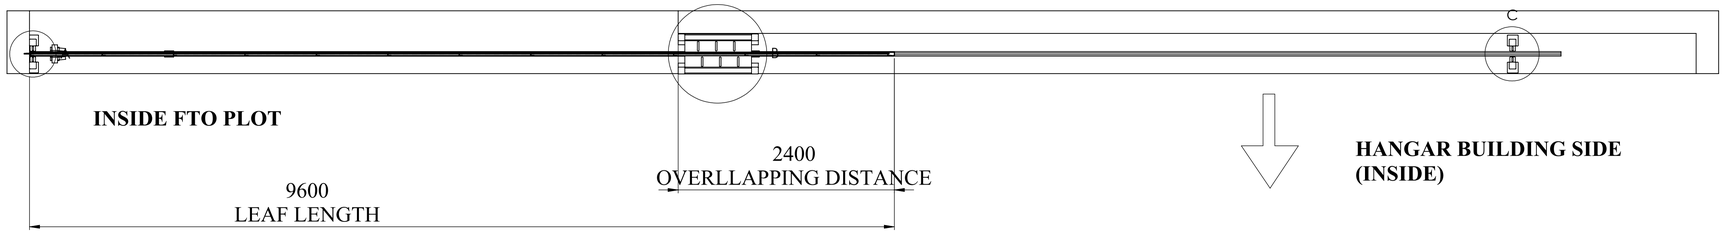
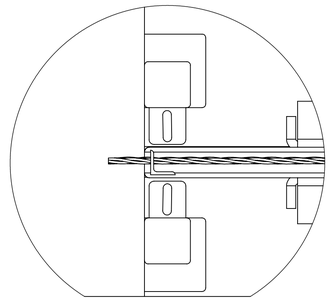
OUTSIDE FTO PLOT
(MADC LAND)

SLIDING DIRECTION

LAND SIDE (OUTSIDE)

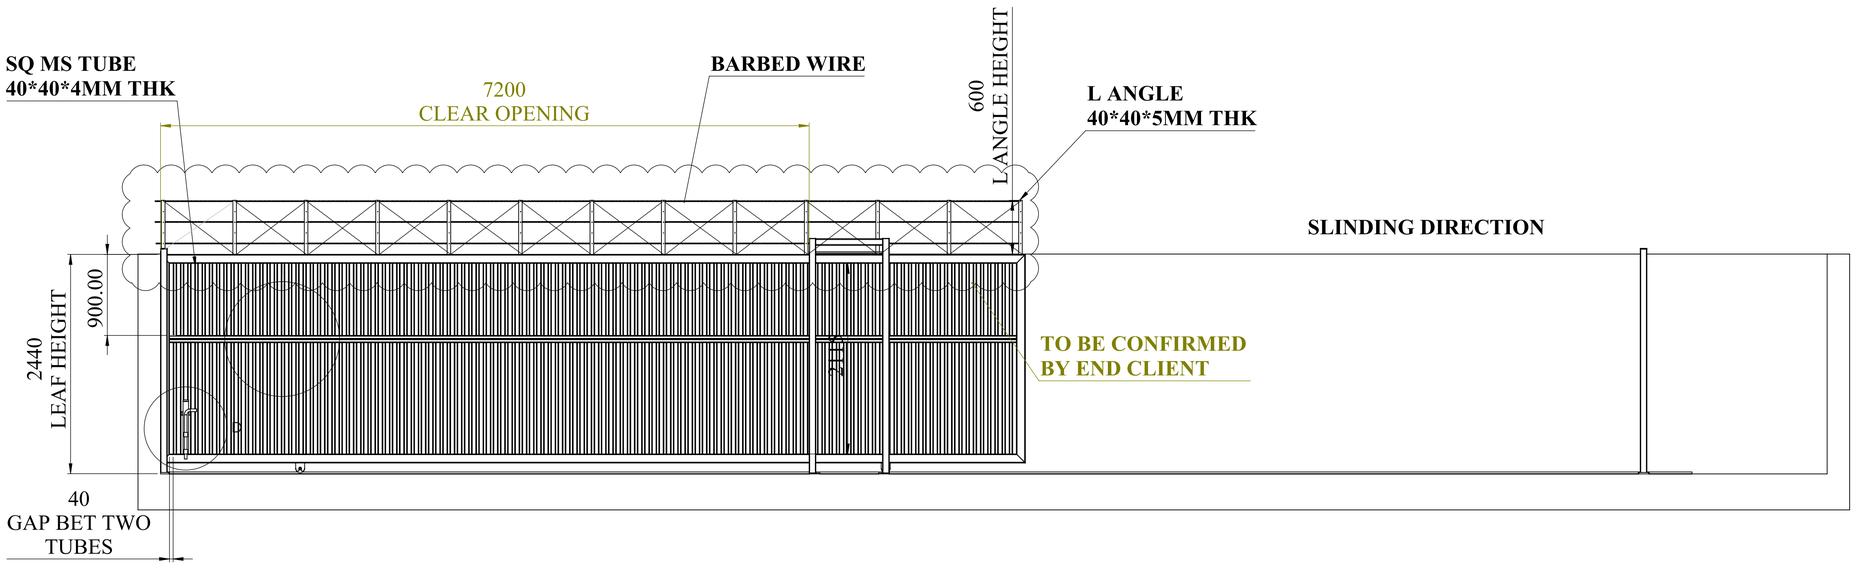


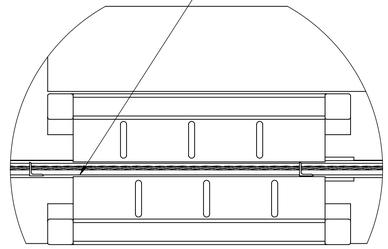

HANGAR BUILDING SIDE
(INSIDE)



POST 1 & NYLON
ROLLER ASM

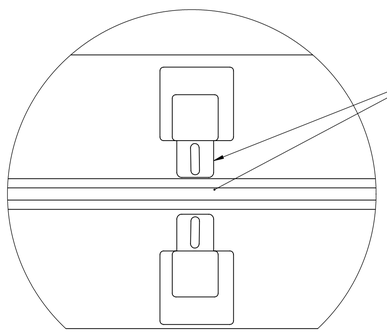
DETAIL A
SCALE 1 : 5



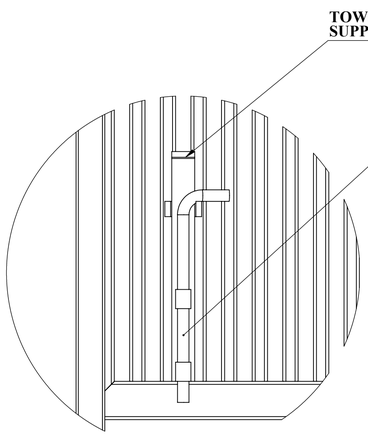

POST 2 & NYLON
ROLLER ASM

DETAIL B
SCALE 1 : 9



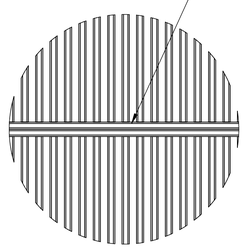

POST 3 & NYLON
ROLLER ASM

DETAIL C
SCALE 1 : 5




TOWER BOLT LOCKING
ARRANGEMENT

DETAIL D
SCALE 1 : 8




DETAIL I
SCALE 1 : 17

**NOTE :**

**1)GA DRAWING SINGLE SLIDING GATE TYPE NO 05.**
**2)03 column posts when the gates is in the closed position.**
**3)03 column posts when the gates is in the fully open position.**
**4) barbed wire design is zigzag pattern.**

| | | | | | |
|---|---|---|---|---|---|
| UNLESS OTHERWISE SPECIFIED: DIMENSIONS ARE IN MILLIMETERS SURFACE FINISH: TOLERANCES: LINEAR: ANGULAR: | FINISH: | | DEBURR AND BREAK SHARP EDGES | DO NOT SCALE DRAWING | REVISION |
| | NAME | SIGNATURE | DATE | TITLE: | |
| DRAWN | | | | | |
| CHK'D | | | | | |
| APPV'D | | | | | |
| MFG | | | | | |
| Q.A | | | | | |
| MATERIAL: | | | | DWG NO. | |
| WEIGHT: | | | | SCALE:1:100 | SHEET 1 OF 1 |

GA DRAWING TYPE 05