


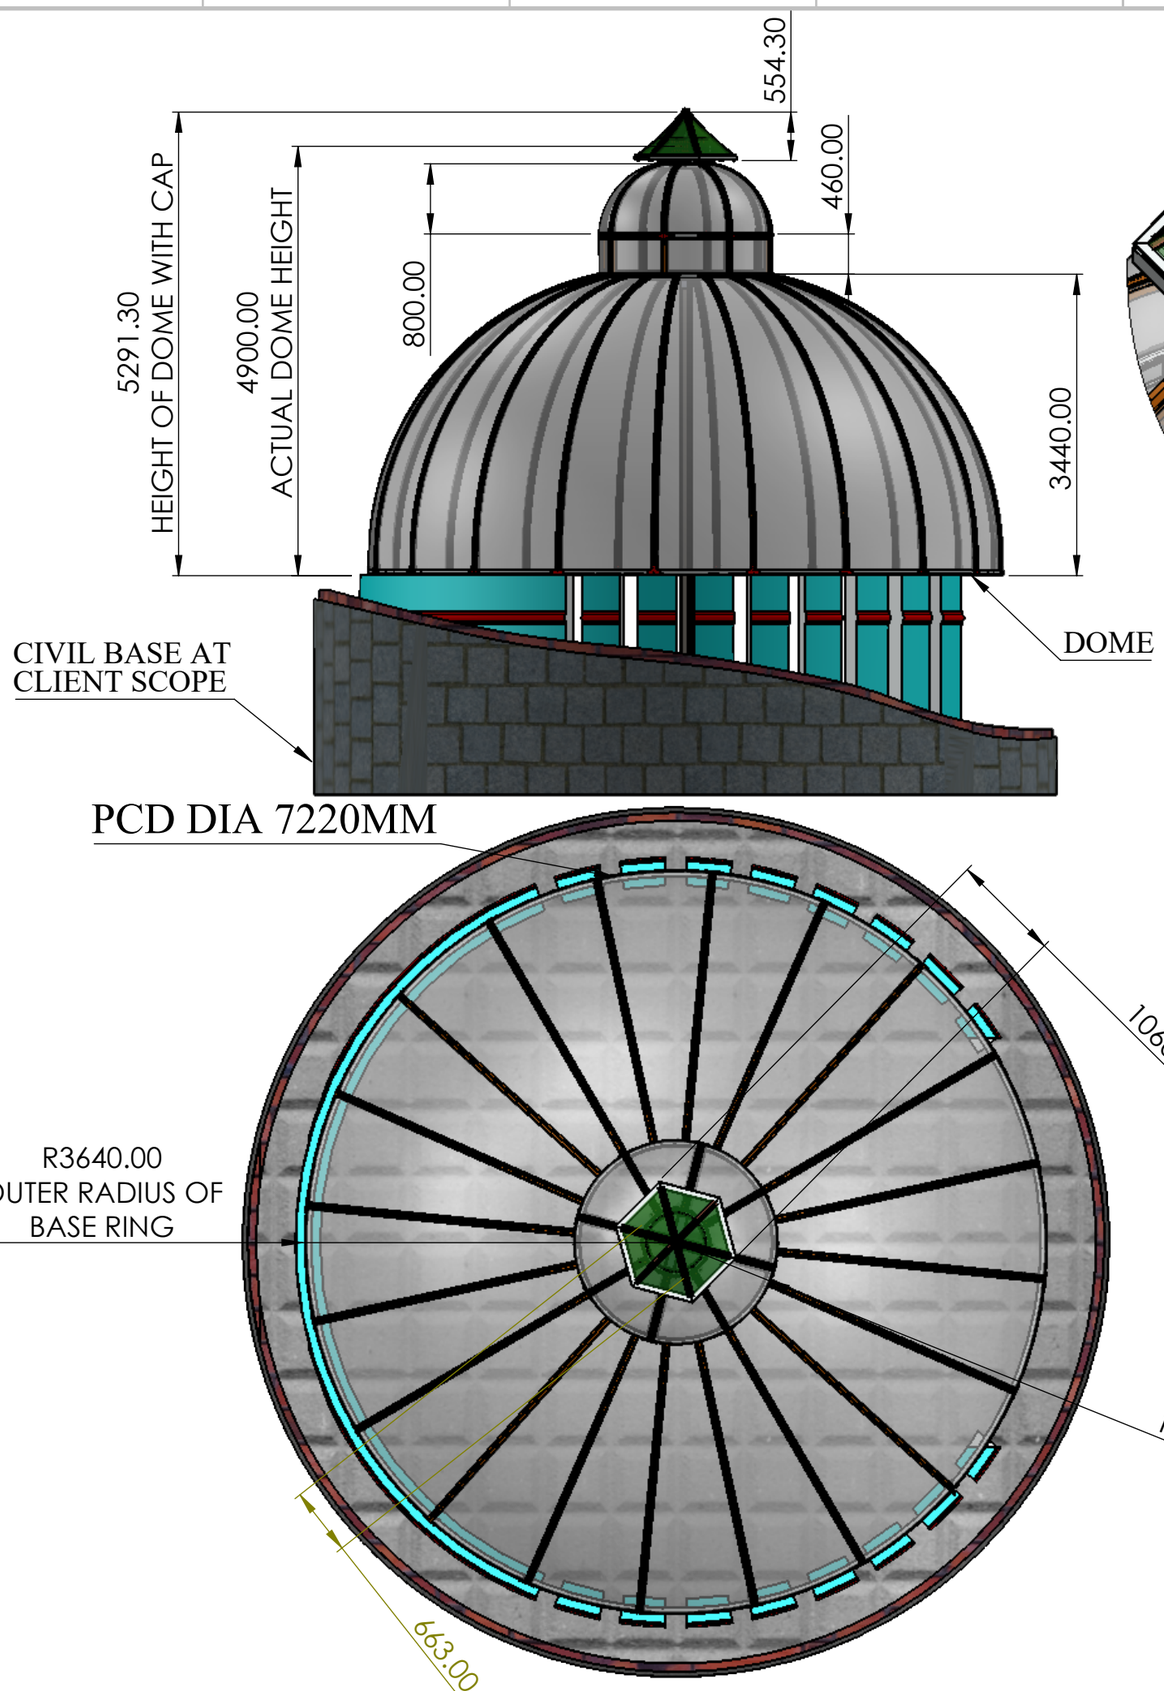


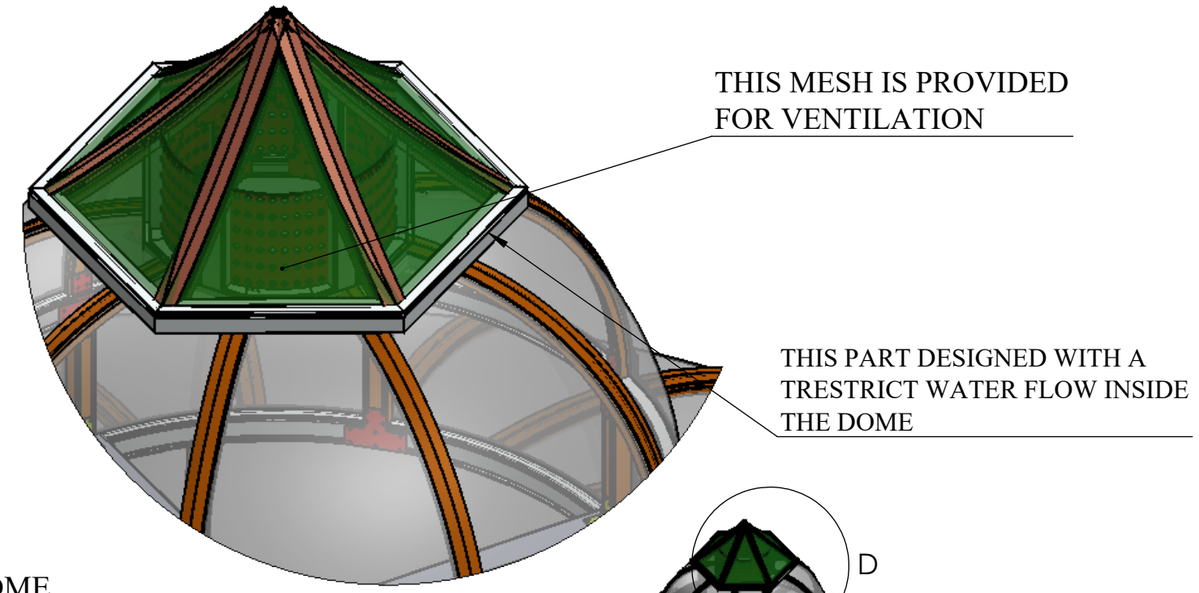


DETAIL D
SCALE 1 : 15

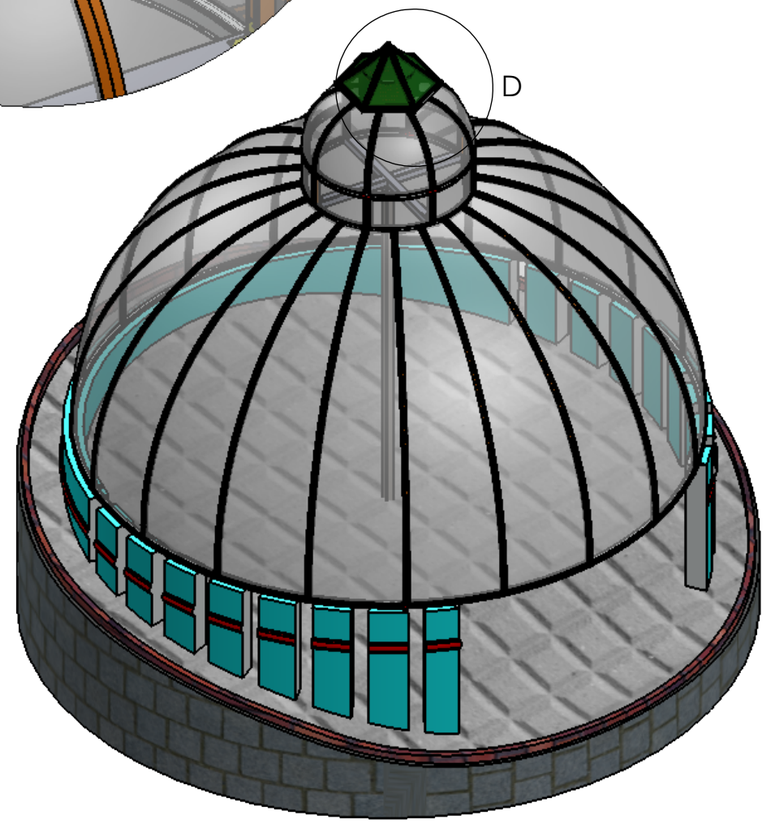


TITLE - RETRACTABLE ROOF				NIHVA TECHNOLOGIES PVT.LTD.PUNE
DWG NO - NTPL-277-PM-001-00-00-00				Website - www.nihva.com
	NAME	SIGNATURE	DATE	PROJECT NO - NTPL-277-PM
DRAWN	V.W		23-04-2025	PRODUCT - RETRACTABLE ROOF
CHK'D	S.W.		25-04-2025	SITE LOCATION - LONAVLA
APPV'D	V.T.		25-04-2025	
if any queries contact - supportautomation@nihva.com				REVISION - 01 / QTY - 1
ALL DIMENSION ARE IN mm			A3	SCALE / SHEET 1 OF 2

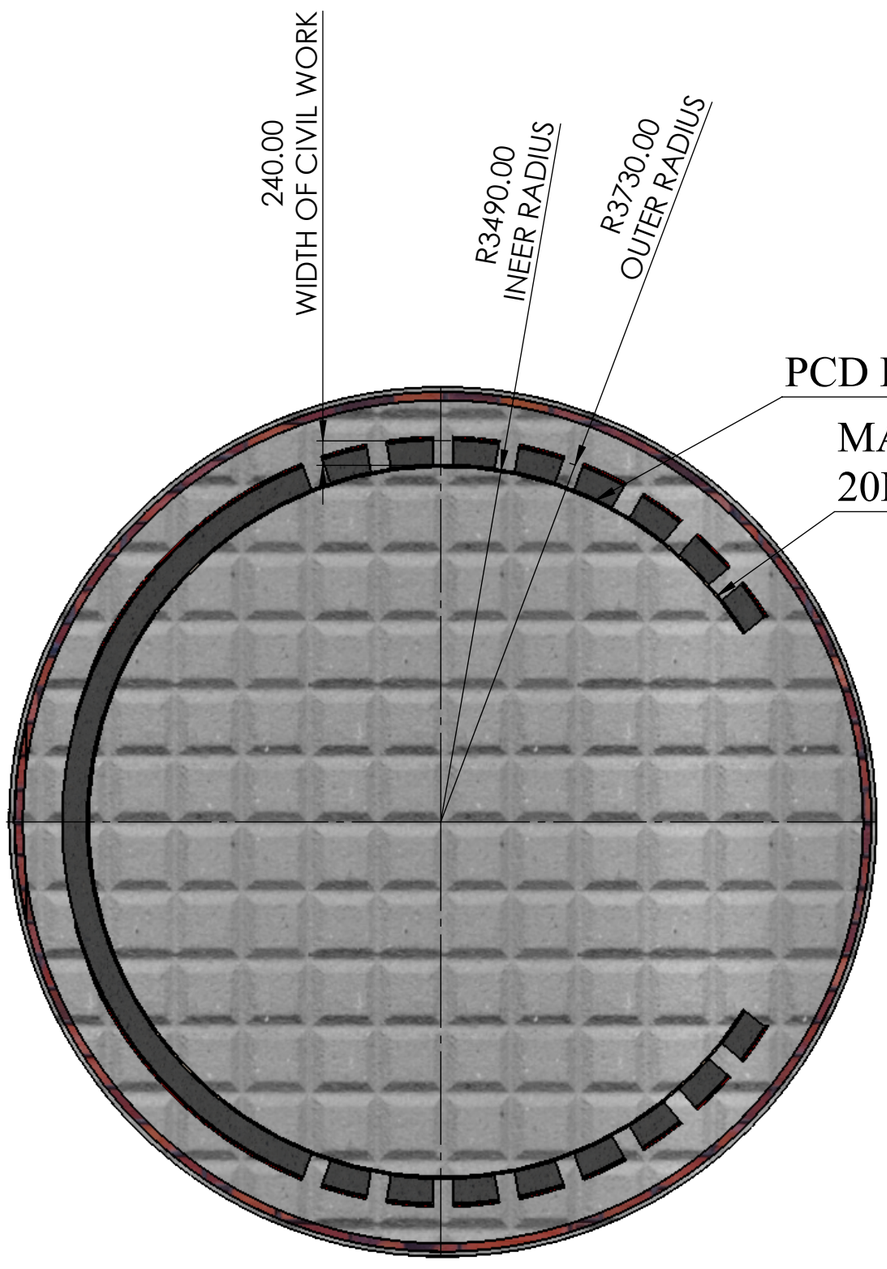

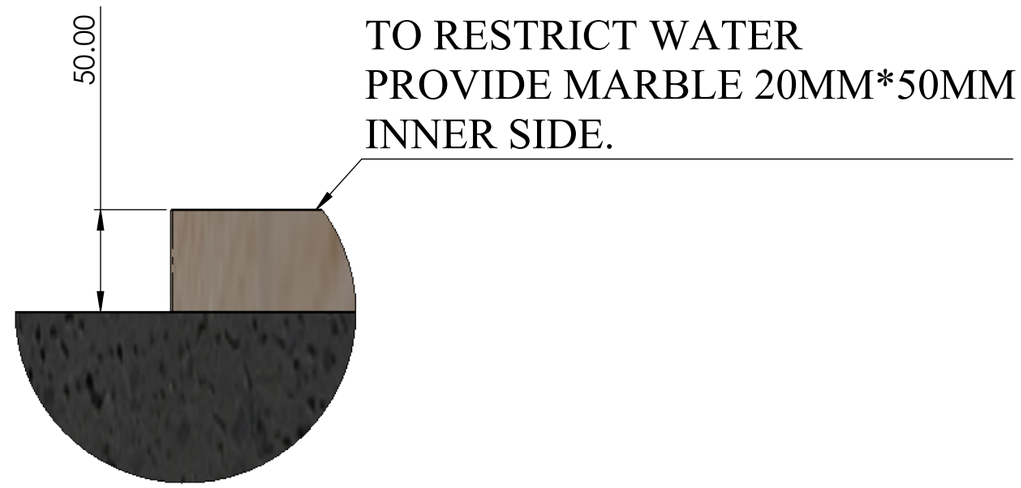

DETAIL A
SCALE 1 : 3

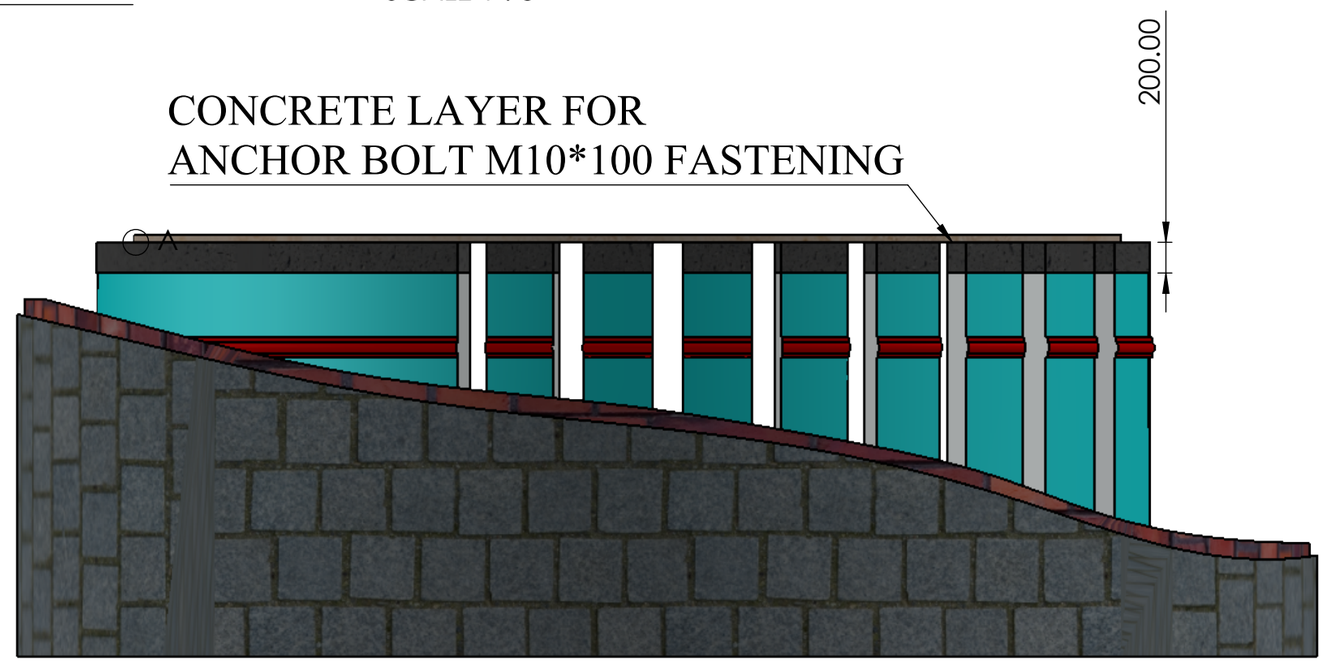

CIVIL DRAWING

NOTE
THERE IS AN OPEN GAP IN THE WALL CONSTRUCTION THAT NEEDS TO BE CLOSED TO PREVENT WATER FLOW INSIDE THE DOME.
TO RESTRICT WATER FLOW INSIDE DOME YOU SHOULD BE CLOSE / FILL THE GAP .

TITLE - RETRACTABLE ROOF				NIHVA TECHNOLOGIES PVT.LTD.PUNE
DWG NO - NTPL-277-PM-001-00-00-00				Website - www.nihva.com
	NAME	SIGNATURE	DATE	PROJECT NO - NTPL-000-PM
DRAWN	V.W		23-04-2025	PRODUCT - RETRACTABLE ROOF
CHK'D	S.W.		25-04-2025	SITE LOCATION - LONAVLA
APPV'D	V.T.		25-04-2025	
if any queries contact - supportautomation@nihva.com				REVISION - 01 / QTY - 1
ALL DIMENSION ARE IN mm		A3		SCALE / SHEET 2 OF 2