




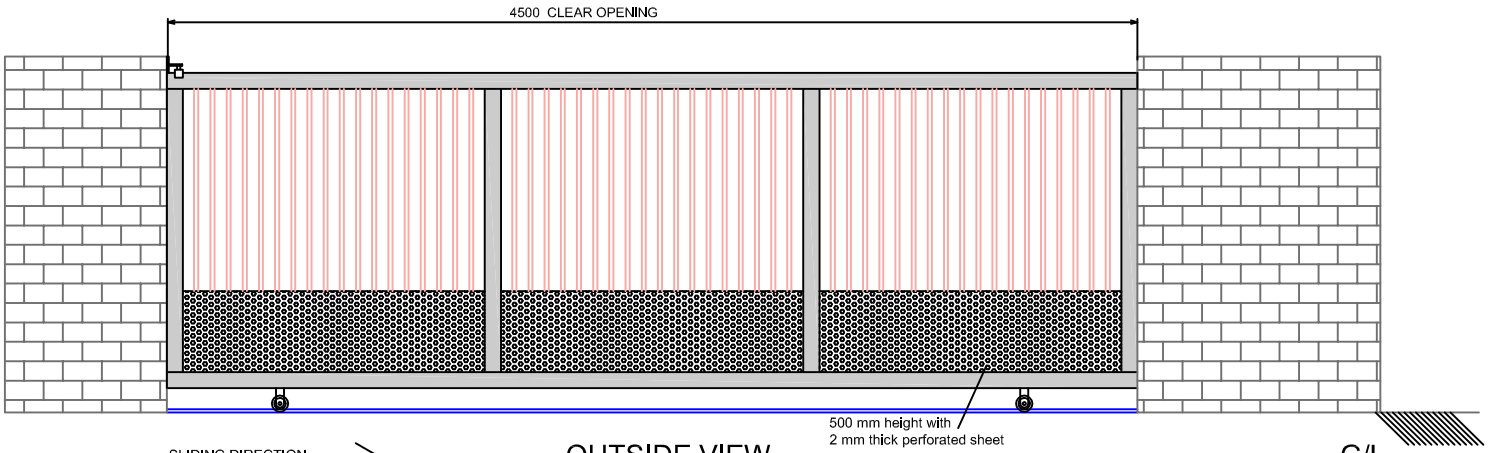

Section A-A

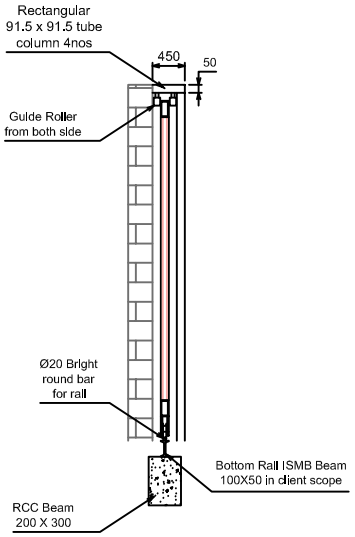

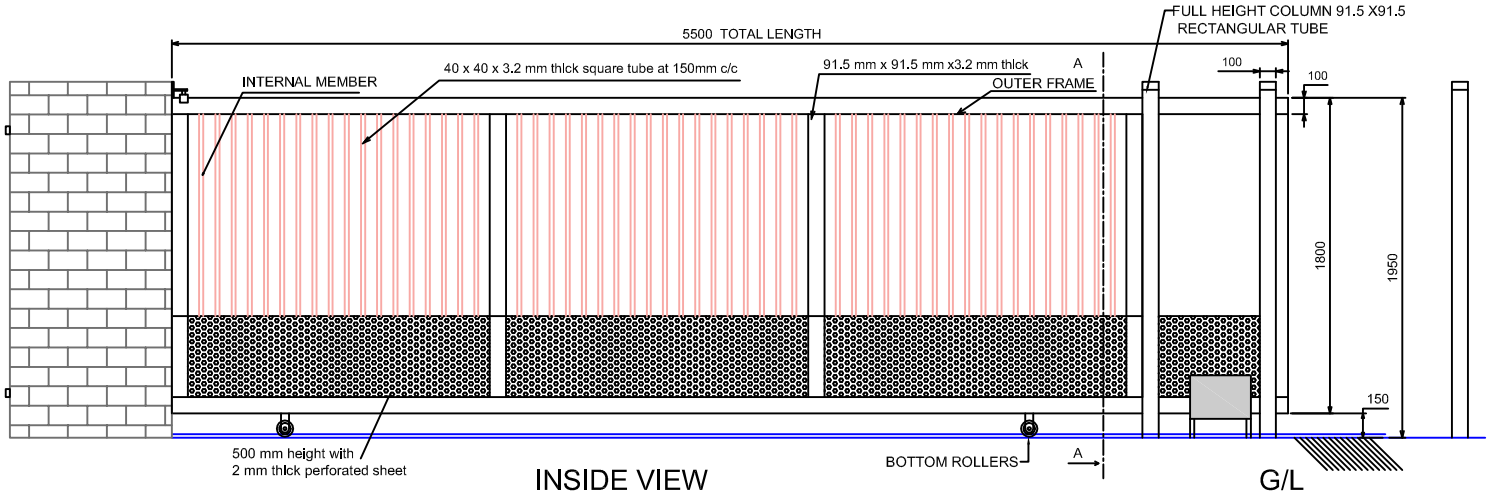

Sliding gate size - 4500X1800mm(Clear opening)
Total length of gate - 5500 1800mm
No. Of Column - 4 nos.
Factory paint finish - Red oxide primer coat
NOTE :- Supply of 'c' channel for vertical support of wicket gate in NIHVA scope
Excavation and civil work for grouting of 'c' channel & I beam will be in client scope.

Drawn By:-A.K	Checked By	Approved By - Date		Date 08-09-14	Scale NTS
NIHVA TECHNOLOGIES PVT. LTD.			CLIENT — PMP Drive system Pvt Ltd.		
			DRG. No. NVA/PMP/07/14-15	Revision 00	Sheet 1-1