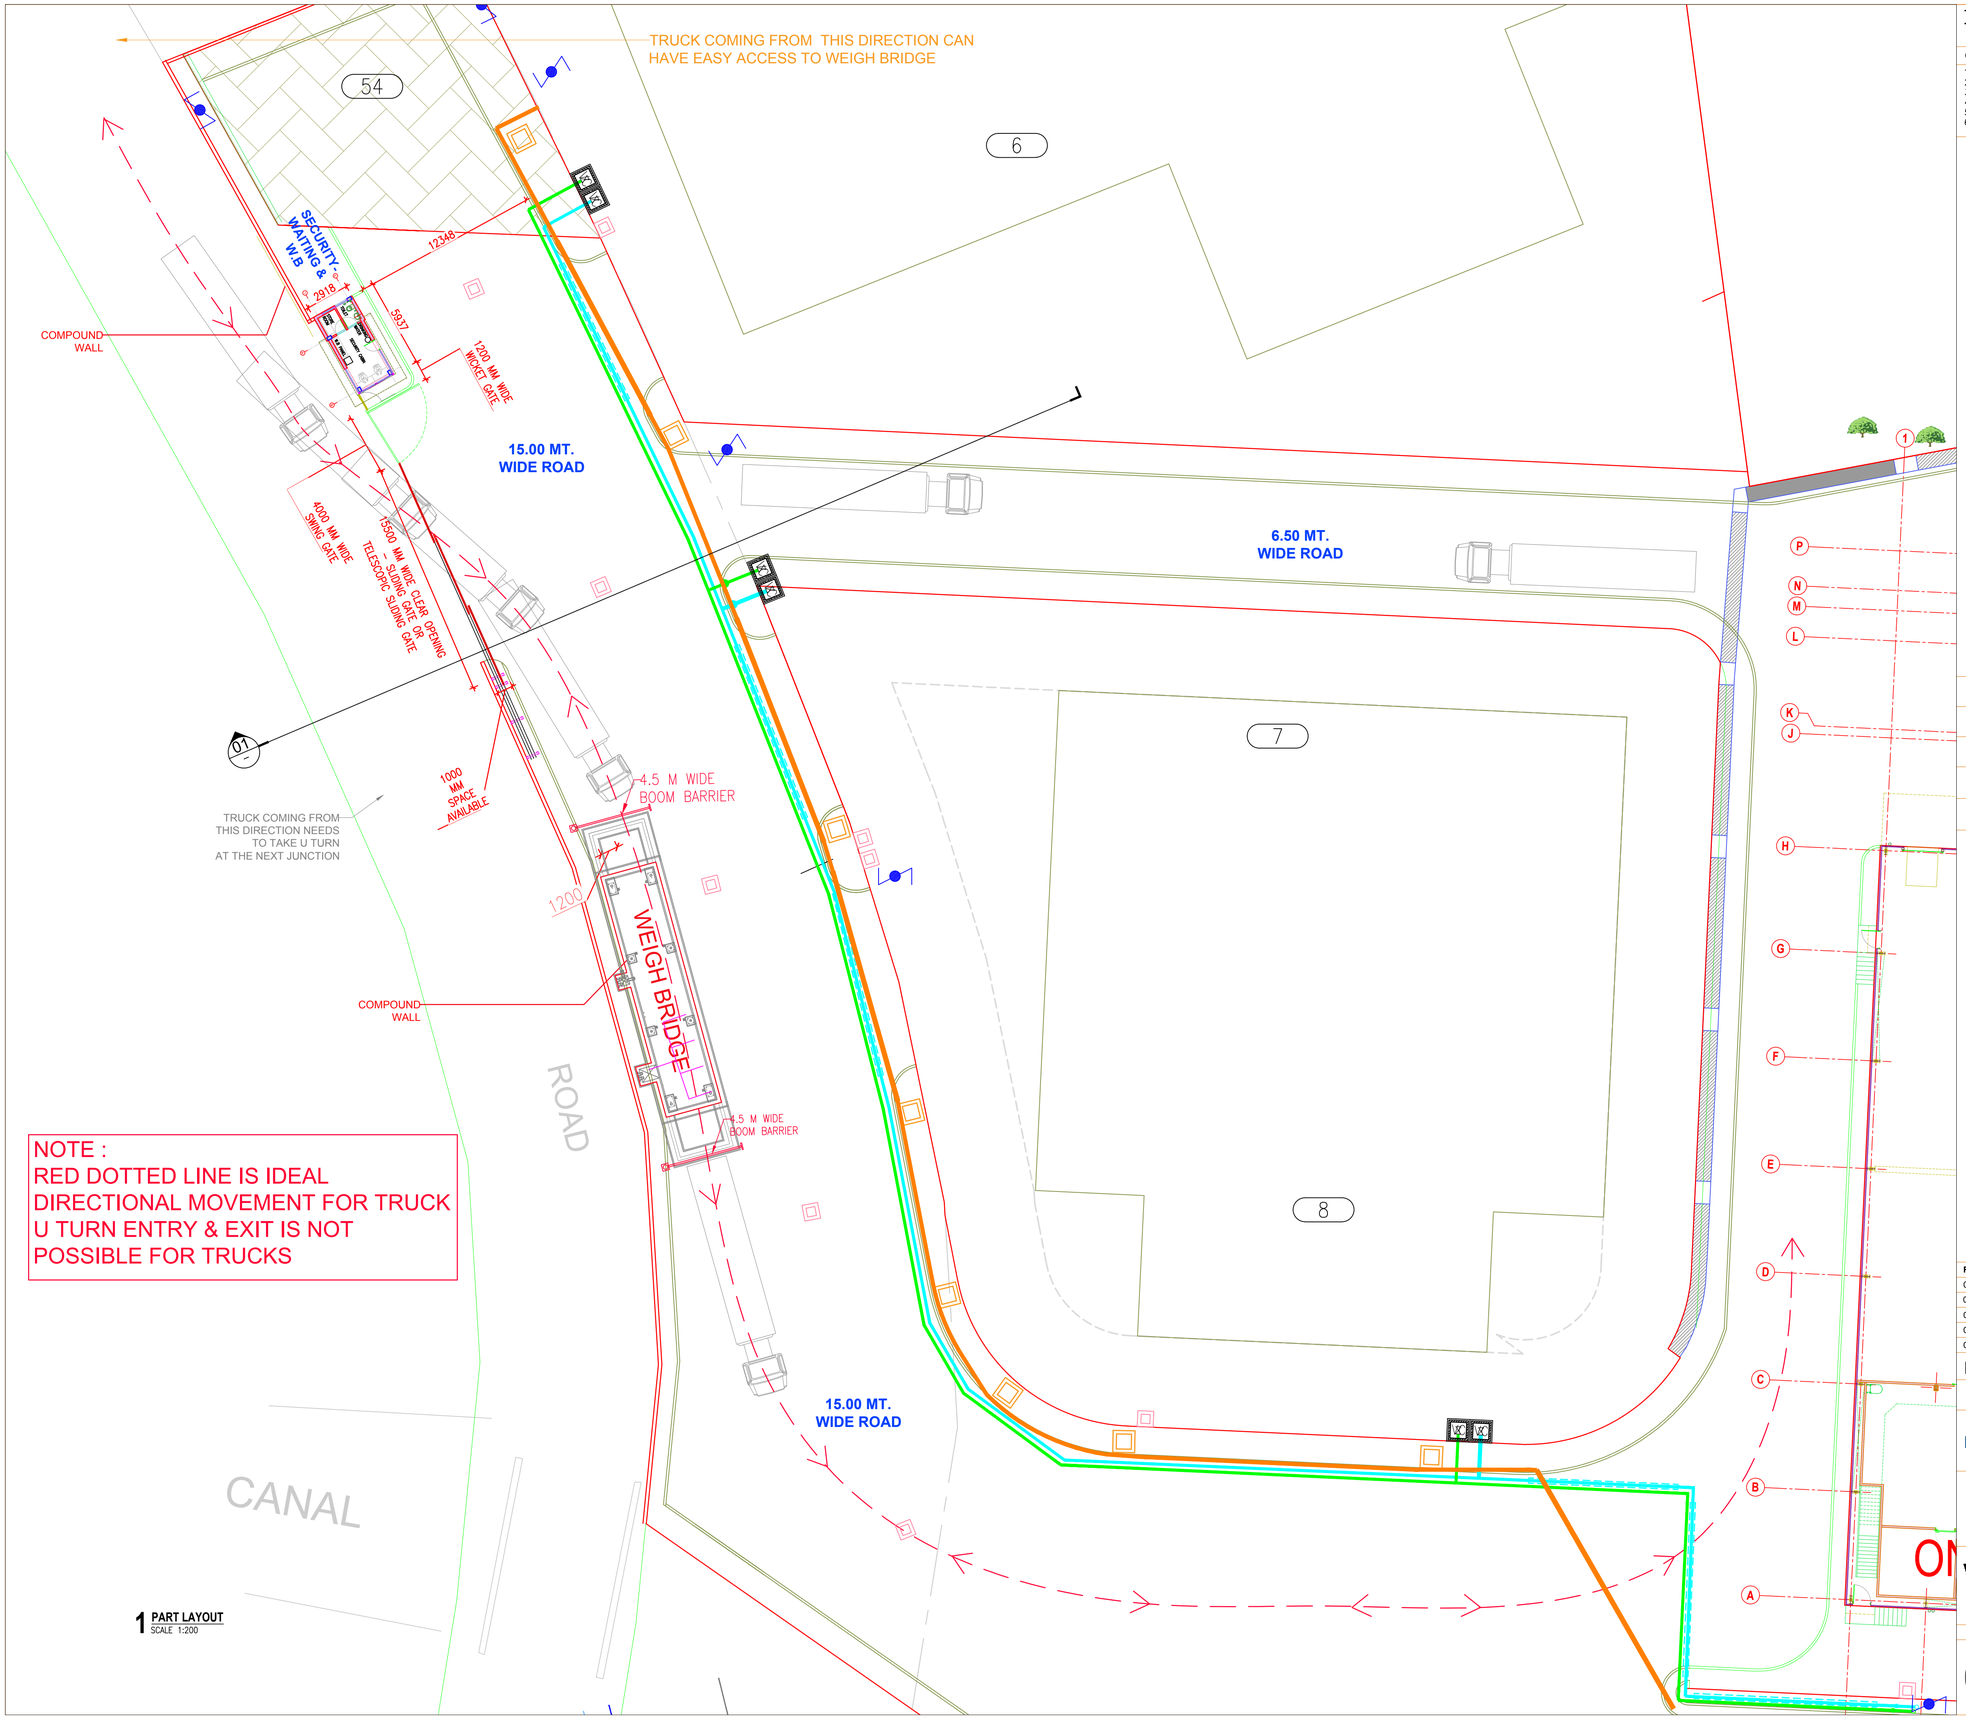


NOTE :
RED DOTTED LINE IS IDEAL DIRECTIONAL MOVEMENT FOR TRUCK U TURN ENTRY & EXIT IS NOT POSSIBLE FOR TRUCKS

1 PART LAYOUT
SCALE 1:200

THIS DRAWING & DESIGN IS THE SOLE PROPERTY OF VMS & SHALL NOT BE COPIED, TRACED OR REPRODUCED BY ANY MEANS WITHOUT PRIOR WRITTEN CONSENT OF THE FIRM.

GENERAL NOTES :

1. ALL THE DIMENSIONS ARE UNFINISHED DIMENSIONS.
2. ALL DIMENSIONS ARE IN MM AND LEVELS ARE IN METERS UNLESS OTHERWISE MENTIONED.
3. ALL CO-ORDINATES ARE IN METER.
4. ALL THE DIMENSIONS SHALL BE READ & NOT TO BE MEASURED.
5. IN CASE OF ANY DISCREPANCY, BRING IT TO THE NOTICE OF THE ARCHITECT IMMEDIATELY.
6. DETAIL DRAWING PRECEDES THE GENERAL DRAWING.

FOR APPROVAL

NO.	DATE	DESCRIPTION	DRAWN BY	CHECKED BY
R2	17-12-20	GENERALLY REVISED	V.M.CHAUHAN	D.DOSHI
R1	15-10-20	GENERALLY REVISED	V.M.CHAUHAN	V.M.C

REVISION HISTORY

REFERENCE DRAWINGS :

01. ARCHITECTURAL :	-
02. STRUCTURAL :	-
03. HVAC :	-
04. ELECTRICAL :	-
05. UTILITIES :	-

MASTER LAYOUT

fanidhar® MEGA FOOD PARK – AT MUDARDA, MEHSANA
khet se bazaar tak...

PROJECT NO.	SCALE :	DRAWN :	V.M.CHAUHAN
2017	1:1500	CHECKED:	V.M.CHAUHAN
	DATE : 14-08-2018	APPROVED:	KINJAL
		COORDINATION CHECKED:	KINJAL

VMS ENGINEERING & DESIGN SERVICES (P) LTD.
CHITRAKOOT FLATS, BEHIND TIMES OF INDIA, OFF ASHRAM ROAD,
AHMEDABAD-380 009. PHONE: +91 (079) 2658-8829/4488, 40236236
FAX : +91 (079) 2658 3596 WWW.VMSCONSULTANTS.COM

SHEET SIZE	DRAWING NO.	FOR	REVISION:
A1	A.G.101	A	R2