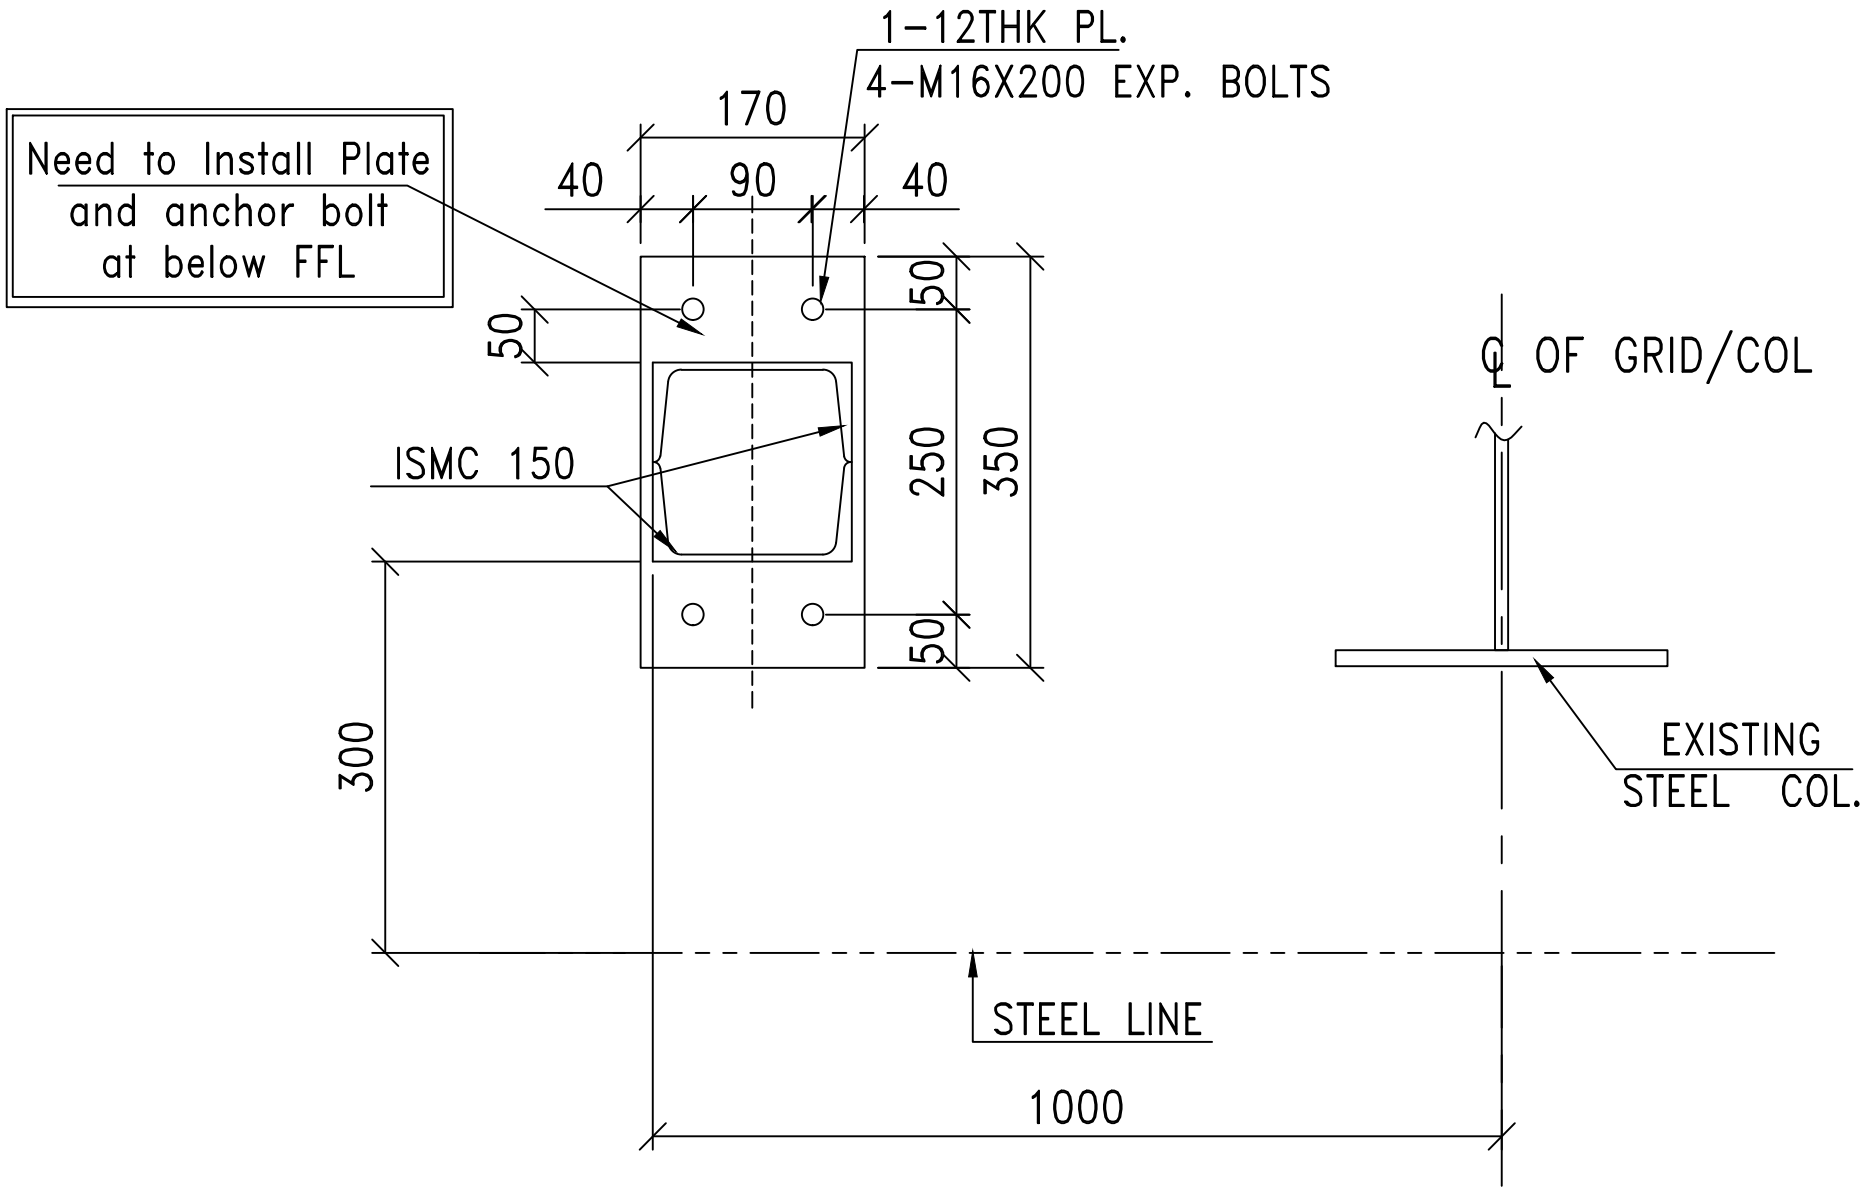
1-12THK PL.
4-M16X200 EXP. BOLTS
Need to Install Plate
and anchor bolt
at below FFL
170
40
90
40
50
50
250
350
50
ISMC 150
300
℄ OF GRID/COL
EXISTING
STEEL COL.
STEEL LINE
1000

DETAIL - D3