

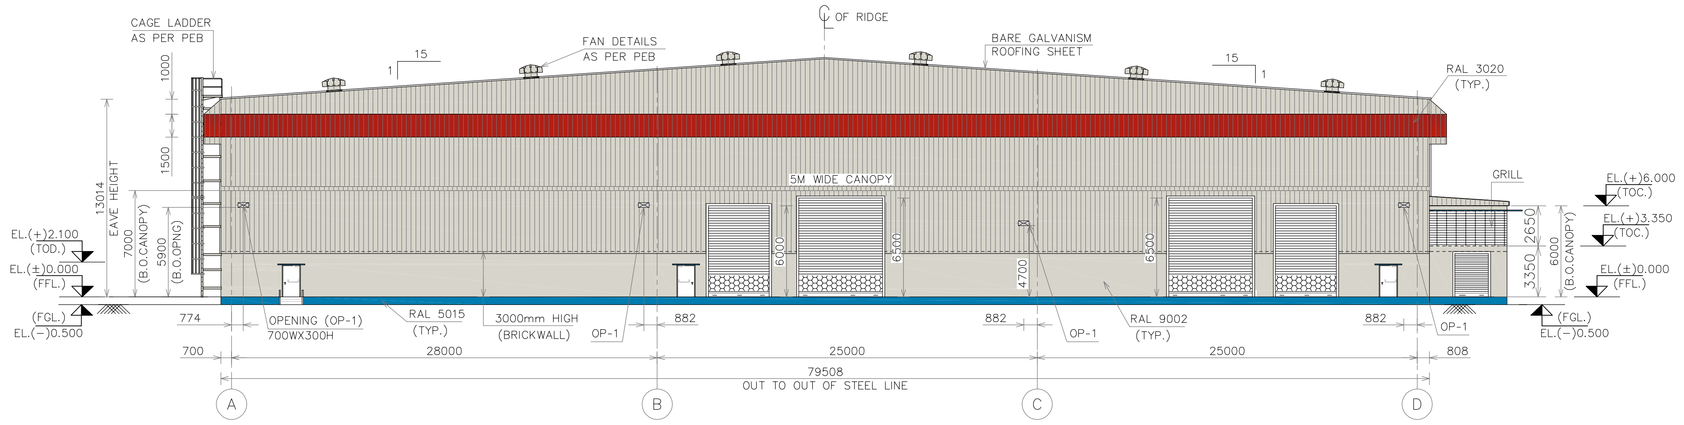


ELEVATION 01
1:200

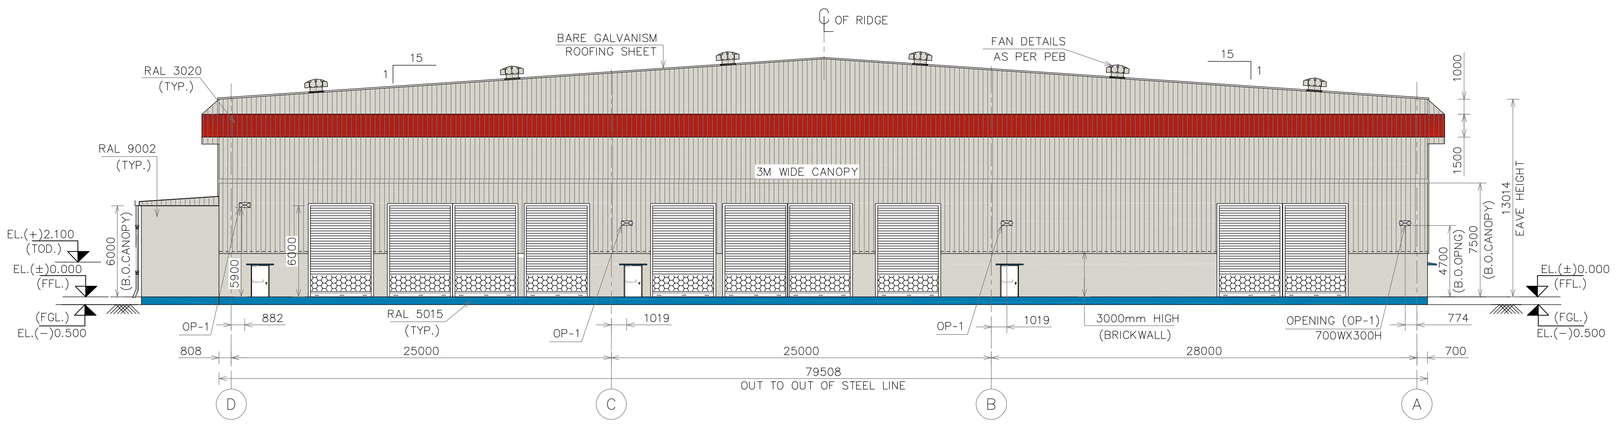


ELEVATION 02
1:200

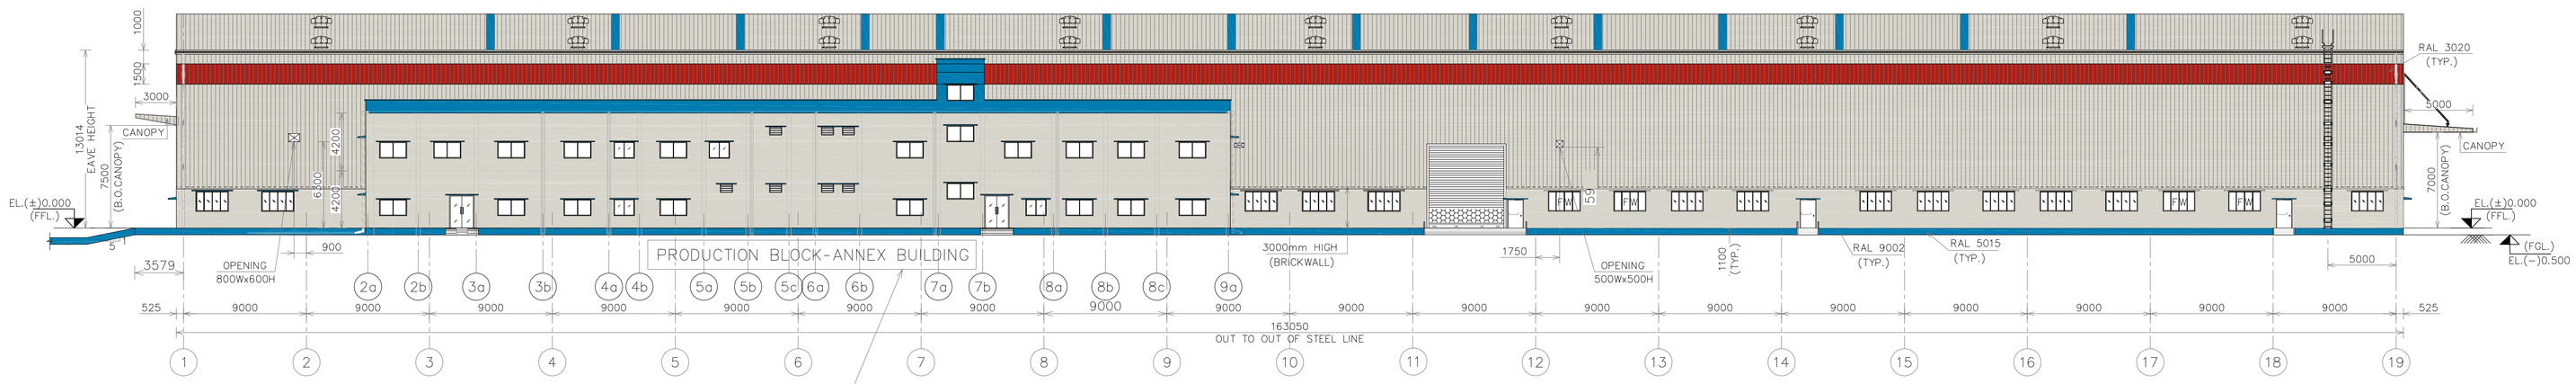


ELEVATION 03
1:200

WALL OPENINGS FOR HVAC SHALL BE AS PER ARCHITECTURAL DWG. OF ANNEX BUILDING

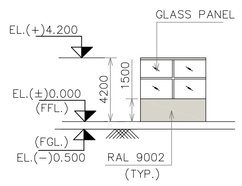


TYP. OFFICE ELEVATION
1:200

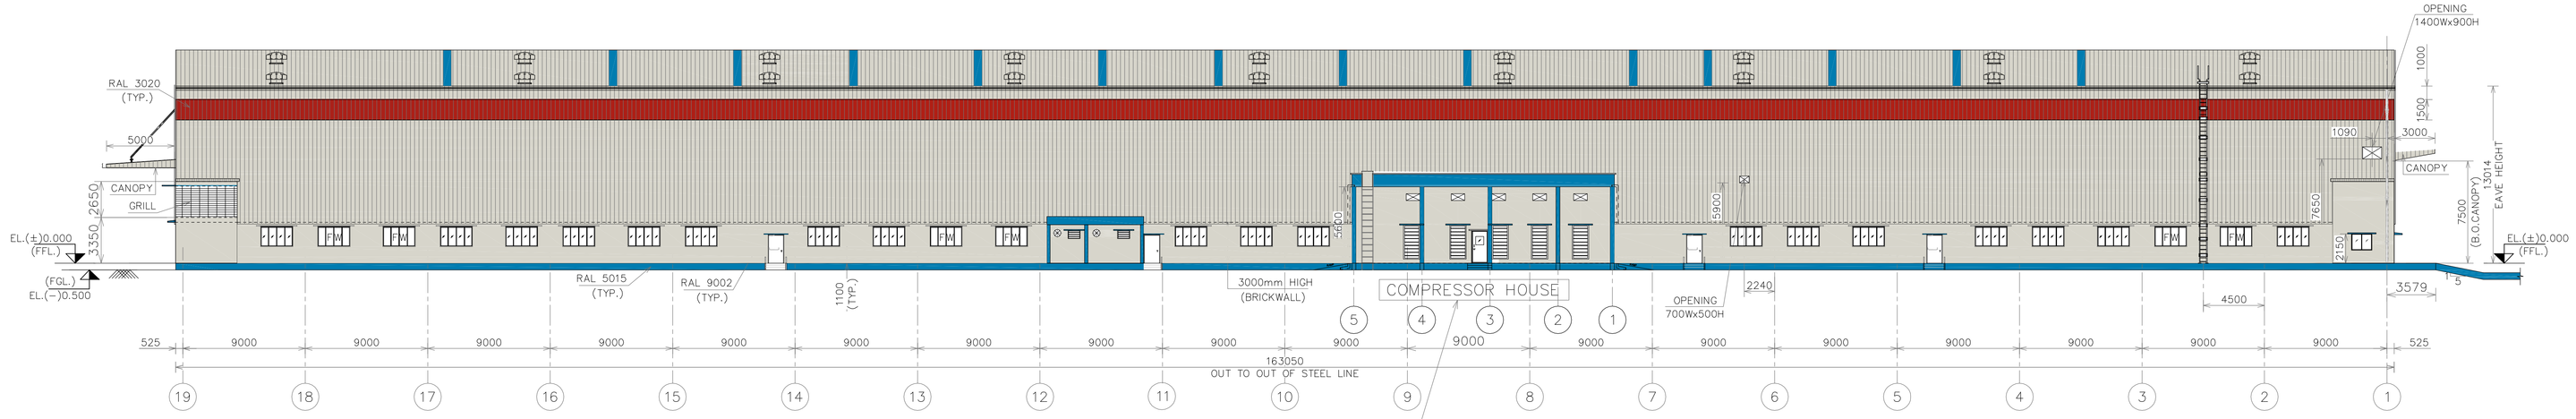


WALL OPENINGS FOR HVAC SHALL BE AS PER ARCHITECTURAL DWG. OF COMPRESSOR HOUSE


ELEVATION 04
1:200

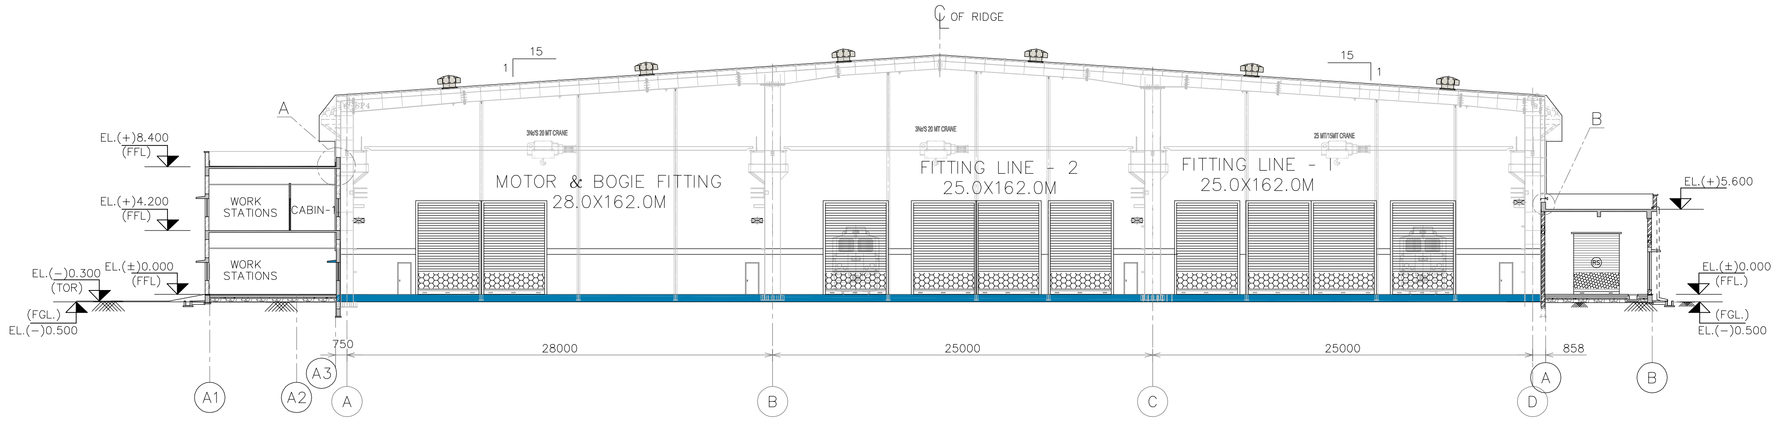


SECTION A-A
1:200

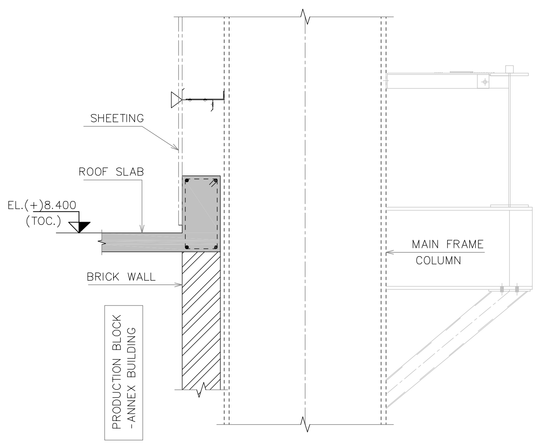


DETAIL A
1:20

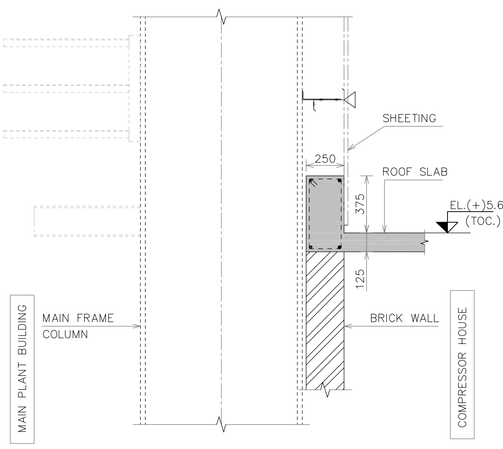


DETAIL B
1:20

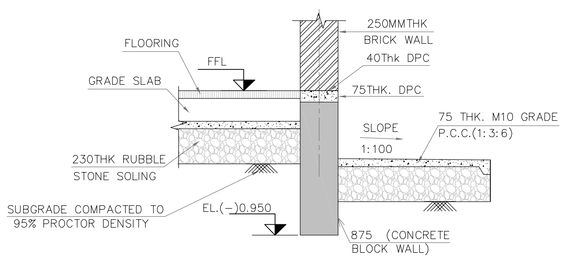

TYP. DETAIL OF PLINTH PROTECTION
1:20

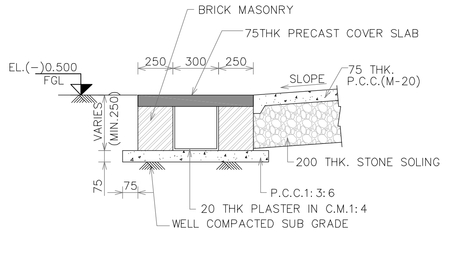

TYP.DETAIL FOR DRAIN TRENCH
1:20

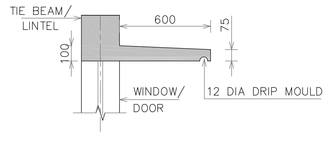

TYPICAL DETAIL OF LINTEL WITH CHAJJA ALOFT
(300MM PROJECTION ON EITHER SIDE OF OPENING FOR CHAJJA)
1:20

NOTES

1. ALL DIMENSIONS ARE IN MILLIMETRES AND LEVELS ARE IN METRES, UNO.
2. EL(±)0.000 REFERS TO FINISHED FLOOR LEVEL WHICH CORRESPONDS TO RL 44.30
3. FRESH AIR REQUIREMENT ARE MET BY
   a) 32 NOS OF 2.4mx1.5m OPENABLE WINDOWS
   b) 40% OF ROLLING SHUTTER AREAS

LEGEND

℄ : CENTER LINE
EL : ELEVATION
TYP : TYPICAL
FFL : FINISHED FLOOR LEVEL
FGL : FINISHED GROUND LEVEL

REFERENCE

1. FOR STRUCTURAL STEEL DETAILS REFER M/S. PEBS PENNER DRAWING NO. BR-1351-01 SHEET A1 TO A2 & E01 TO E15.
2. FOR PLAN & MARKINGS REFER DWG NO: TPL-3452-X9100-EC-AC-6200.

REV.NO.	DATE	REVISION	CIVIL	MECH	ELEC	INST	APPD	DRAWN
1	28.02.17	ISSUED FOR APPROVAL					AS	GMN
0	09.02.17	ISSUED FOR APPROVAL					AS	GMN

CLEARED

THIS DRAWING IS PROPERTY OF **"TATA PROJECTS LIMITED"** MUST NOT BE PASSED ON TO ANY PERSON OR BODY NOT AUTHORIZED BY US TO RECEIVE IT NOR BE COPIED OR OTHERWISE MADE USE EITHER IN FULL OR IN PART BY SUCH PERSON OR BODY WITHOUT OUR PRIOR PERMISSION IN WRITING.

EPC CONTRACTOR
TATA PROJECTS LIMITED
H. NO.1-7-80 TO 87, "MITHONA TOWERS - 1"
PRENDERGHAST ROAD, SECUNDERABAD - 500003.

PROJECT TITLE
PLANT FACILITY FOR
MADHEPURA ELECTRIC LOCOMOTIVE PRIVATE LIMITED
AT MADHEPURA, BIHAR.

OWNER
MADHEPURA ELECTRIC LOCOMOTIVE PRIVATE LIMITED

OWNER A/E CONSULTANT :
SEMAC CONSULTANTS PVT LTD
6-1-276, 2ND FLOOR, ARCHANA BLOCK,
CONJEEVARAM HOUSE, PADMARAO NAGAR
SECUNDERABAD - 500025.

	SIGNATURE	DATE
DRAWN	GMN	09.02.17
DESIGNED	RS	09.02.17
CHECKED	AS	09.02.17
DEPT.HEAD	AS	09.02.17

RELEASED FOR :
- INFORMATION
- APPROVAL ✓
- ENGINEERING
- CONSTRUCTION

DWG. TITLE:
FACTORY AREA
MAIN FACTORY BUILDING
ELEVATIONS & SECTIONS

DEPT. CIVIL | JOB NO. 0000 | SCALE: – | SHEET: 1 OF 1 | SIZE : A0

FILE NAME. ALSTOM-M-AR-MFB-102 | REV./ISSUE

DWG.NO. TPL-3452-X9100-EC-AC-6201 | R1