

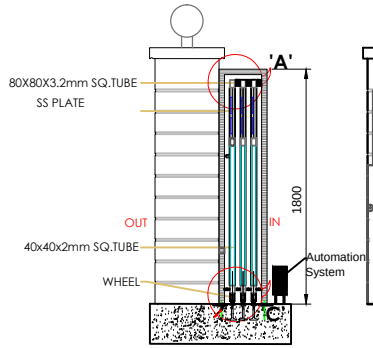



SIDE VIEW

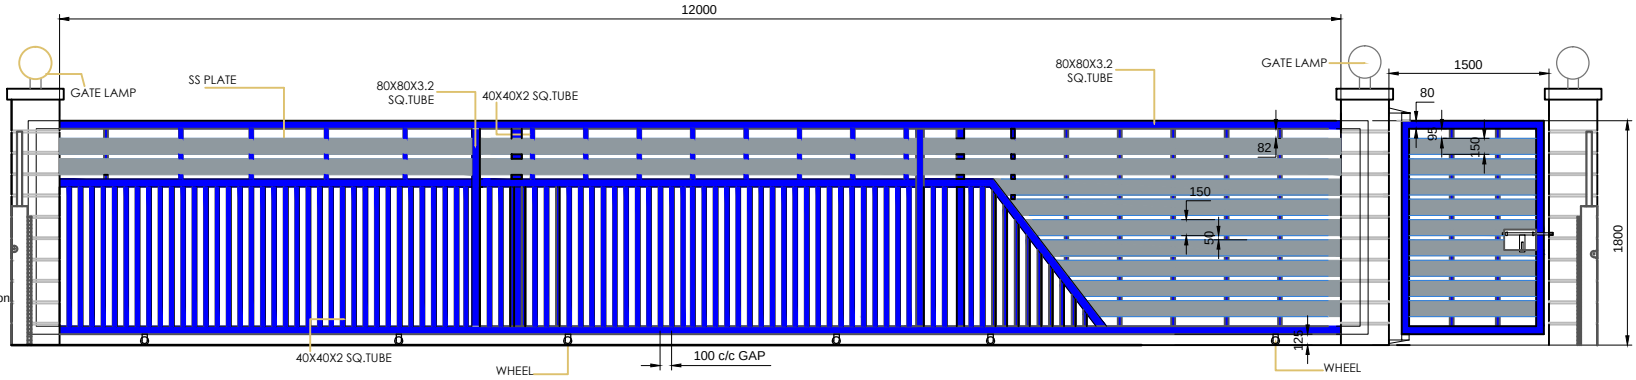


OUTSIDE ELEVATION

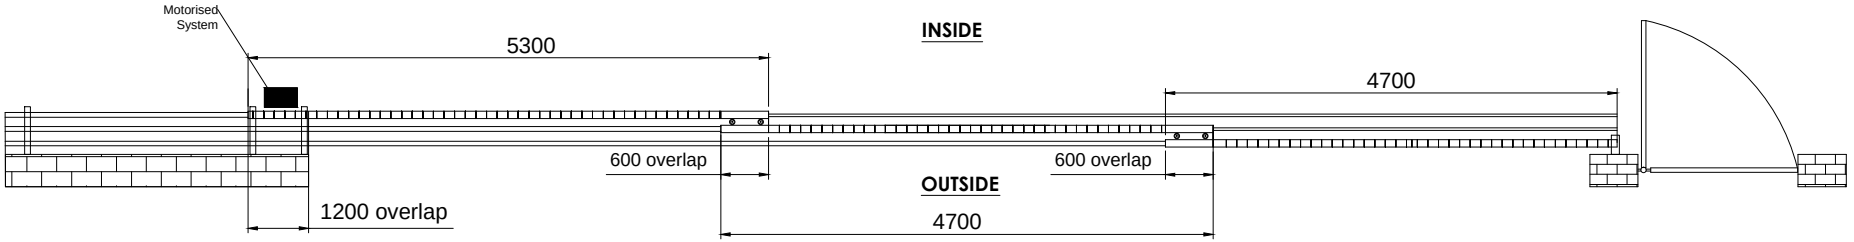

Clear Opening size - 12000mm x 1800mm
Total No. of Leaf - 3 Leaf
NOTE :- *ALL REQ. CIVIL WORK WILL BE IN CLIENT SCOPE.

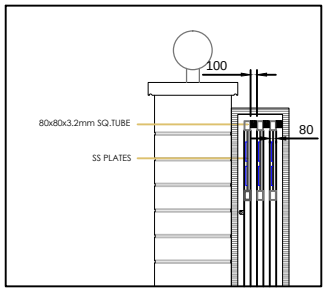

DETAIL AT 'A'

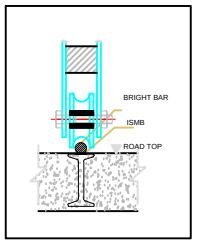

DETAIL AT 'C'

This drawing & designing is the property of NIHVA TECHNOLOGIES. Not be sold or copy to any other concern.

TITLE	TELESCOPIC SLIDING GATE		NIHVA TECHNOLOGY PVT. LTD. PUNE Tel : 020 66304033 Email:- info@nihva.com Website:- www.nihva.com
	SIGN	DATE	
DRAWN	OMKAR	19/03/16	CLIENT - TOYOTA
CHECK	ANIL	19/03/16	PROJECT - TOYOTA
REV.	00		SITE -
APPROVAL			DWG. NO. : NIHVA/15-16/223/R01
If any queries contact : projects@nihva.com			SCALE: 01 / WT: / SHEET: 01 OF 01
ALL DIMENSION ARE IN mm			