



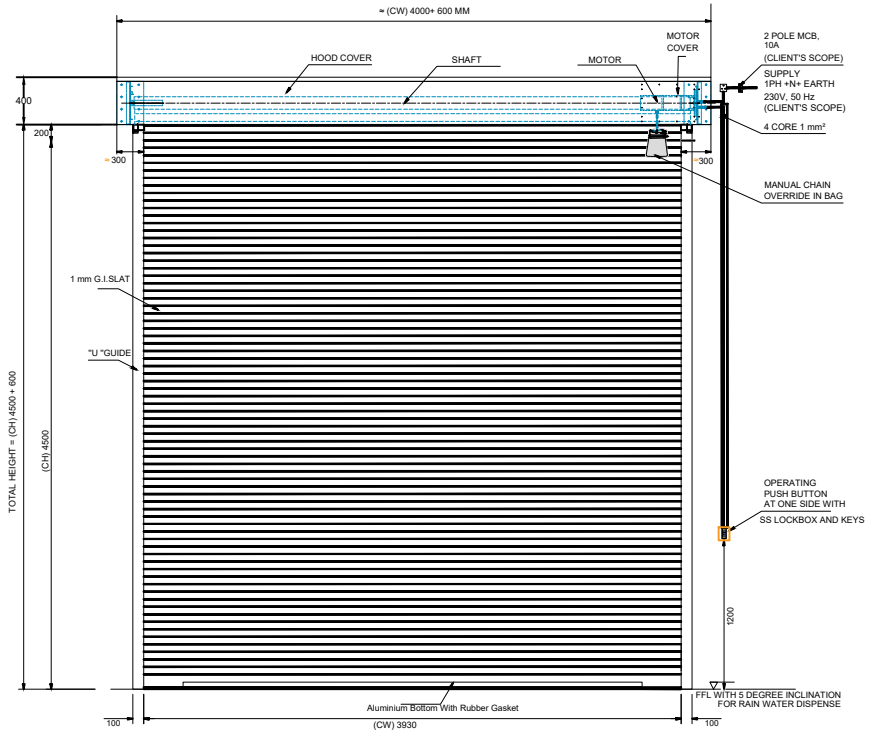

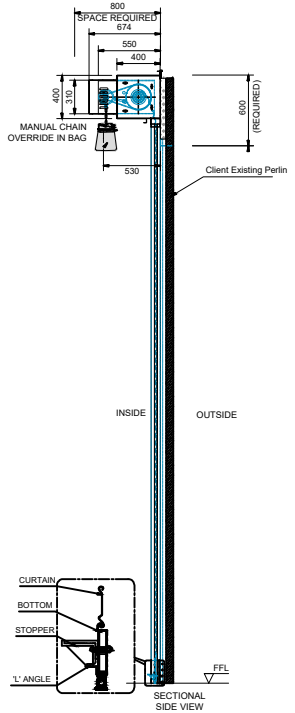

INSIDE ELEVATION

TECHNICAL SPECIFICATION:-

SR.	SPECIFICATION	DETAILS
1.	Description & Drive	Motorised Rolling Shutter (Indirect Drive) with Manual Chain Arrangment
2.	Location Area	Inside
3.	Mounting Surface	Side Brackets: M.S Structure (Client Scope)
4.	Slat	Flat profile 80 mm G.I. Slat - 1.0 mm Thk
5.	Bottom Profile	Aluminium Bottom With Rubber Gasket
6.	Guide Profile	M.S." U " Shape profile 100 x 2.5 mm Thk. With Rubber Gasket on Guide .
7.	Hood Cover & Motor Cover	Made of GI Sheet Thickness 0.9 mm
8.	Accessories	Push Button at One Side
9.	Surafce Finish & Painting	Primer & Duco Paint (Matt Finish) Color Shed-Light Blue RAL 5015

SHUTTER SIZES :-

SR.	CLEAR WIDTH	CLEAR HEIGHT	QTY.
01	3930	4500	01

This drawing & designing is the property of NIHVA TECHNOLOGIES. Not to be sold or copied to any other concern

TITLE :- MOTORISED ROLLING SHUTTER	NAME	DATE	NIHVA TECHNOLOGIES PVT. LTD. PUNE Tel : 020 66304033 Email:- info@nihva.com Website:- www.nihva.com
DRAWN	S.J.	29/02/2024	CLIENT - Power Erectors
CHECK	A.K.	29/02/2024	PROJECT -ROLLING SHUTTER
APPROVAL	V.T.	29/02/2024	FORMAT NO - NIHVA-DD-F-03
			DWG. NO. : NIHVA/23-24/NTPL- 219 A — REV-01
			SCALE: NTS — WT: — SHEET: 01 OF 01
ALL DIMENSION ARE IN mm			If any queries contact : design@nihva.com