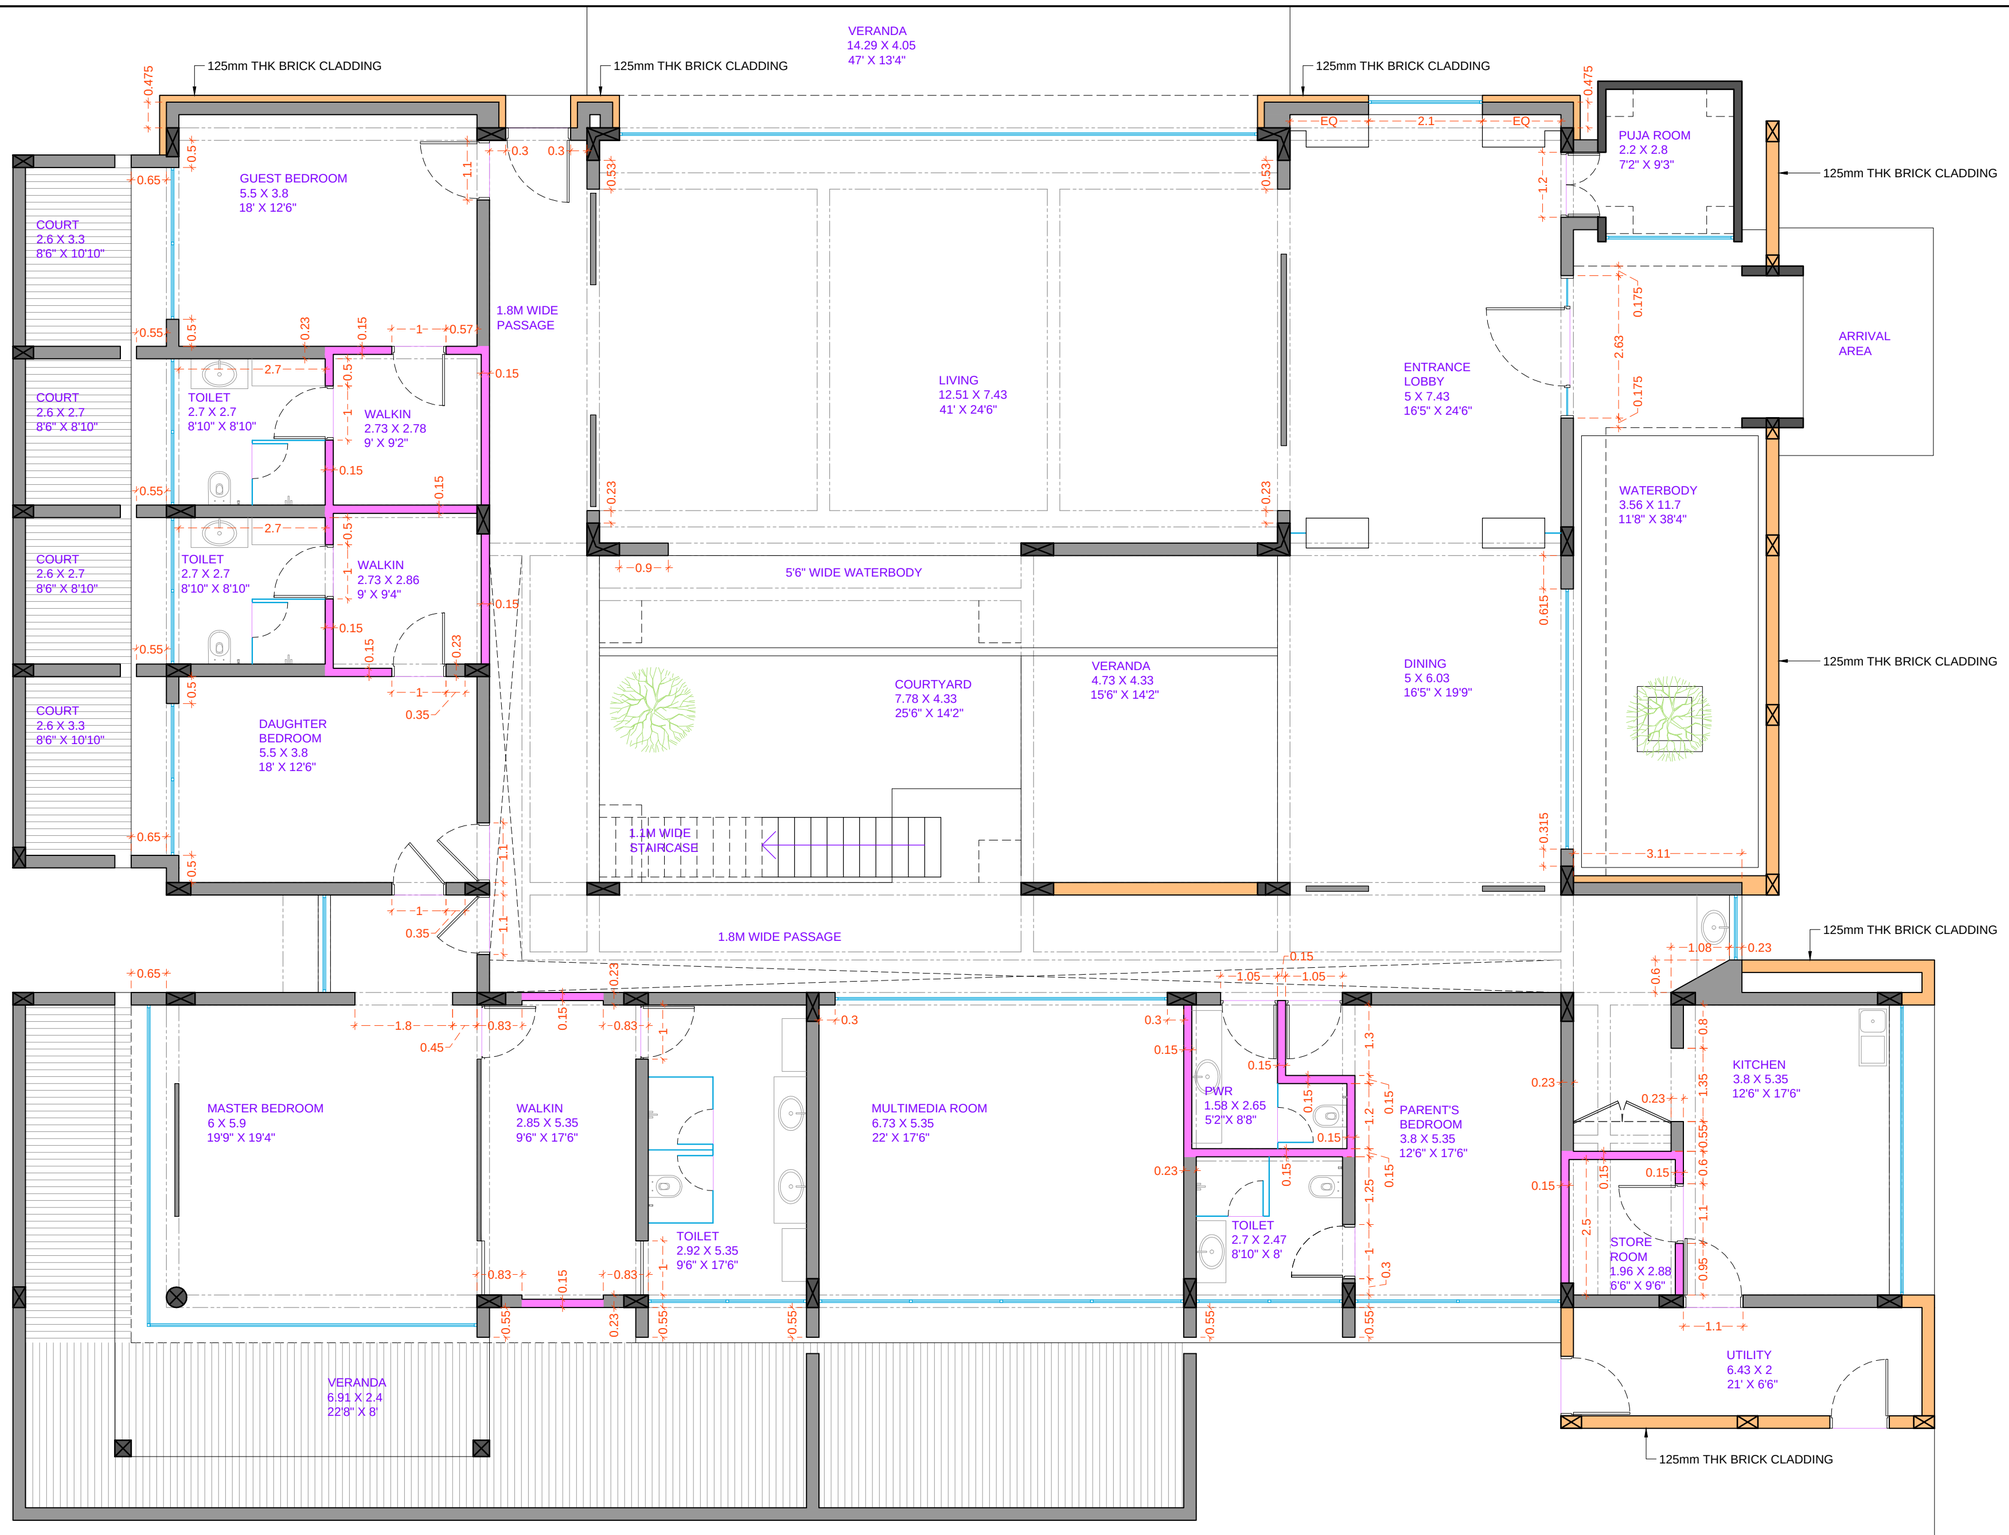


PROJECT STAGE
WORKING DRAWING

PROJECT
BUNGALOW AT MANJRI

1. THIS DRAWING IS PROPERTY OF STUDIO HUMANE ARCHITECTS AND SHALL NOT BE USED FOR ANY OTHER PURPOSE THAN SPECIFIED WITHOUT PERMISSION.
2. DRAWING IS NOT TO BE SCALED. WRITTEN DIMENSIONS TO BE FOLLOWED.
3. THIS DRAWING IS TO READ IN CONJUNCTION WITH OTHER RELEVANT ARCHITECTURAL / ENGINEERING DRAWINGS.
4. ALL RCC / STRUCTURAL DETAILS TO BE DONE AS PER THE STRUCTURAL ENGINEER'S DRAWINGS.
5. ALL DETAILS REGARDING SERVICES TO BE DONE AS PER MEP / RESPECTIVE SERVICE CONSULTANTS.
6. DISCREPANCIES IF ANY SHOULD BE IMMEDIATELY BROUGHT TO THE NOTICE OF THE ARCHITECT BY CONTRACTOR /IN WRITING PRIOR TO CONSTRUCTION.

STRUCTURAL ENGINEER
SANTOSH PADSALGE

CLIENT
MR.SANKET TILEKAR

NORTH

DRAWING TITLE
BRICK LAYOUT

SCALE 1:80 DATE **30 05 2022**

DRAWING NO. **ST_CS_06**

DRAWN	CHECKED	APPROVED
NEMICHAND	SUNIL H.	SUNIL H.

PURPOSE AND STAMP
FOR CONSTRUCTION
DATE :
SIGN :

STUDIO HUMANE
ARCHITECTS, LANDSCAPE ARCHITECTS AND INTERIOR DESIGNERS
#2 Prassana, Lane 4,Pushpak Park,
Off, ITI Rd, Aundh, Pune,
Maharashtra 411007

ANY CHANGES ON SITE TO BE DONE BY ARCHITECTS ORDER ONLY. BLUE PRINT NOT BE SCALED. WRITTEN DIMENSION TO BE FOLLOWED. THIS DRAWING SHOULD NOT BE REPRODUCED WITHOUT THE WRITTEN PERMISSION OF THE OWNERS.