

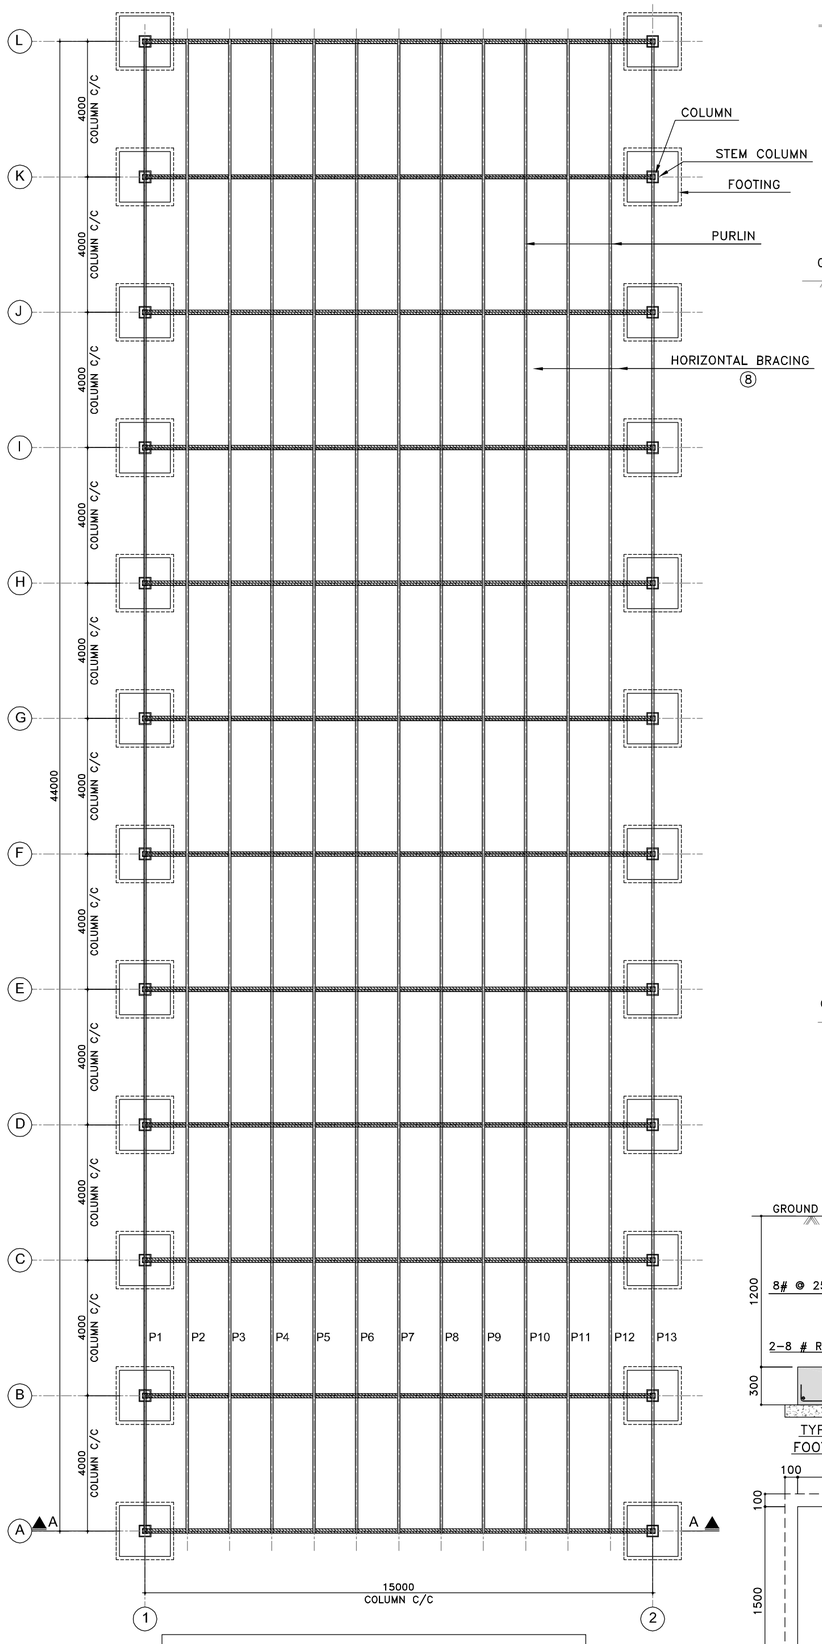



STRUCTURAL LAYOUT PLAN FOR PRACTICE PITCHES COVER SHED

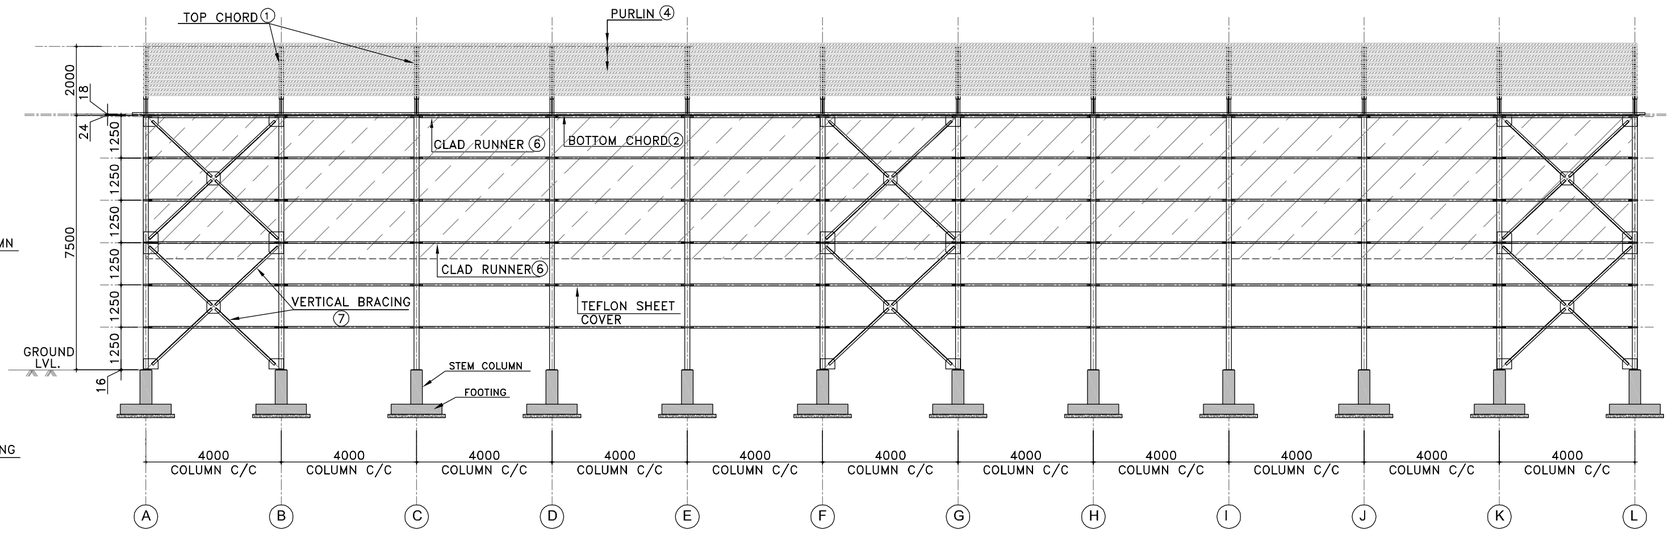


SIDE ELEVATION OF THE STRUCTURE

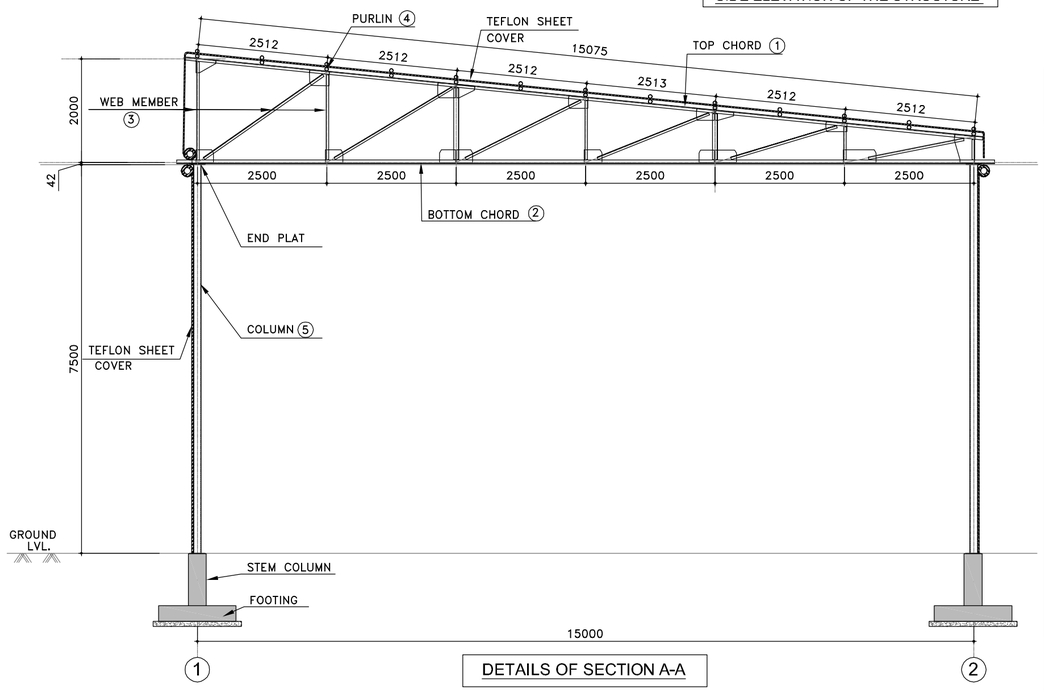

DETAILS OF SECTION A-A

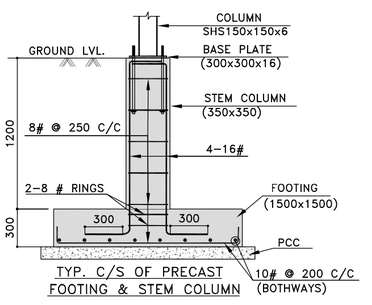

TYP. C/S OF PRECAST FOOTING & STEM COLUMN

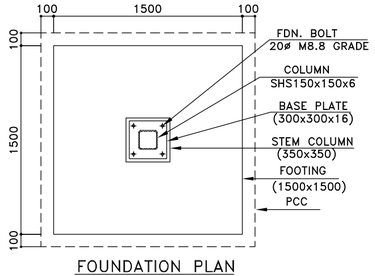

FOUNDATION PLAN
(SCALE 1:30)

BILL OF MATERIAL

SR.No.	SPECIFICATIONS			LENGTH(m)	QTY.	Wt.(kg)/ m	TOTAL WT.	
							In kg.	Tonnes
1	TRUSS	TOP CHORD	ISA 60 X 60 X 4 (2 nos.)	15.075	24	3.7	1338.66	1.34
2		BOTTOM CHORD	ISA 65 X 65 X 5 (2 nos.)	15	24	4.9	1764	1.76
3		WEB	ISA 50 X 50 X 3 (2 nos.)	24.5	48	2.3	2704.8	2.70
4	PURLINS		CHS 42.4 x 3.2	44	26	3.01	3443.44	3.44
5	COLUMNS		SHS 150 X 150 X 6	7.5	24	26.4	4752	4.75
6	CLAD RUNNER		SHS 60 x 60 x 3.2	528	1	5.5	2904	2.90
7	VERTICAL BRACING		2 ISA 65 X 65 X 5	5.483	24	4.9	1289.6	1.29
						TOTAL WT.(Tonnes)		18.20

NOTES:-

1	ALL DIMENSIONS ARE IN MM UNLESS NOTED OTHERWISE.
2	ONLY FIGURED DIMENSIONS SHALL BE FOLLOWED.
3	# REPRESENTS TMT STEEL OF Fe550 D GRADE CONFORMING IS 1786
4	USE CONCRETE GRADE = M40, USE SELF COMPACTING CONCRETE FOR COLUMN CORE, BEAM TOP CONCRETING OF THE SAME GRADE.
5	CLEAR COVER TO REINFORCEMENT IN FOOTING=50 mm, STEM COLUMN=45 mm, BEAM=30 mm.
6	ALL ANCHORAGES & LAP LENGTH SHALL BE (Ld)=36 ø & ALL LAPS SHALL BE STAGGERED.
7	ALL LEVELS ARE w.r.t. G.F.L. ± 0.00
8	ALL THE DIMENSIONS & CENTRE LINES SHALL BE VERIFIED FROM ARCH.
9	SBC OF STRATA – 15 T/M^2

REVISION STATUS AND DETAILS

NO	DATE	REVISION	DEALT	CHECKED	APPD.

DESIGNED & CHECKED SIGNATURE WITH DATE		DRG. VERIFIED BY		DRG. APPROVED BY
DRAWN R P S	03.08.2026	ARCHITECT		Y. P. KAJALE Regd. Structural Engineer State Govt. of Maharashtra No.STATE/R/2025/APL/16187 MCGM NO.: STR: 840015350 Existing BP. No.: STR/K/170
DESIGNED	03.08.2026	MEP ENGR.		
CHECKED		ELECT. ENGR.		

SHIRKE®
CONSULTANCY SERVICES

THIS DRAWING AND ALL SPECIFICATIONS, DATA AND OTHER INFORMATION CONTAINED THEREIN ARE CONFIDENTIAL AND THE SOLE PROPERTY OF SHIRKE CONSULTANCY SERVICES MUNDHWA PUNE-36. IT IS FORBIDDEN TO USE, REPRODUCE, MODIFY OR IN ANY MANNER REVEAL ITS CONTENTS EXCEPT FOR THE PURPOSES FOR WHICH IT WAS INTENDED.

CLIENT
B. G. SHIRKE CONST. TECH. PVT. LTD.
PUNE - 411036

PROJECT BY

SHIRKE CONSULTANCY SERVICES
72-76, Industrial Estate, Mundhwa, Pune – 411 036, Maharashtra (India)
TEL: +91 20 26708100 E-MAIL: shirkeconsultancy@shirke.co.in

PROJECT: MCA CLUB/ INDOOR CRICKET ACADEMY ON

LOCATION: R.G PLOT AT G-BLOCK BANDRA- KURLA COMPLEX

PROJECT BY : BANDRA, MUMBAI

MCA :- PRACTICE PITCHES COVER SHED

SCALE: AS SHOWN	DRG. TITLE:	GENERAL ARRANGEMENT DWG. FOR PRACTICE PITCHES COVER SHED.	
JOB NO.: 12-2023	DRG. NO.	SCS / MCA / BKC / MUMBAI / WD / 01	REV. NO. 0

D:\RPS\MCA OP-3.DWG

A2