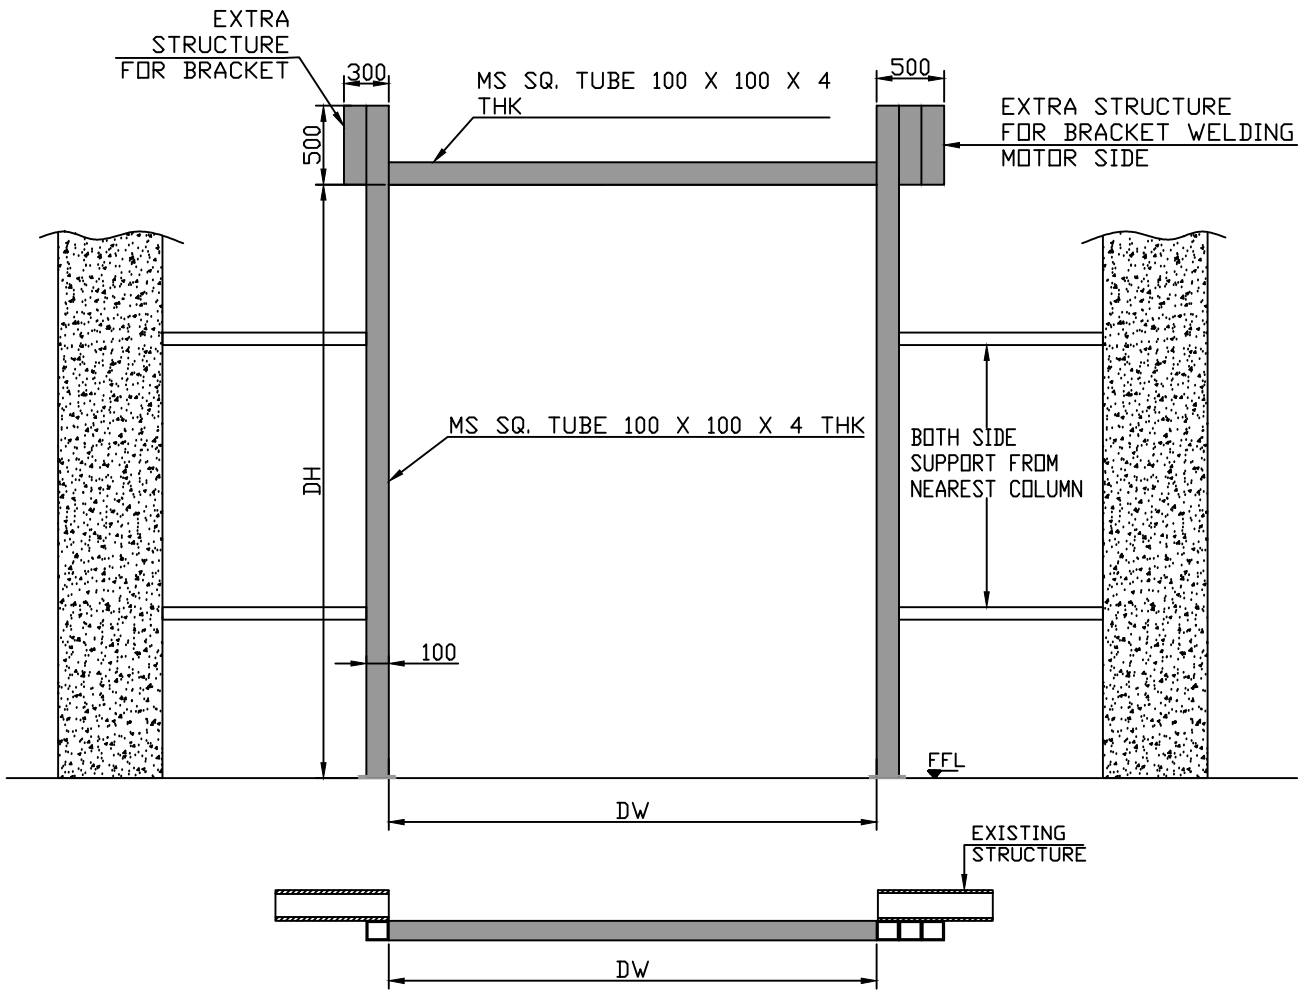



| SR NO | DW | DH | QUANTITY |
|---|---|---|---|
| 1 | 2400 | 3000 | 4 |
| 2 | 1800 | 3000 | 2 |

DOOR DIMENSION

Tolerance ±3 mm (for all dimensions)

Dimensions in [ ] ==> clearance for installation

This drawing & design is the property of NIHVA TECHNOLOGIES. Not to be sold or copied to any other concern.

TITLE - RR300 PLUS ALU HSD STRUCTURE

NIHVA TECHNOLOGIES PVT. LTD. PUNE
Tel : 020 66304033
Email:- info@nihva.com
Website:- www.nihva.com

| | NAME | SIGN | DATE |
|---|---|---|---|
| DRAWN | P.V.A | | 25.03.19 |
| CHECK | V.M.T | | 25.03.19 |
| APPROVED | | | |

CLIENT - UNITED ARCHITECT

PROJECT - A RAYMOND

LOCATION - CHAKAN, PUNE

If any queries contact:sales@nihva.com

DWG. NO. -NIHVA/18-19/0317 REV- 0

ALL DIMENSION ARE IN mm

SCALE: NTS WT: SHEET:

NOTE-
1. ALL CIVIL WORK WILL BE CLIENT'S SCOPE.
2.STRUCTURE REQUIRED FOR SHUTTER IS IN CLIENT'S SCOPE.