
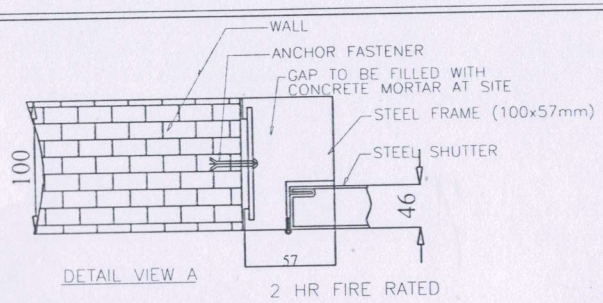


DETAIL VIEW A

2 HR FIRE RATED

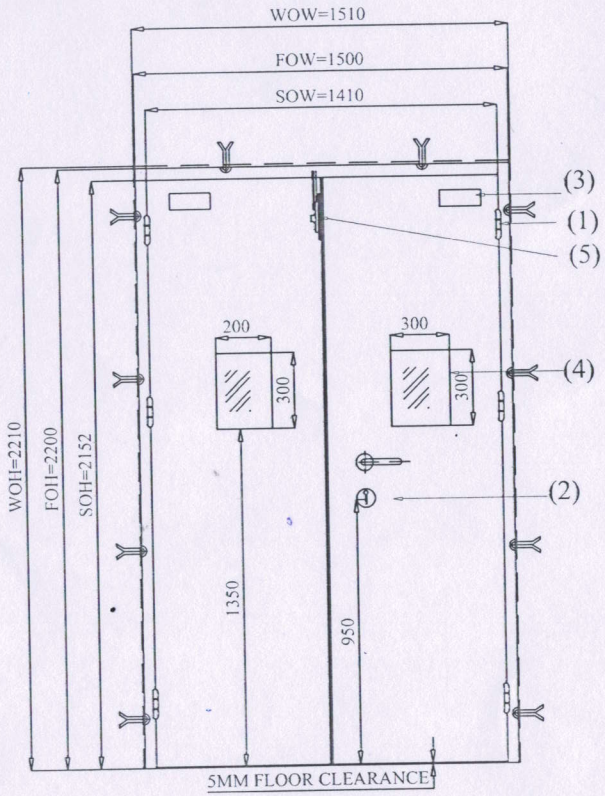

5MM FLOOR CLEARANCE

NOTES:-

ALL DIMENSIONS ARE IN MM.

A. ABBREVIATION

Wall Opening Width : WOW
Wall Opening Height : WOH
Frame Opening Height : FOH
Frame Opening Width : FOW
Shutter Opening Height : SOH
Shutter Opening Width : SOW

MATERIAL OF CONSTRUCTION
2HRS FIRE RATED
REF STD: IS 3614 PART-2: BS: 476

FRAME : G.I. 1.60mm Sheet
SHUTTER : G.I. 1.20mm Sheet

DOOR THICKNESS : 46mm

FRAME PROFILE : 100 x 57mm (Single Ribet)

INFILL MATERIAL : Rock Wool

PAINT: White Colour Both Sides

SCHEDULE OF HARDWARE

1) S.S. Ball Bearing Hinges (Yale Make) - 6 Nos.
2) Mortise Lock with Handle & Cylinder (Yale Make) - 1 Nos.
3) Heavy Duty Door Closer - 2 Nos. (Yale Make)
4) Vision Panel with Fire Rated Glass of Size : 200 x 300mm (6mm Thick Fire Glass) - 2 Nos.
5) Concealed Flush Tower Bolt - 1 Nos.

NIHVA TECHNOLOGIES PVT. LTD. PUNE
Approved

24/11/20

This drawing & design is the property of NIHVA TECHNOLOGIES. Not to be sold or copied to any other concern.

TITLE 1500mm (W) x 2200mm (H) Double Leaf Fire Door

	NAME	SIGN	DATE
DRAWN	S.M.S.		24.11.2020
CHECK			
APPRD.			

If any queries contact : projectsupport@nihva.com

ALL DIMENSION ARE IN mm

NIHVA
NIHVA TECHNOLOGIES PVT. LTD.

NIHVA TECHNOLOGIES PVT. LTD. PUNE
Tel : 020 66304033
Email:- info@nihva.com
Website:- www.nihva.com

CLIENT -

PROJECT -

SITE LOCATION -

DWG. NO. : NIHVA/20-21/VDR/0078 REV- R00

SCALE: NTS WT: SHEET: