


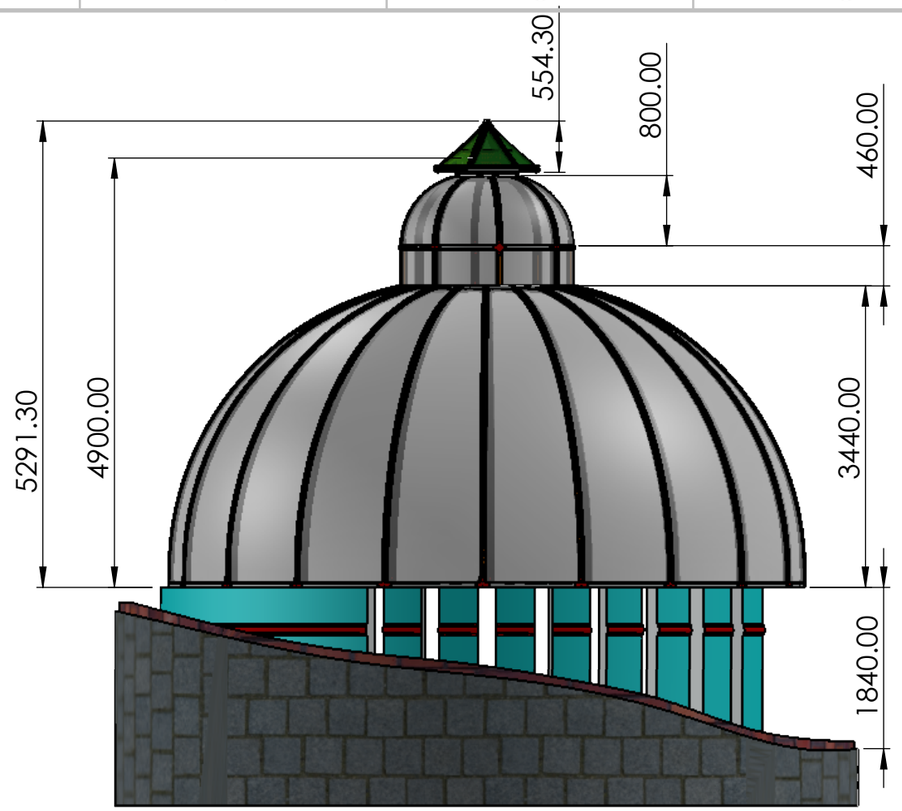


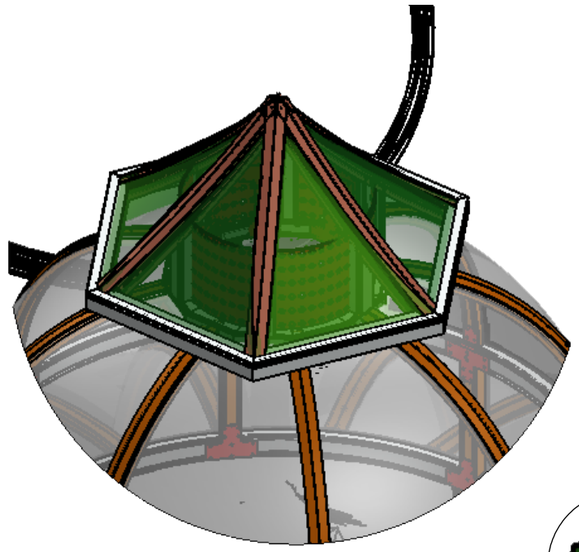

DETAIL A
SCALE 1 : 18

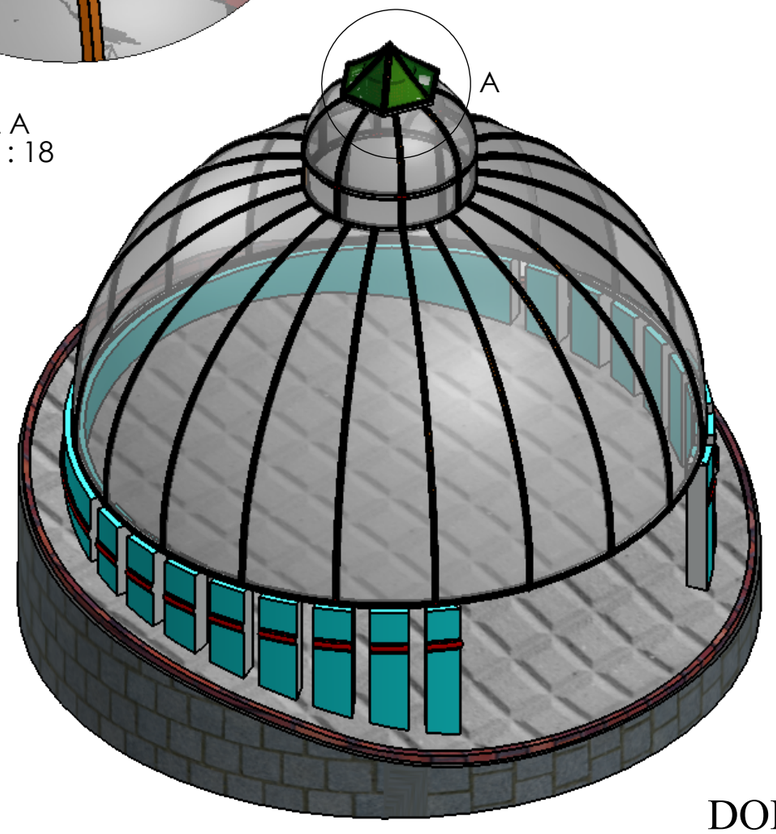


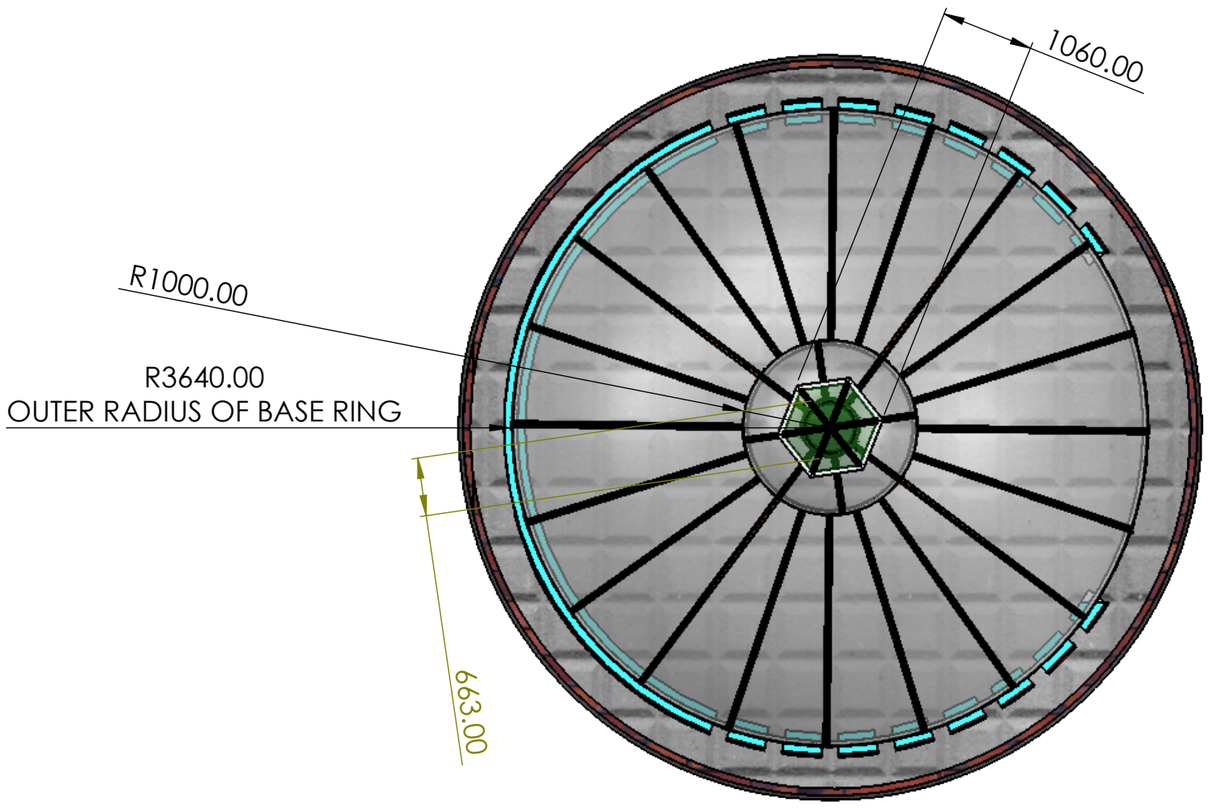

DOME


TITLE - ROOF AUTOMATION				NIHVA TECHNOLOGIES PVT.LTD.PUNE
DWG NO - NTPL-278-PM-001-00-00-00				Website - www.nihva.com
	NAME	SIGNATURE	DATE	PROJECT NO - NTPL-278-PM
DRAWN	V.W		28-04-2025	PRODUCT - DOME
CHK'D	S.W.		28-04-2025	SITE LOCATION - LONAVLA
APPV'D	V.T.		28-04-2025	
if any queries contact - supportautomation@nihva.com				REVISION - QTY - 1
ALL DIMENSION ARE IN mm		A3		SCALE SHEET 1 OF 18


ITEM NO.	PART NUMBER	DESCRIPTION	QTY.
1	..REV03BASE RING	AL 6063_T4	1
2	..REV03VERTICAL SUPPORT PROFILE ABOVE BASE	AL 6063_T4	20
3	..REV03TOP RING SUPPORT	AL 6063_T4	2
4	..REV03VERTICAL SUPPORT ABOBE TOP RING 1	AL 6063_T4	8
5	..REV03TOP VERTICAL SUPPORT 2	AL 6063_T4	8
6	..REV03POLYGOANL SHAPE BY WELDIND	AL 6063_T4	1
7	..REV03POLYCARBONET SHEET1	POLYCARBONET	20
8	..REV03POLYCARBONET SHEET2	POLYCARBONET	8
9	..REV03VIJAY_T PLATE ASM	SS-304	25
10	..REV03New upper plus bend plate	SS-304	8
11	..REV03New Bottom bend joining plate	SS-304	1
12	..REV03PLUS PLATE ASM	SS-304	8
13	..REV03REV 01New upper bend vertical support joining plate ASM	SS-304	8
14	..REV03REV 02VIJAY_T PLATE ASM	SS 304	20
15	..REV03REV 02New Bottom bend joining plate	SS 304	20
16	REV 02New upper BEND vertical support ABOVE BASE RINGjoining plate ASM	SS-304	20
17	..REV03POLYCARBONET SHEET3	POLYCARBONET	8
18	..HEXAGONAL SAHPE MS 60*30*1.5MM THK	MS	1
19	..VERTICAL TUBE FOR CAP SHAPE SUPPORT MS-60*30*1.5MM THK	MS	6
20	..TOP CAP VERTICAL SQ TUBE SUPPOERT MS 60*60*1.5MM THK	MS	6
21	..MESH	MS	1
22	..TOP CAP PC SHEET	POLYCARBONET	6

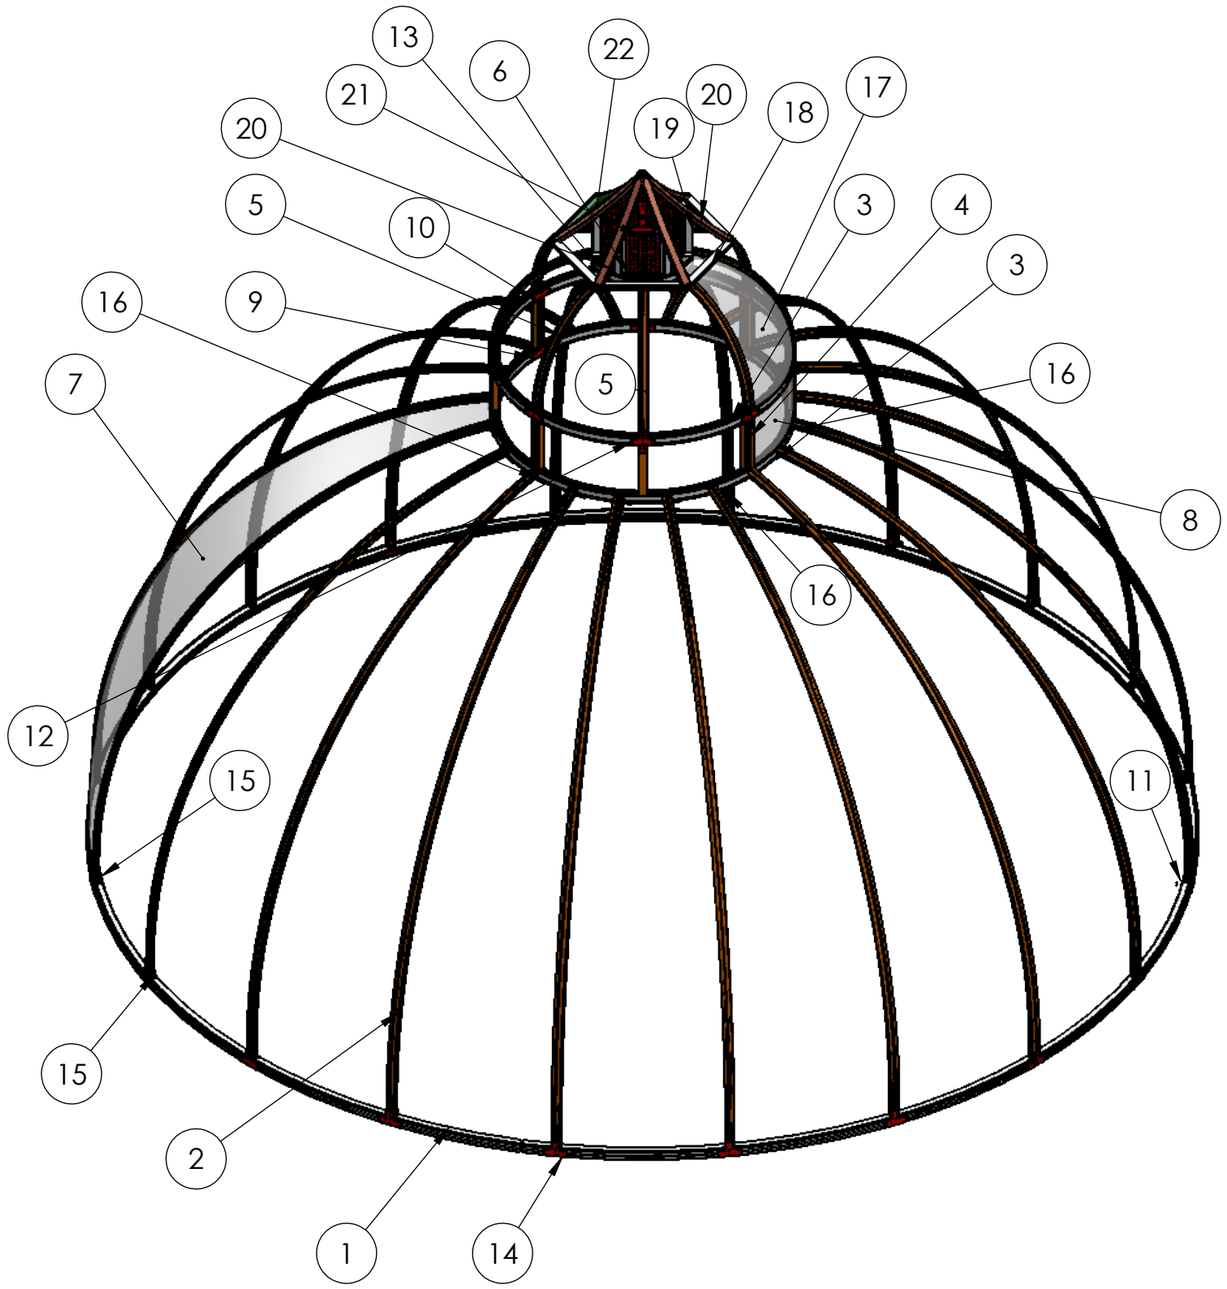

TITLE - ROOF AUTOMATION				NIHVA TECHNOLOGIES PVT.LTD.PUNE
DWG NO - NTPL-278-PM-001-00-00-00				Website - www.nihva.com
	NAME	SIGNATURE	DATE	PROJECT NO - NTPL-278-PM
DRAWN	V.W		28-04-2025	PRODUCT -DOME
CHK'D	S.W.		28-04-2025	SITE LOCATION - LONAVLA
APPV'D	V.T.		28-04-2025	
if any queries contact - supportautomation@nihva.com				REVISION - QTY - 1
ALL DIMENSION ARE IN mm		A3		SCALE SHEET 2 OF 18

ITEM NO.	PART NUMBER	DESCRIPTION	QTY.
1	REV03BASE RING	AL 6063_T4	1

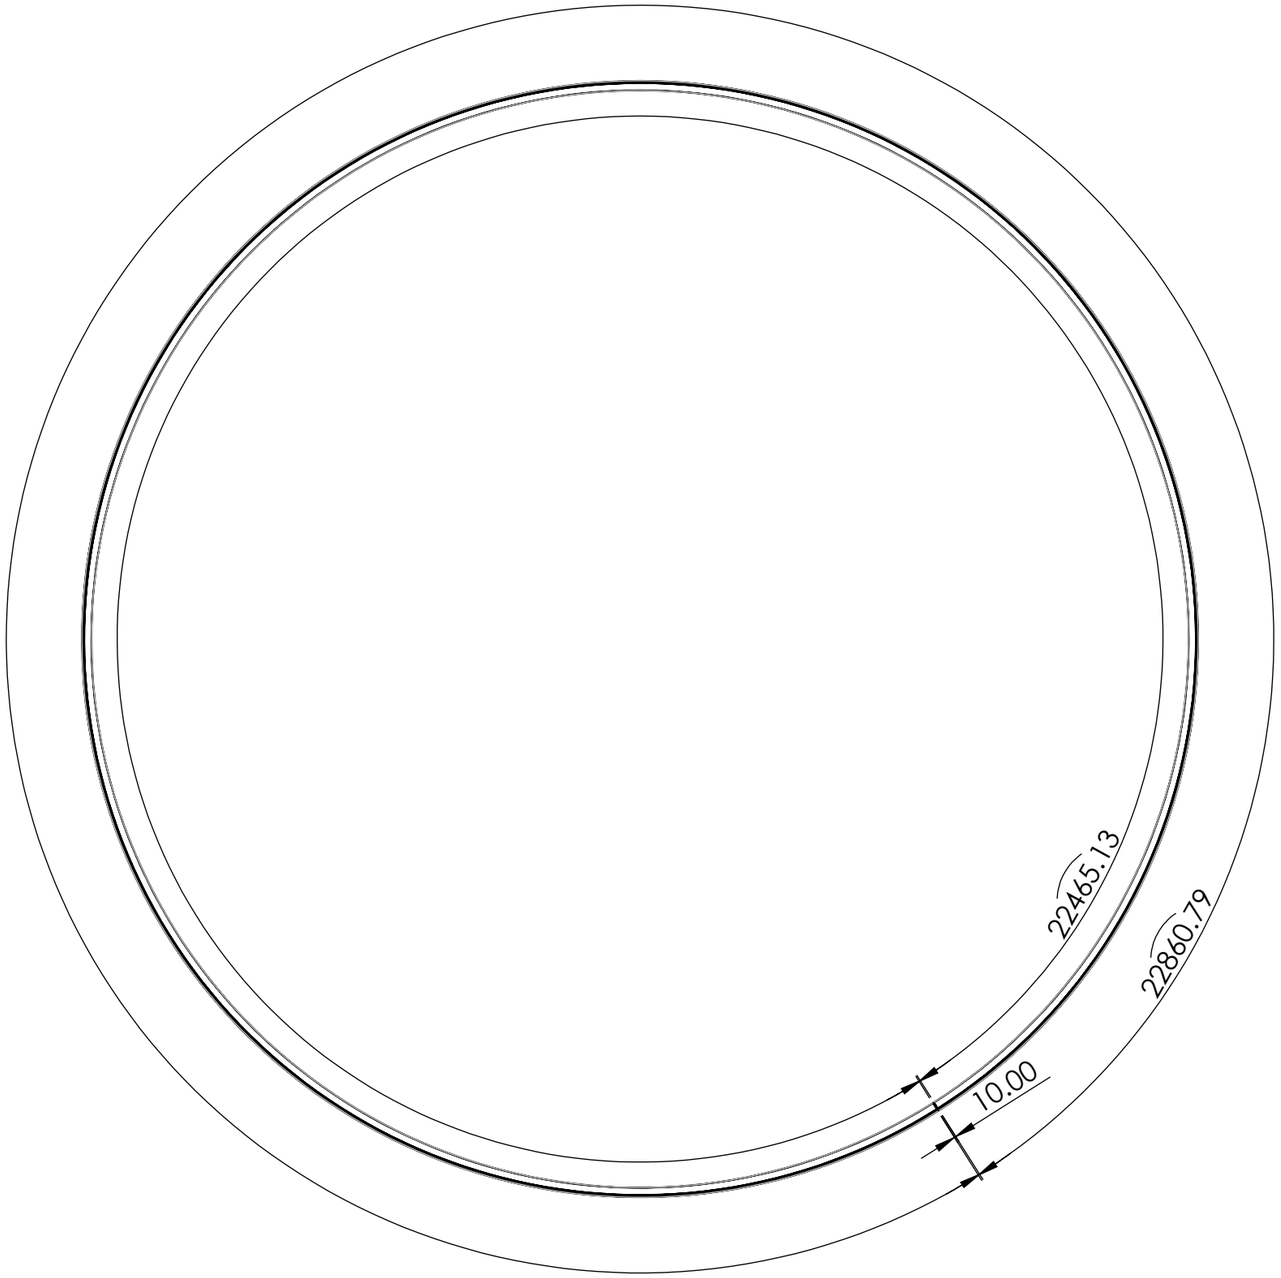


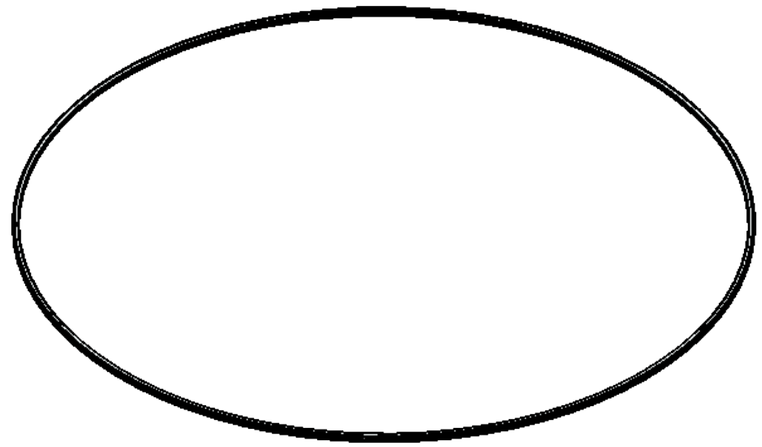


NOTE
BASE RING
USE PROFILE GNT-006

TITLE -ROOF AUTOMATION				NIHVA TECHNOLOGIES PVT.LTD.PUNE
DWG NO - NTPL-278-PM-001-01-00-01				Website - www.nihva.com
	NAME	SIGNATURE	DATE	PROJECT NO - NTPL-278-PM
DRAWN	V.W		28-04-2025	PRODUCT - DOME
CHK'D	S.W.		28-04-2025	SITE LOCATION - LONAVLA
APPV'D	V.T.		28-04-2025	
if any queries contact - supportautomation@nihva.com				REVISION - QTY - 1
ALL DIMENSION ARE IN mm		A3		SCALE SHEET 3 OF 18

ITEM NO.	PART NUMBER	DESCRIPTION	QTY.
1	..REV03VERTICAL SUPPORT PROFILE ABOVE BASE	AL 6063_T4	20

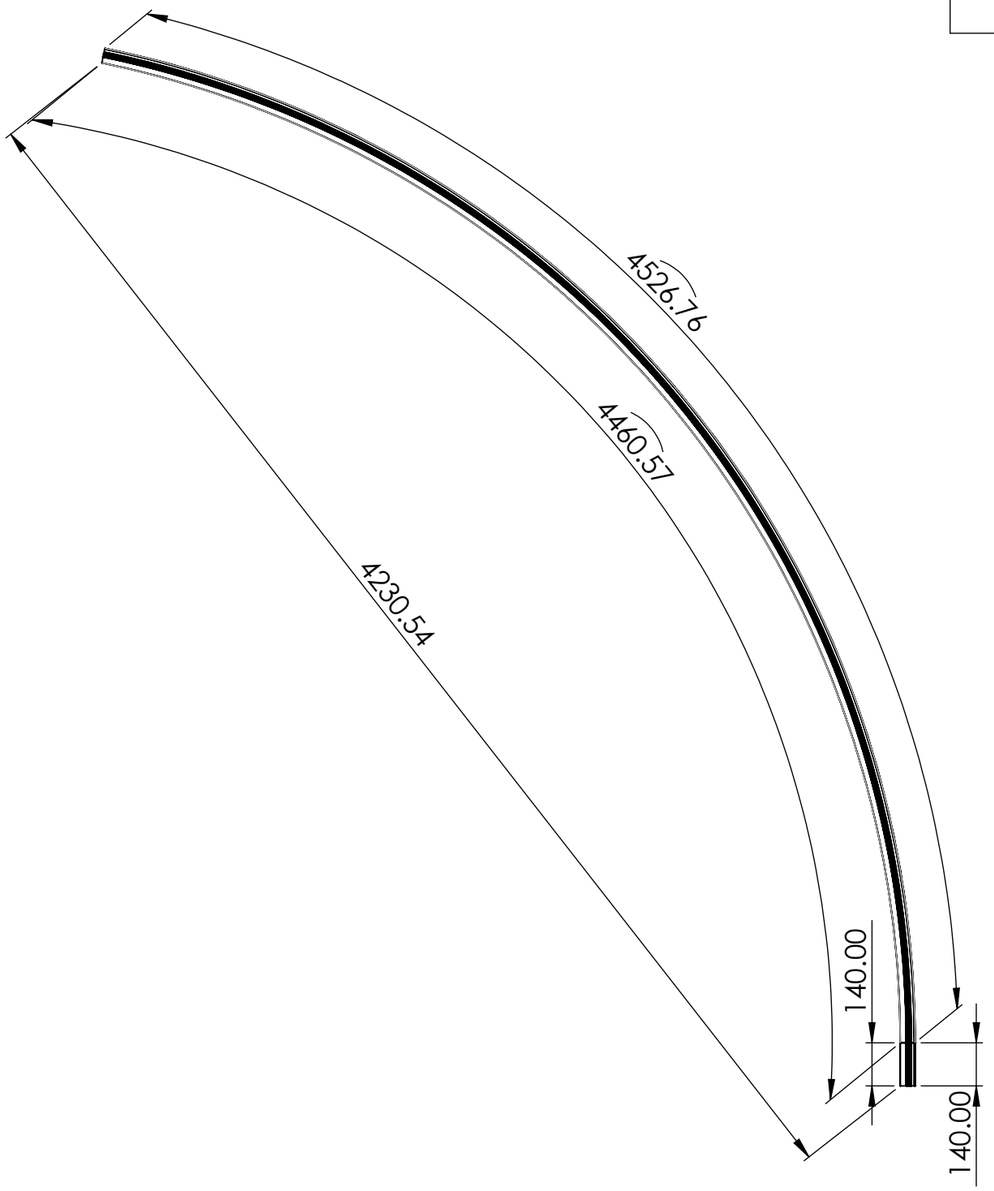


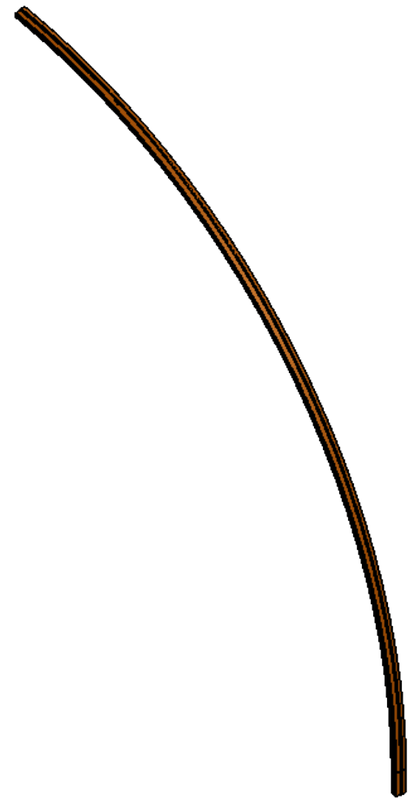


NOTE
VERTICAL SUPPORT PROFILE ABOVE BASE RING
USE PROFILE GNT-009

TITLE - ROOF AUTOMATION				NIHVA TECHNOLOGIES PVT.LTD.PUNE	
DWG NO - NTPL-278-PM-001-02-00-02				Website - www.nihva.com	
	NAME	SIGNATURE	DATE	PROJECT NO - NTPL-278-PM	
DRAWN	V.W		28-04-2025	PRODUCT - DOME	
CHK'D	S.W.		28-04-2025	SITE LOCATION - LONAVLA	
APPV'D	V.T.		28-04-2025		
if any queries contact - supportautomation@nihva.com				REVISION -	QTY - 1
ALL DIMENSION ARE IN mm			A3	SCALE	SHEET 4 OF 18

ITEM NO.	PART NUMBER	DESCRIPTION	QTY.
1	..REV03TOP RING SUPPORT	AL 6063_T4	2

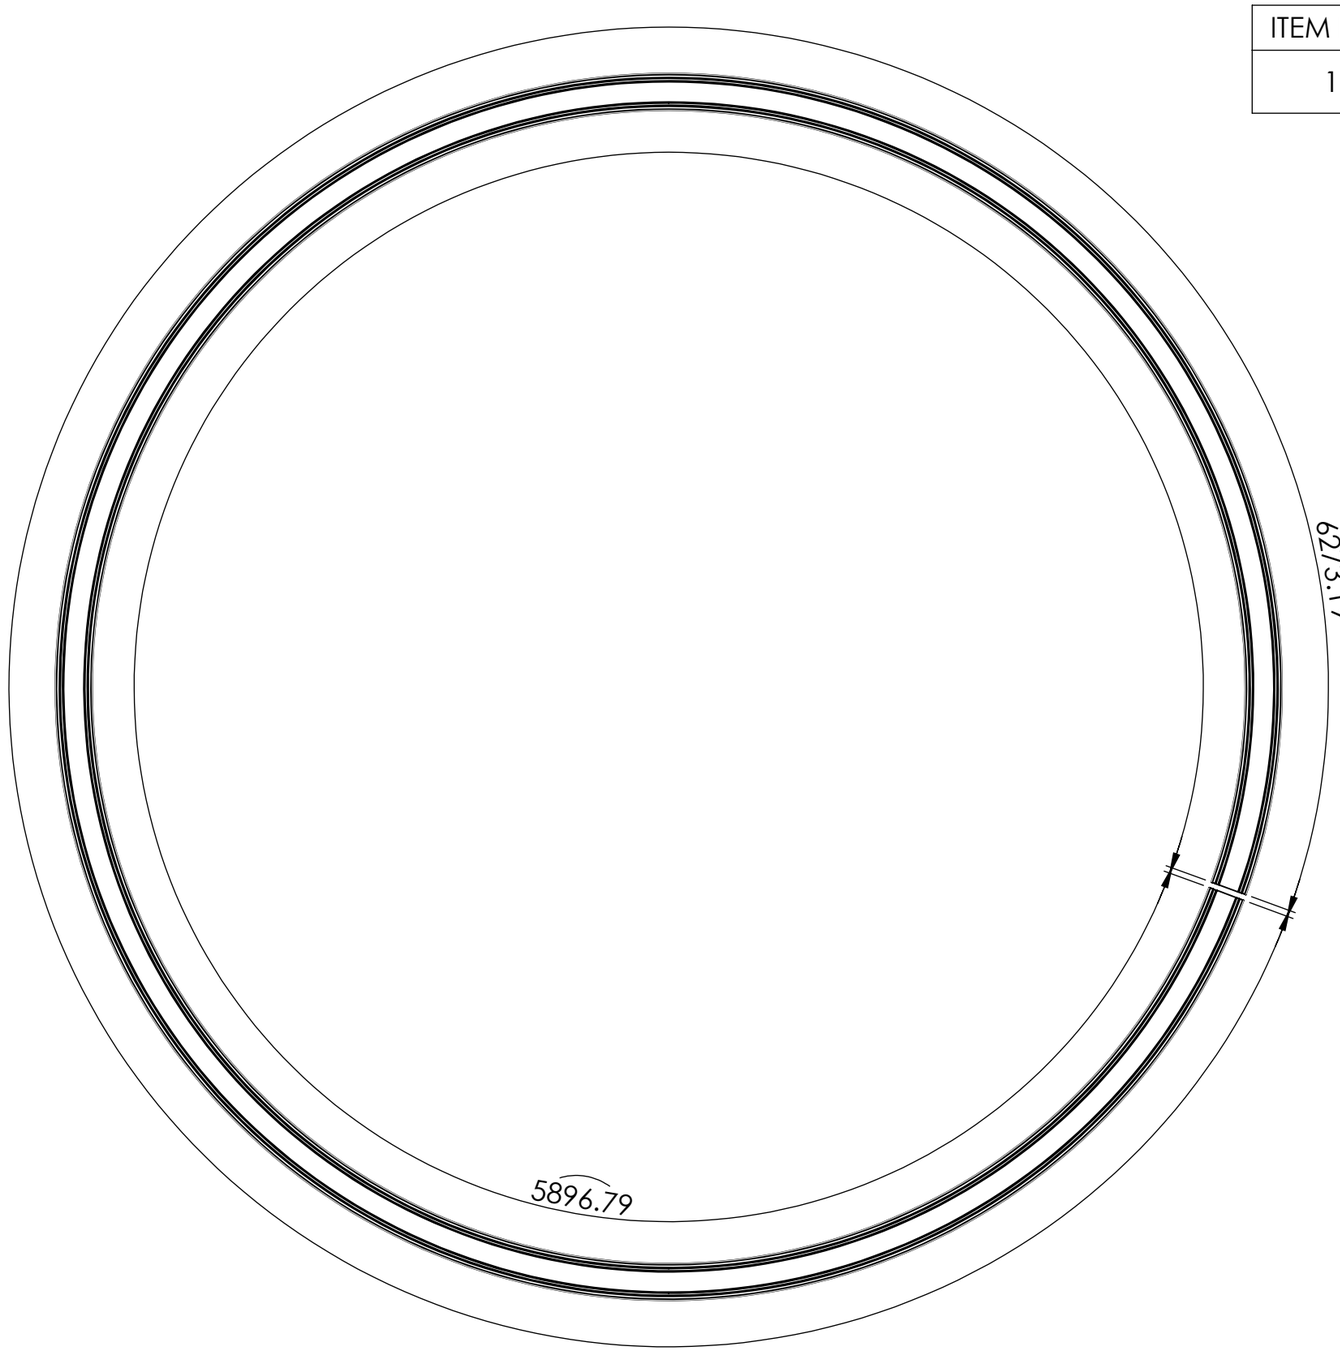


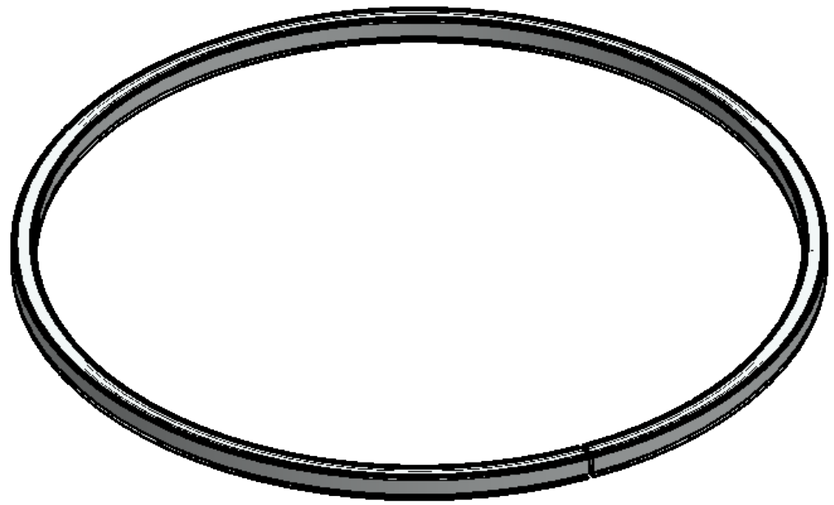


NOTE
TOP RING SUPPORT
USE PROFILE GNT-006

TITLE - ROOF AUTOMATION				NIHVA TECHNOLOGIES PVT.LTD.PUNE Website - www.nihva.com
DWG NO - NTPL-278-PM-001-03-00-03				
	NAME	SIGNATURE	DATE	PROJECT NO - NTPL-278-PM
DRAWN	V.W		28-04-2025	PRODUCT - DOME
CHK'D	S.W.		28-04-2025	SITE LOCATION - LONAVLA
APPV'D	V.T.		28-04-2025	
if any queries contact - supportautomation@nihva.com				REVISION - QTY - 1
ALL DIMENSION ARE IN mm		A3		SCALE SHEET 5 OF 18

ITEM NO.	PART NUMBER	DESCRIPTION	QTY.
1	..REV03VERTICAL SUPPORT ABOBE TOP RING 1	AL 6063_T4	8

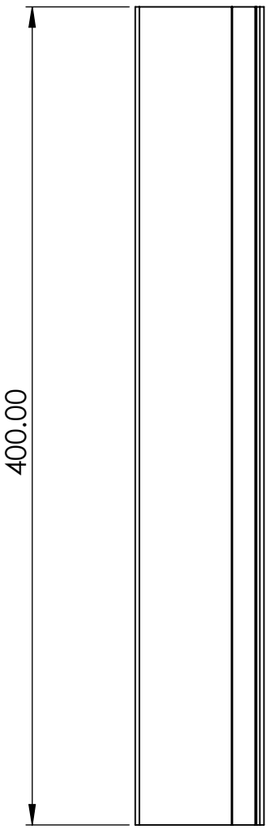


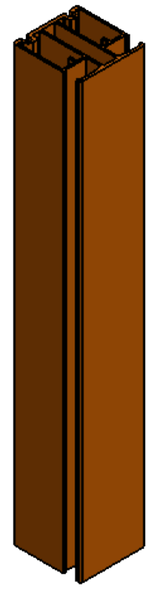


NOTE
VERTICAL SUPPORT ABOBE TOP RING 1
USE PROFILE GNT-006

TITLE - ROOF AUTOMATION				NIHVA TECHNOLOGIES PVT.LTD.PUNE
DWG NO - NTPL-278-PM-001-04-00-04				Website - www.nihva.com
	NAME	SIGNATURE	DATE	PROJECT NO - NTPL-278-PM
DRAWN	V.W		28-04-2025	PRODUCT - DOME
CHK'D	S.W.		28-04-2025	SITE LOCATION - LONAVLA
APPV'D	V.T.		28-04-2025	
if any queries contact - supportautomation@nihva.com				REVISION - QTY - 1
ALL DIMENSION ARE IN mm			A3	SCALE SHEET 6 OF 18

ITEM NO.	PART NUMBER	DESCRIPTION	QTY.
1	..REV03TOP VERTICAL SUPPORT 2	AL 6063_T4	8

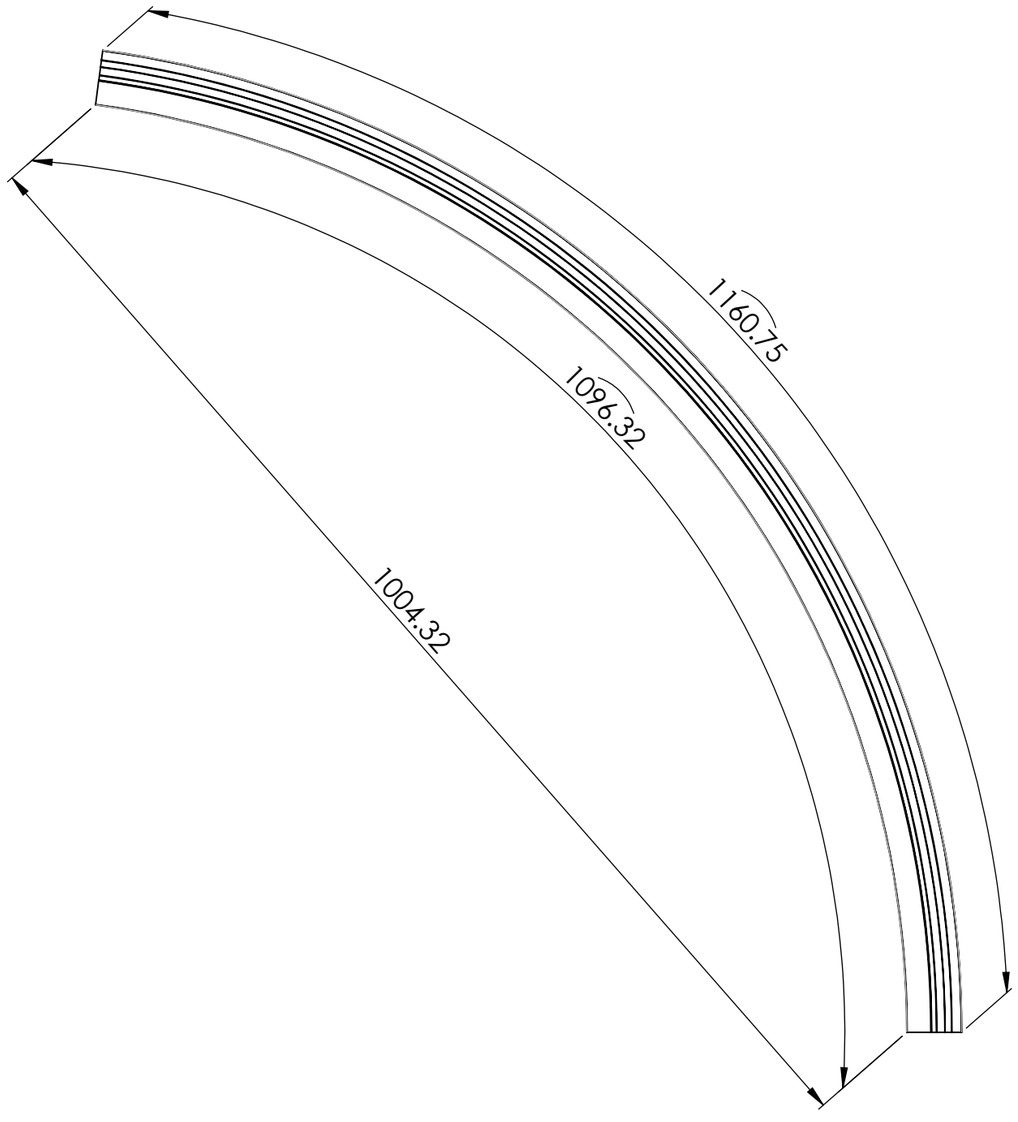


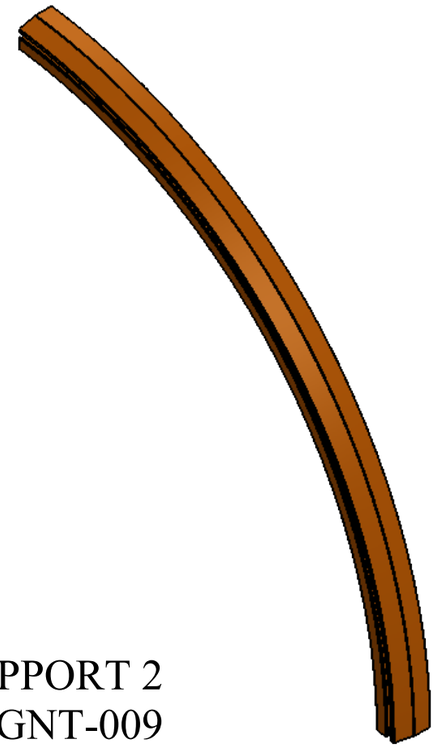


NOTE
VERTICAL SUPPORT 2
USE PROFILE GNT-009

TITLE - ROOF AUTOMATION				NIHVA TECHNOLOGIES PVT.LTD.PUNE
DWG NO - NTPL-278-PM-001-05-00-05				Website - www.nihva.com
	NAME	SIGNATURE	DATE	PROJECT NO - NTPL-278-PM
DRAWN	V.W		28-04-2025	PRODUCT - DOME
CHK'D	S.W.		28-04-2025	SITE LOCATION - LONAVLA
APPV'D	V.T.		28-04-2025	
if any queries contact - supportautomation@nihva.com				REVISION - QTY - 1
ALL DIMENSION ARE IN mm			A3	SCALE SHEET 7 OF 18

ITEM NO.	PART NUMBER	DESCRIPTION	QTY.
1	..REV03POLYGOANL SHAPE BY WELDIND	AL 6063_T4	1

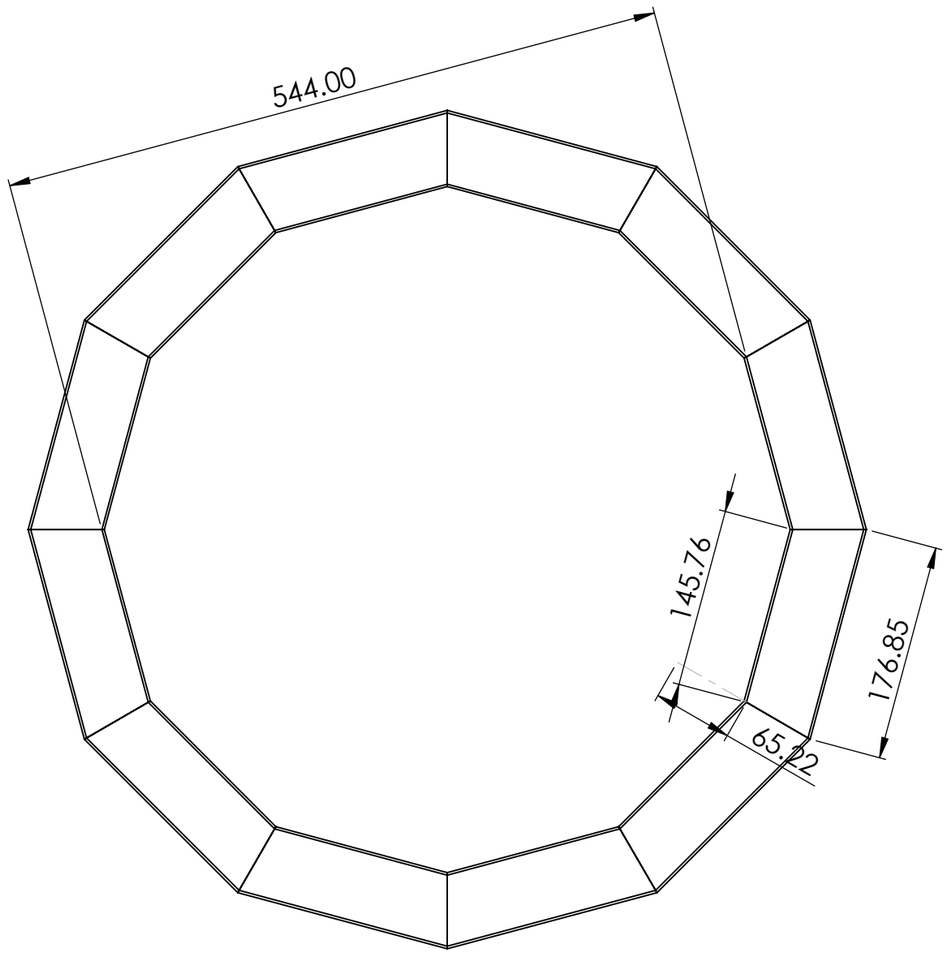


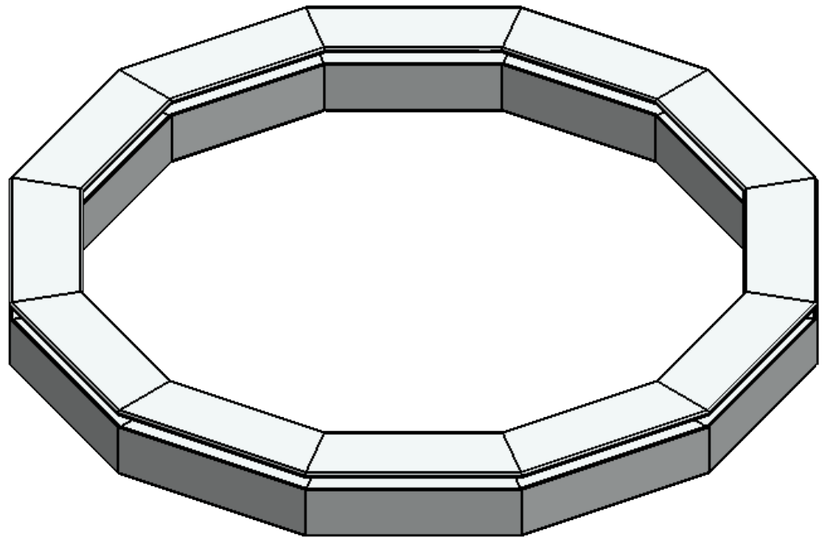


NOTE
POLYGONAL SHAPE BY WELDING
USE PROFILE GNT-006

TITLE - ROOF AUTOMATION				NIHVA Technologies Pvt. Ltd.	NIHVA TECHNOLOGIES PVT.LTD.PUNE Website - www.nihva.com
DWG NO - NTPL-278-PM-001-06-00-06					
	NAME	SIGNATURE	DATE	PROJECT NO - NTPL-278-PM	
DRAWN	V.W		28-04-2025	PRODUCT - DOME	
CHK'D	S.W.		28-04-2025	SITE LOCATION - LONAVLA	
APPV'D	V.T.		28-04-2025		
if any queries contact - supportautomation@nihva.com				REVISION -	QTY - 1
ALL DIMENSION ARE IN mm			A3	SCALE	SHEET 8 OF 18

ITEM NO.	PART NUMBER	DESCRIPTION	QTY.
1	T PLATE	SS304 -117.5X156X3 MM THK	40
2	..REV03VIJAY_Rivet_iso_15977_4_x_16_0	RIVET M4X16	10

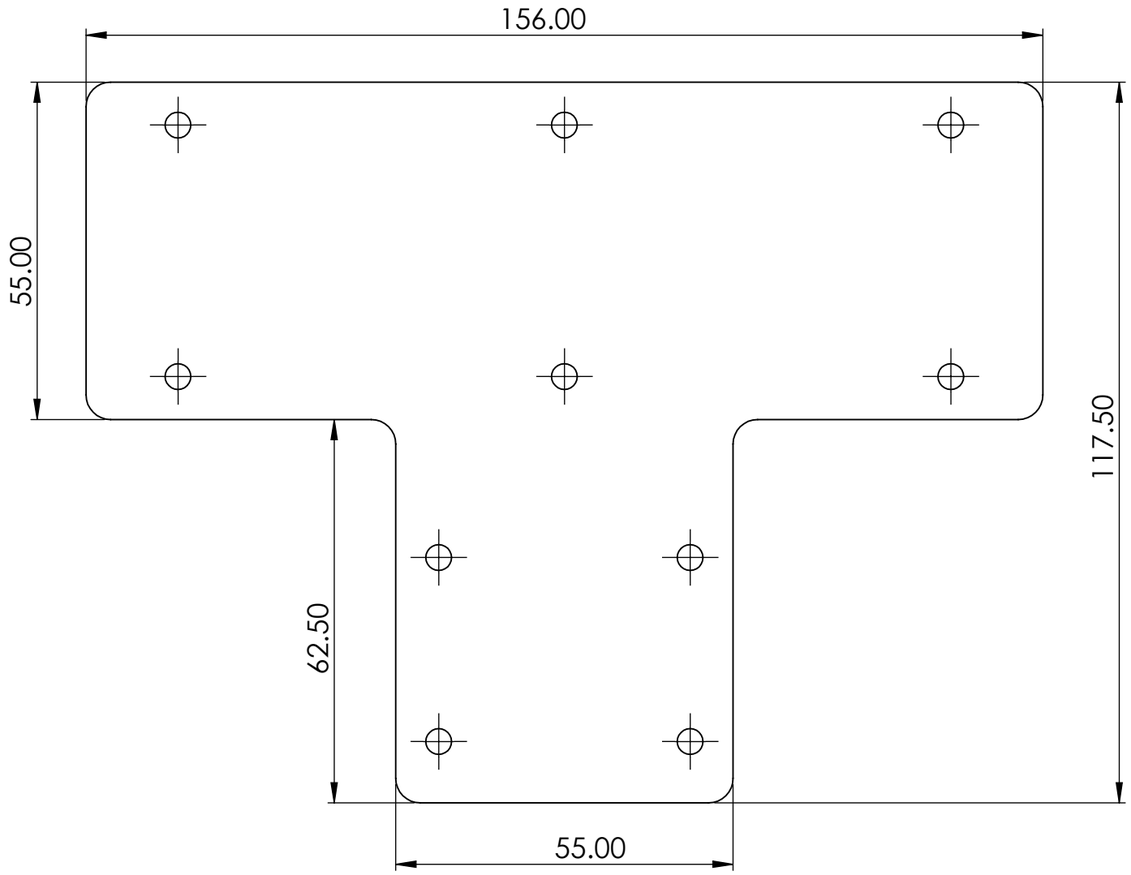


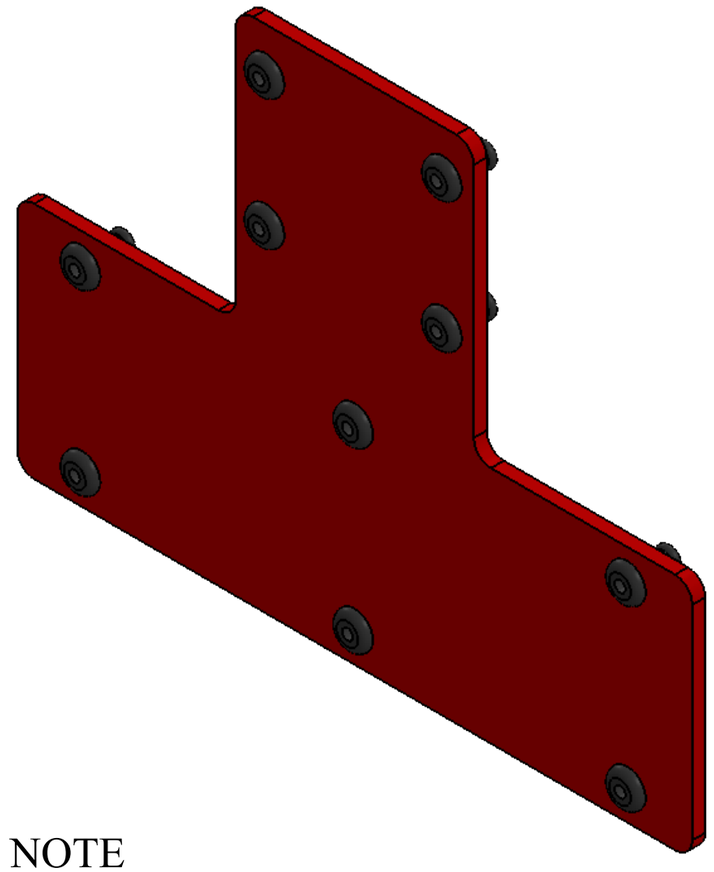



NOTE
T PLATE
LASER CUTTING

TITLE - ROOF AUTOMATION				NIHVA TECHNOLOGIES PVT.LTD.PUNE
DWG NO - NTPL-278-PM-001-09-00-09				Website - www.nihva.com
	NAME	SIGNATURE	DATE	PROJECT NO - NTPL-278-PM
DRAWN	V.W		28-04-2025	PRODUCT - DOME
CHK'D	S.W.		28-04-2025	SITE LOCATION - LONAVLA
APPV'D	V.T.		28-04-2025	
if any queries contact - supportautomation@nihva.com				REVISION - QTY - 1
ALL DIMENSION ARE IN mm		A3		SCALE SHEET 9 OF 18

ITEM NO.	PART NUMBER	DESCRIPTION	QTY.
1	..REV03New Upper Plus bend plate	SS 304 - 197.14*156*3MM THK	8
2	..REV03VIJAY_Rivet_iso_15977_4_x_16_0	RIVET M4X16	14

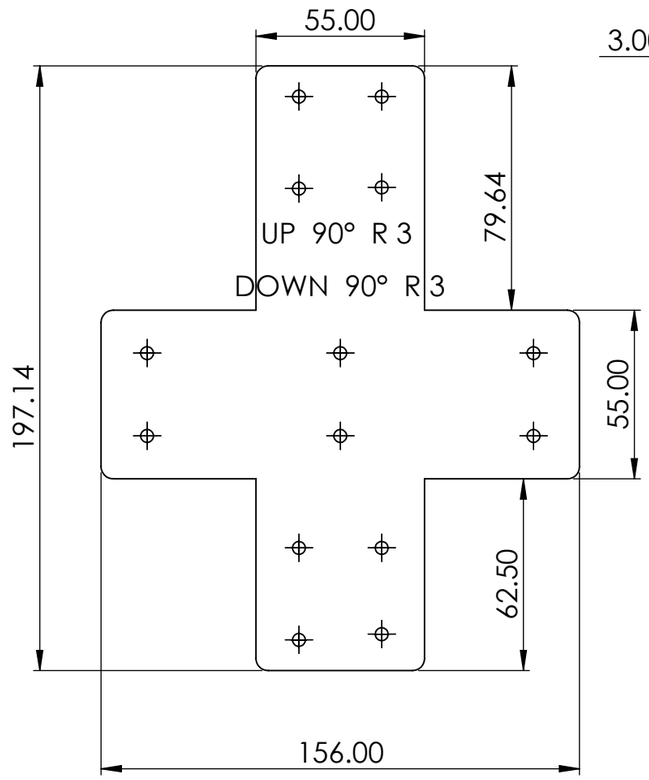

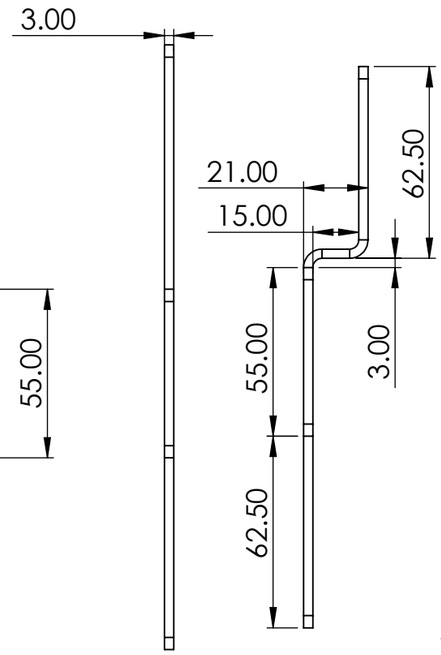


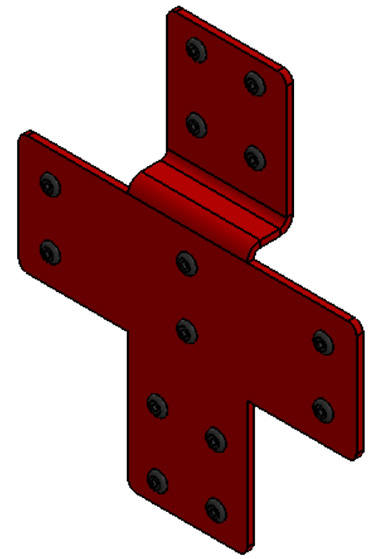


NOTE
NEW UPPER PLUS BEND PLATE
LASER CUTTING

TITLE - ROOF AUTOMATION				NIHVA TECHNOLOGIES PVT.LTD.PUNE
DWG NO - NTPL-278-PM-001-10-00-10				Website - www.nihva.com
	NAME	SIGNATURE	DATE	PROJECT NO - NTPL-278-PM
DRAWN	V.W		28-04-2025	PRODUCT - DOME
CHK'D	S.W.		28-04-2025	SITE LOCATION - DOME
APPV'D	V.T.		28-04-2025	
if any queries contact - supportautomation@nihva.com				REVISION - QTY - 1
ALL DIMENSION ARE IN mm		A3		SCALE SHEET 10 OF 18

ITEM NO.	PART NUMBER	DESCRIPTION	QTY.
1	..REV03REV 02New Bottom Bend Joining Plate	SS 304 - 138.64*156*3MM THK	20
2	..REV03REV 02VIJAY_Rivet_iso_15977_4_x_16_0	RIVET M4X16	10

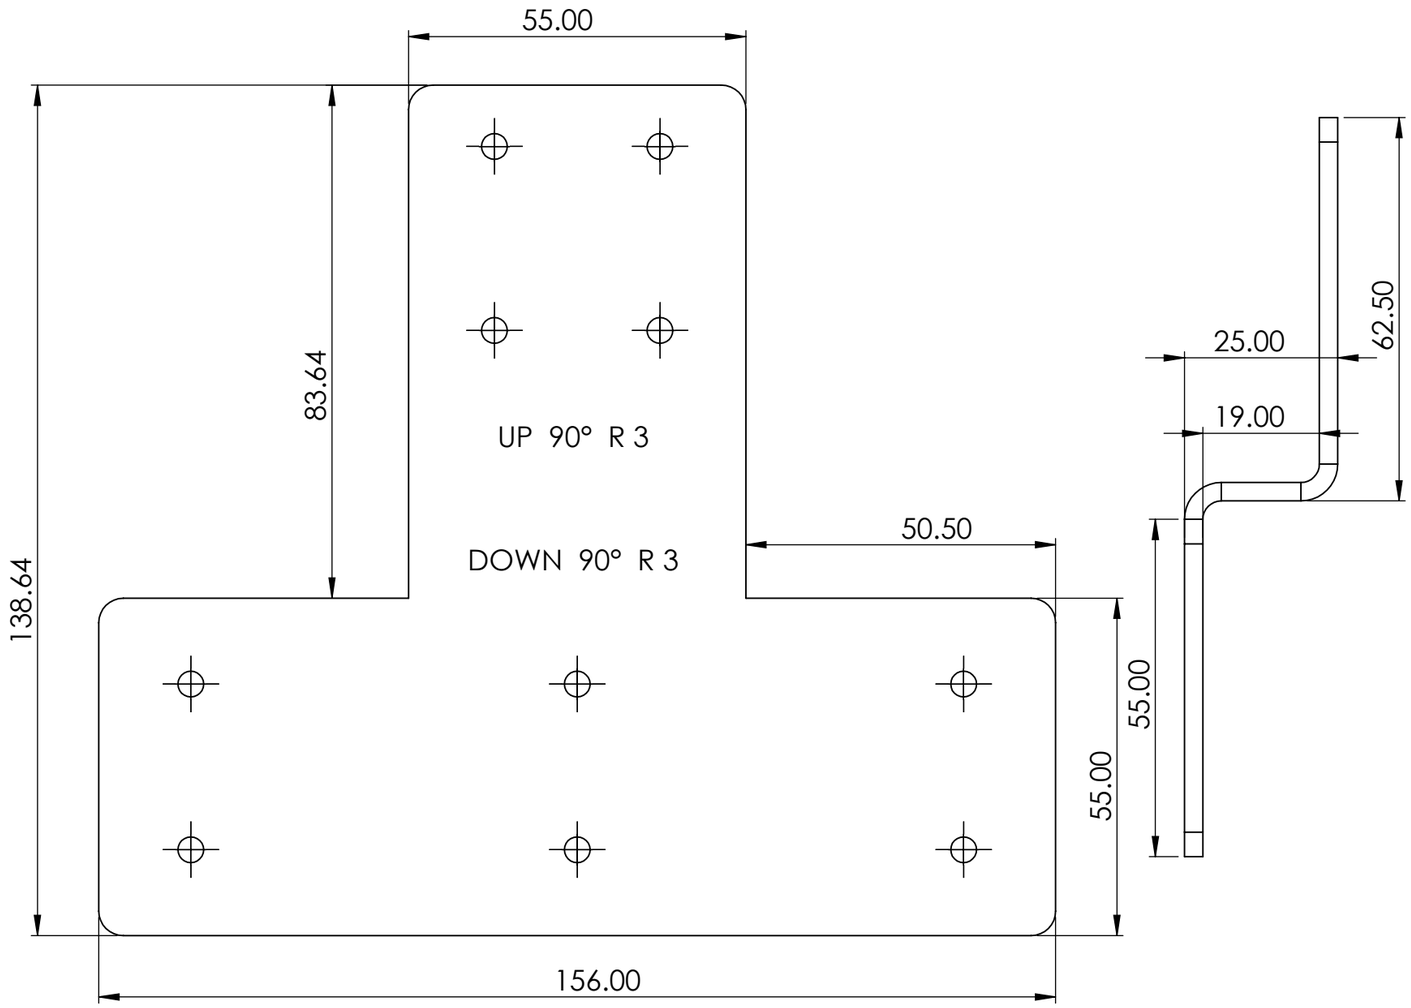


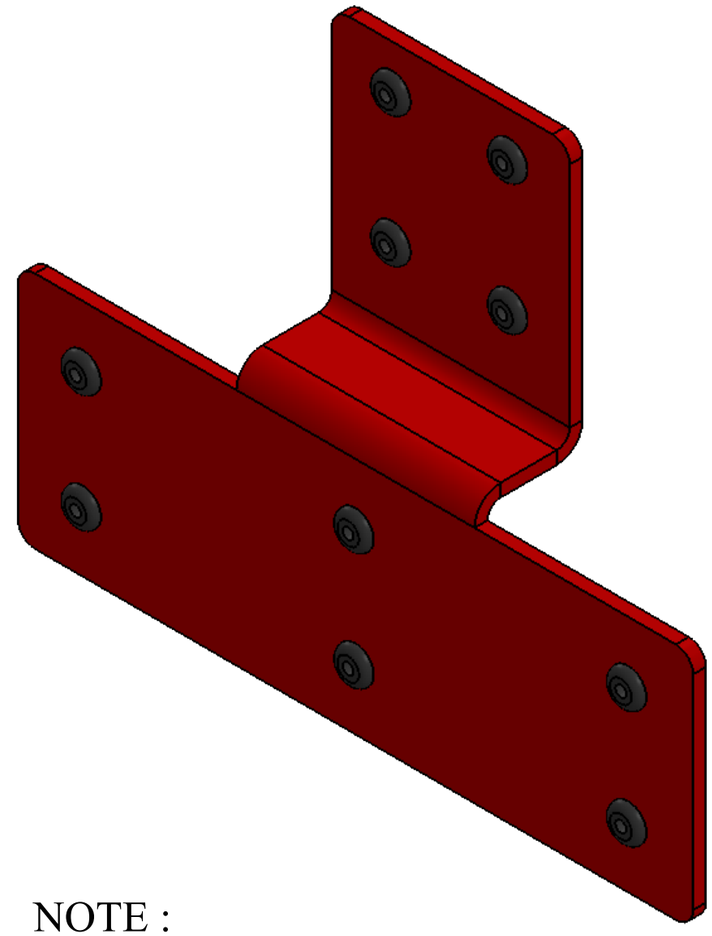


NOTE :
NEW BOTTOM BEND JOINING PLATE
LASER CUTTING

TITLE - ROOF AUTOMATION				NIHVA TECHNOLOGIES PVT.LTD.PUNE Website - www.nihva.com
DWG NO - NTPL-278-PM-001-11-00-11				
	NAME	SIGNATURE	DATE	PROJECT NO - NTPL-278-PM
DRAWN	V.W		28-04-2025	PRODUCT - DOME
CHK'D	S.W.		28-04-2025	SITE LOCATION - LONAVLA
APPV'D	V.T.		28-04-2025	
if any queries contact - supportautomation@nihva.com				REVISION - QTY - 1
ALL DIMENSION ARE IN mm		A3		SCALE SHEET 11 OF 18

ITEM NO.	PART NUMBER	DESCRIPTION	QTY.
1	..REV03NEW PIUS PALTE	SS 304 - 180*156*3MM THK	8
2	..REV03VIJAY_Rivet_iso_15977_4_x_16_0	RIVET M4X16	14

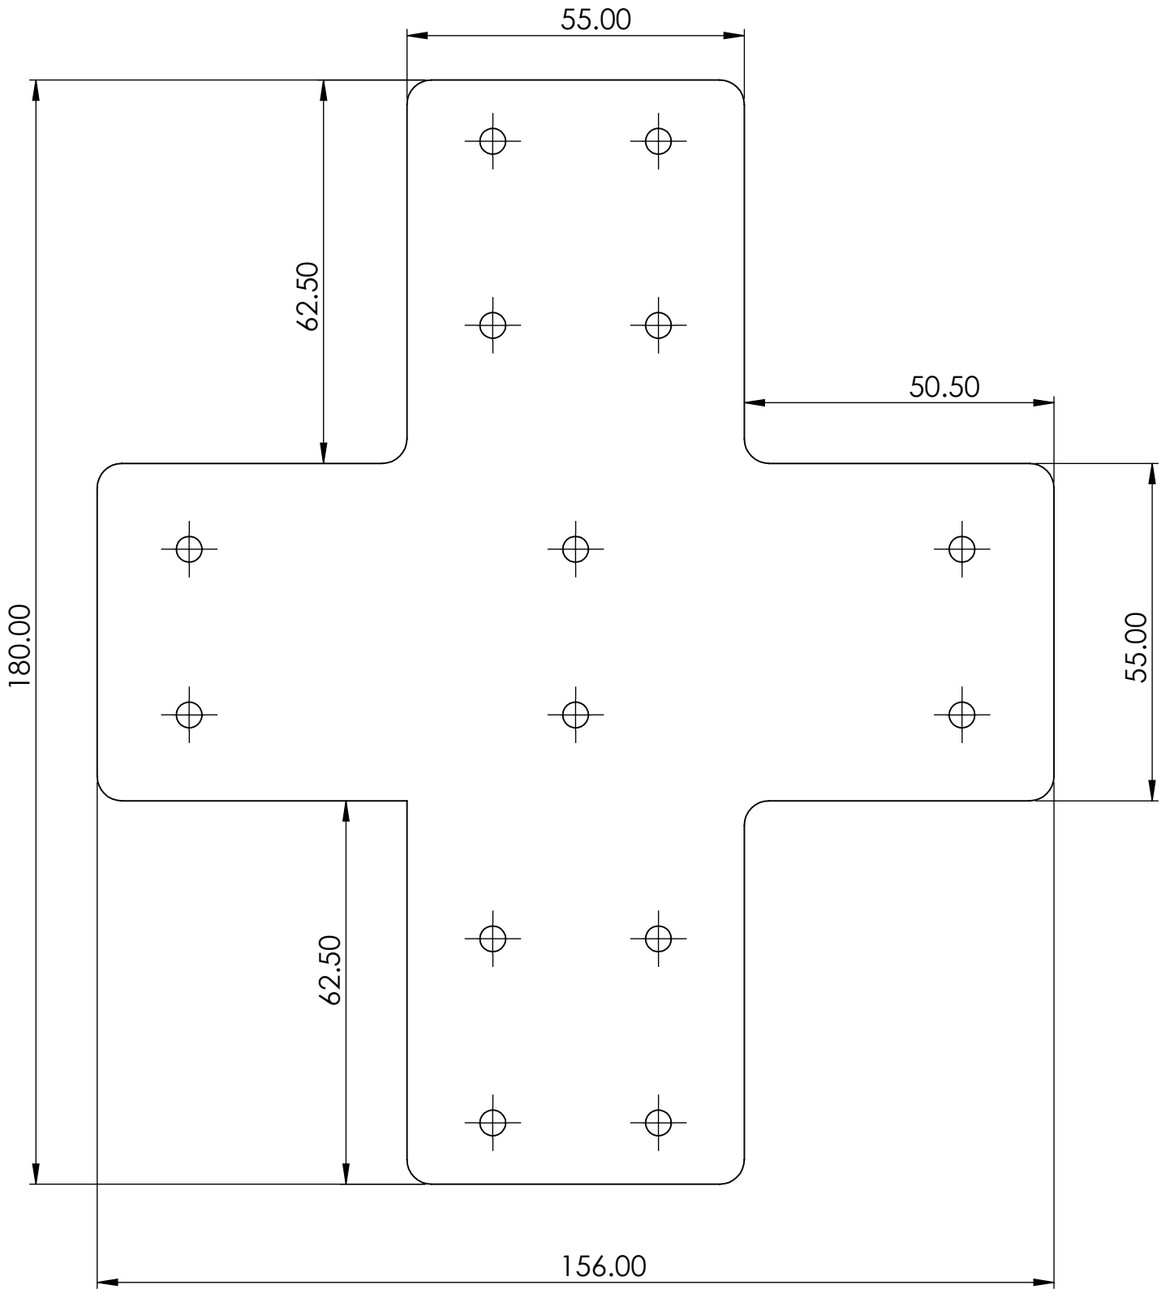


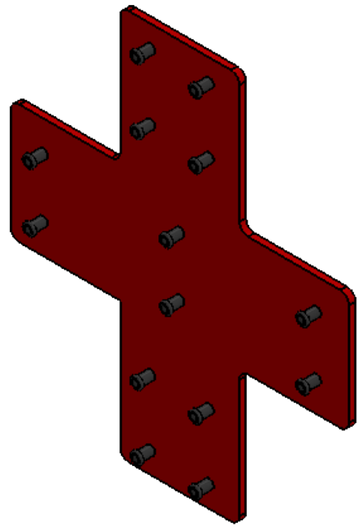



NOTE
NEW PLUS PLATE
LASER CUTTING

TITLE - ROOF AUTOMATION				NIHVA Technologies Pvt. Ltd.	NIHVA TECHNOLOGIES PVT.LTD.PUNE Website - www.nihva.com
DWG NO - NTPL-278-PM-001-12-00-12					
	NAME	SIGNATURE	DATE	PROJECT NO - NTPL-278-PM	
DRAWN	V.W		28-04-2025	PRODUCT - DOME	
CHK'D	S.W.		28-04-2025	SITE LOCATION - LONAVLA	
APPV'D	V.T.		28-04-2025		
if any queries contact - supportautomation@nihva.com				REVISION -	QTY - 1
ALL DIMENSION ARE IN mm		A3		SCALE	SHEET 12 OF 18

ITEM NO.	PART NUMBER	DESCRIPTION	QTY.
1	..REV03REV 01New UPPER BEND VERTICAL SUPPORT Joining Plate	SS 304 - 135.64*156*3MM THK	8
2	..REV03REV 01VIJAY_Rivet_iso_15977_4_x_16_0	RIVET M4X16	10

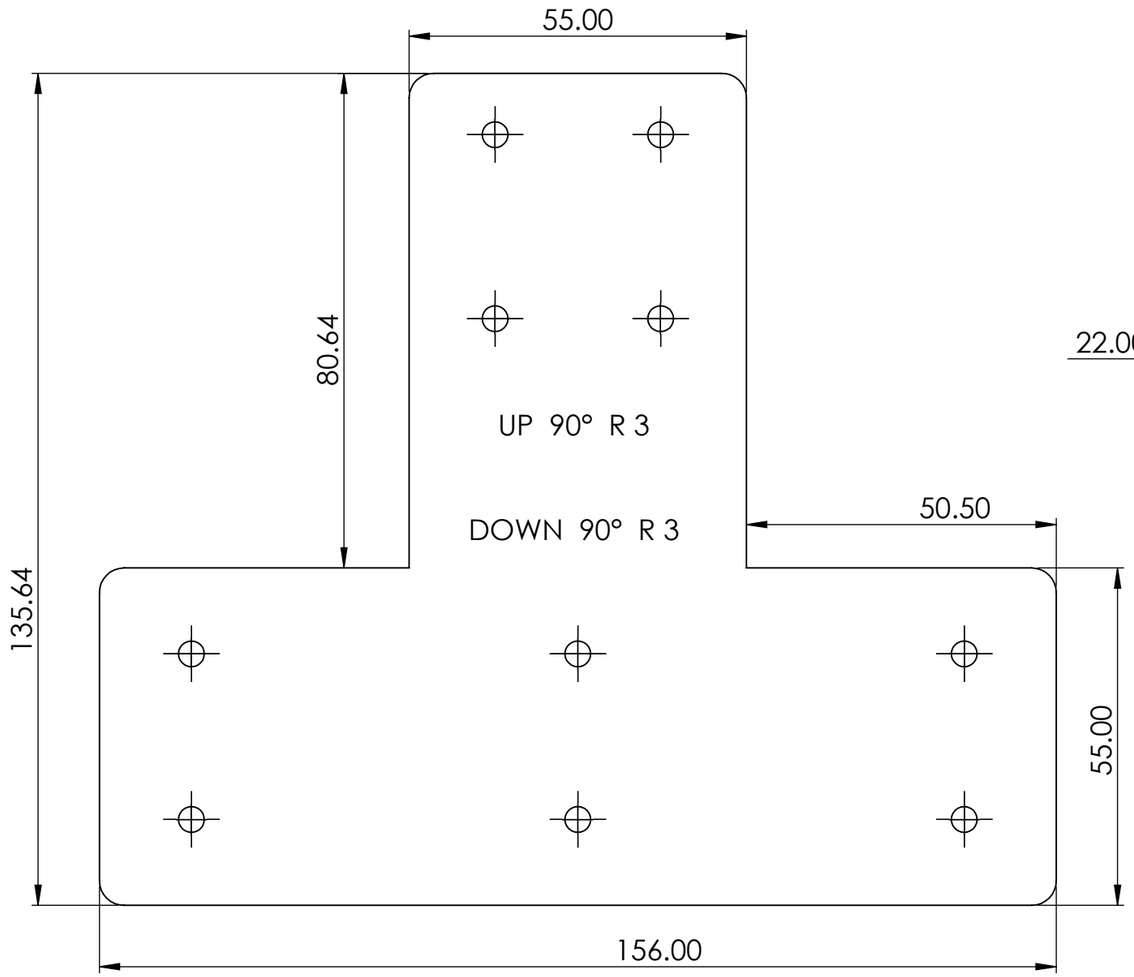

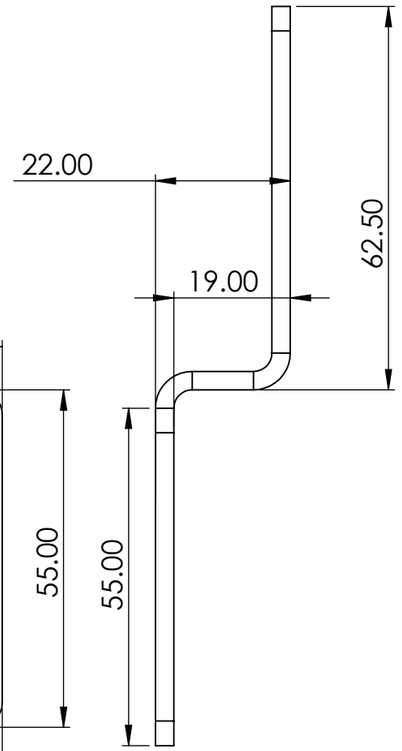


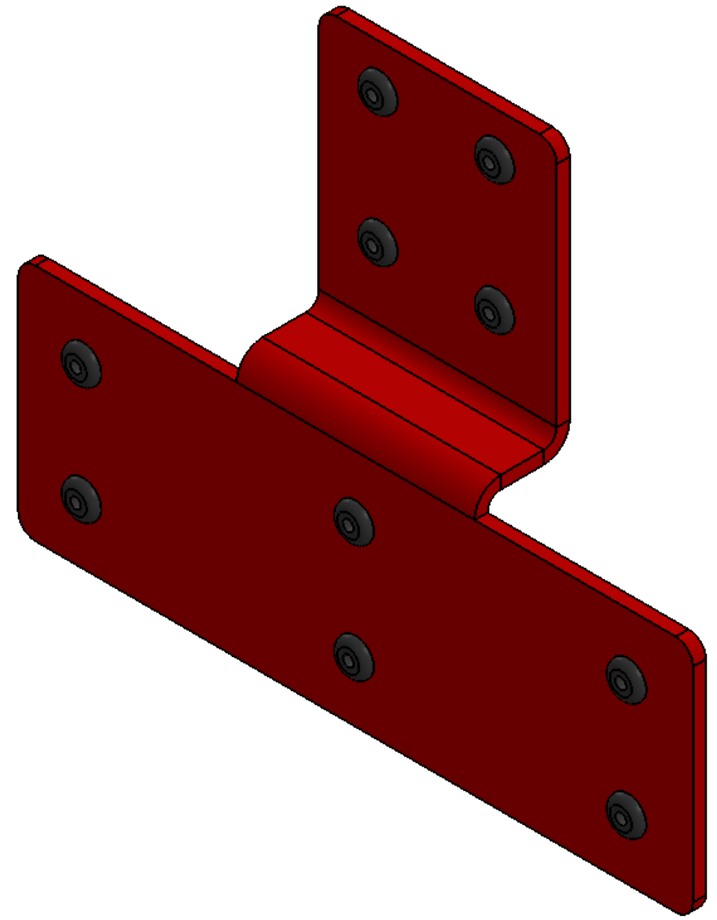



NOTE
NEW UPPER BEND VERTICAL SUPPORT JOINING PLATE
LASER CUTTING

TITLE - ROOF AUTOMATION				NIHVA TECHNOLOGIES PVT.LTD.PUNE
DWG NO - NTPL-278-PM-001-13-00-13				Website - www.nihva.com
	NAME	SIGNATURE	DATE	PROJECT NO - NTPL-278-PM
DRAWN	V.W		28-04-2025	PRODUCT - DOME
CHK'D	S.W.		28-04-2025	SITE LOCATION - LONAVLA
APPV'D	V.T.		28-04-2025	
if any queries contact - supportautomation@nihva.com				REVISION - QTY - 1
ALL DIMENSION ARE IN mm		A3		SCALE SHEET 13 OF 18

ITEM NO.	PART NUMBER	DESCRIPTION	QTY.
1	..REV03REV 02New UPPER Bend VERTICAL SUPPORT ABOVE BASE RING Joining Plate	SS 304 - 138.64*156*3MM THK	20
		Sheet	1

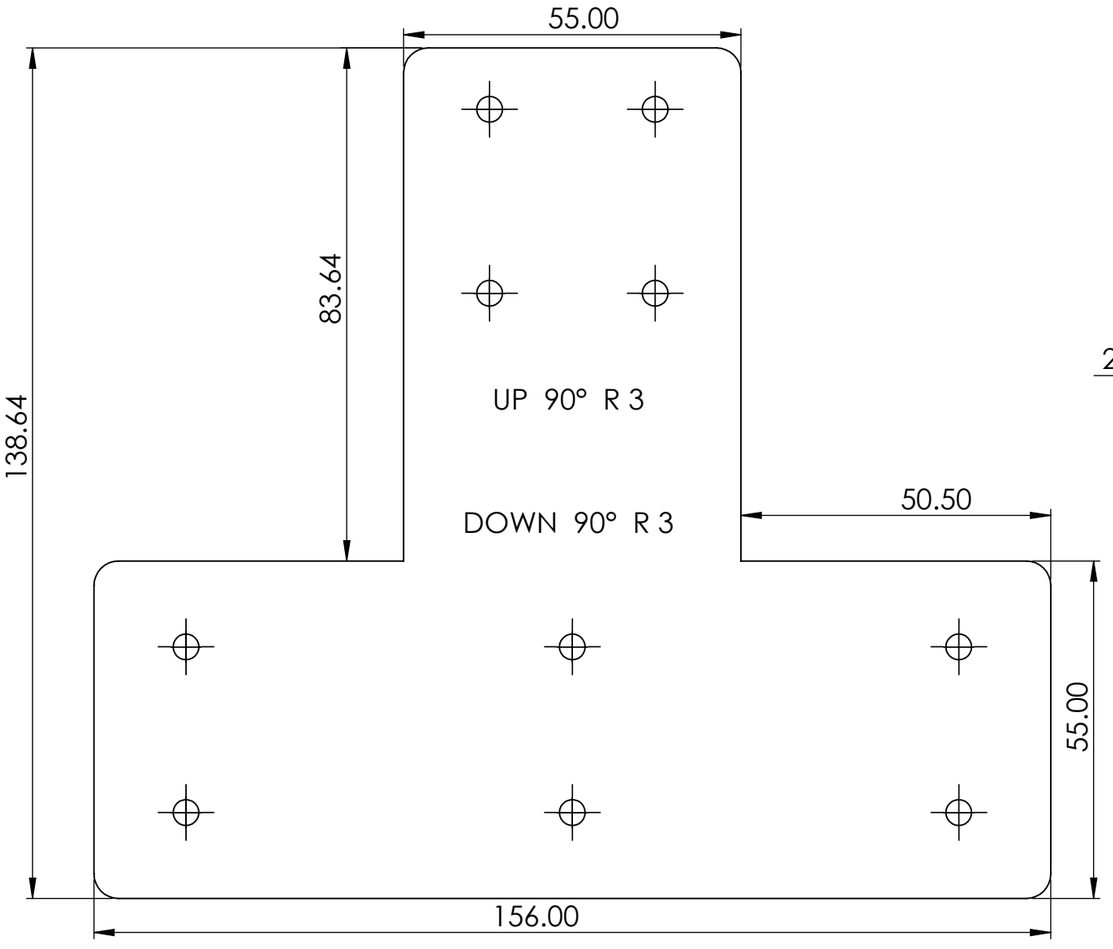

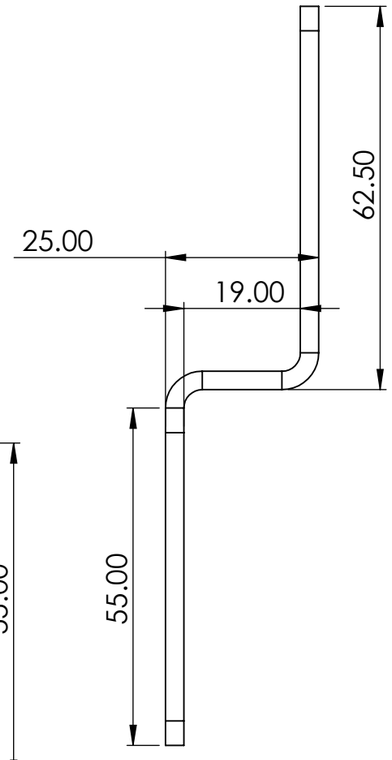


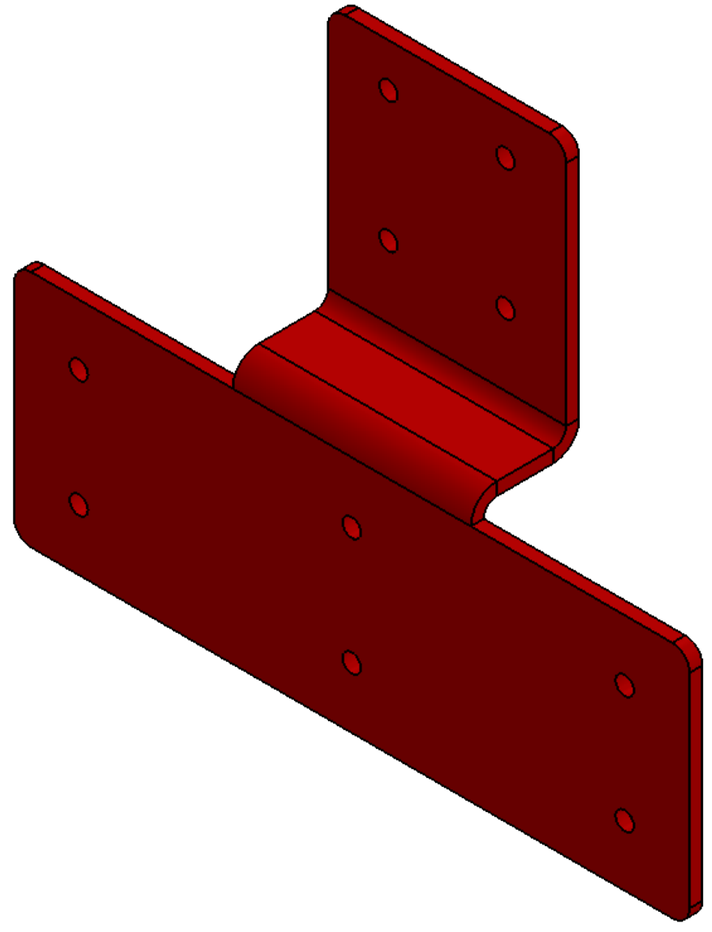


NOTE
NEW UPPER BEND VERTICAL SUPPORT ABOVE BASE RING
JOINING PLATE
LASER CUTTING

TITLE - ROOF AUTOMATION				NIHVA TECHNOLOGIES PVT.LTD.PUNE
DWG NO - NTPL-278-PM-001-16-00-16				Website - www.nihva.com
	NAME	SIGNATURE	DATE	PROJECT NO - NTPL-278-PM
DRAWN	V.W		28-04-2025	PRODUCT - DOME
CHK'D	S.W.		28-04-2025	SITE LOCATION - LONAVLA
APPV'D	V.T.		28-04-2025	
if any queries contact - supportautomation@nihva.com				REVISION - QTY - 1
ALL DIMENSION ARE IN mm			A3	SCALE SHEET 14 OF 18

ITEM NO.	PART NUMBER	DESCRIPTION	QTY.
1	..HEXAGONAL SAHPE MS 60*30*1.5MM THK	MS	1

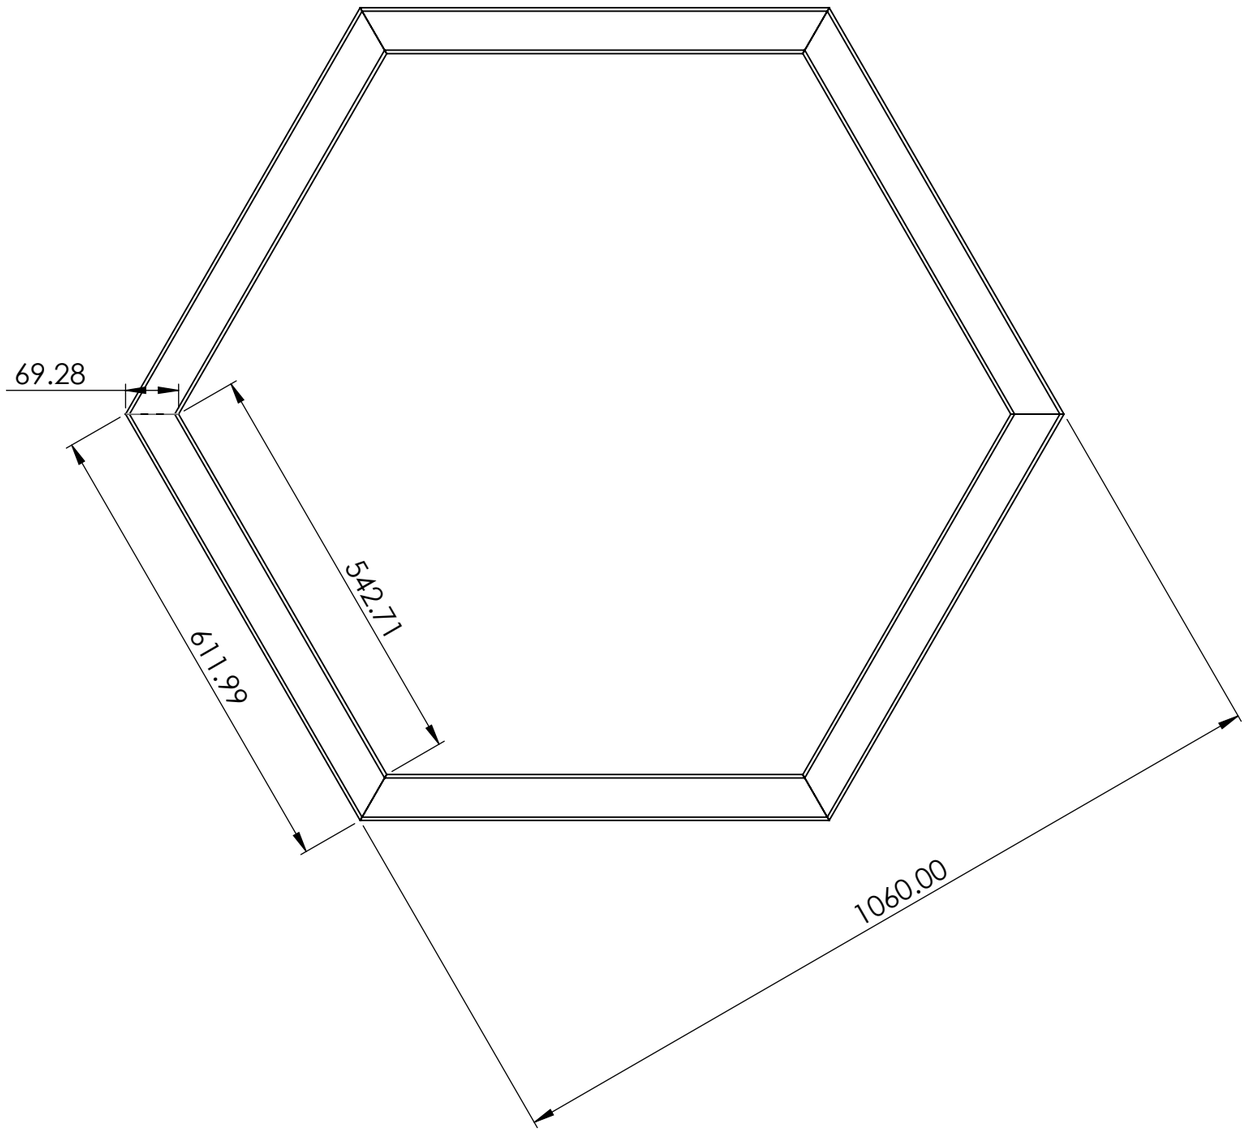


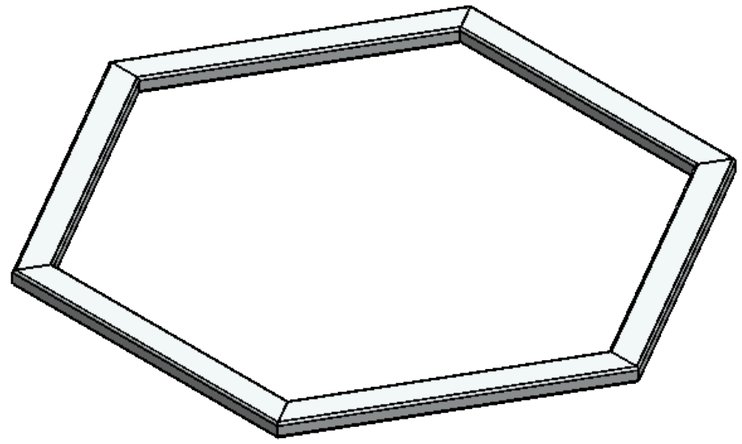


NOTE
HEXAGONAL SHAPE BY WELDIND
MS - 60*30*1.5MM THK

TITLE -ROOF AUTOMATION				NIHVA TECHNOLOGIES PVT.LTD.PUNE
DWG NO - NTPL-278-PM-001-18-00-18				Website - www.nihva.com
	NAME	SIGNATURE	DATE	PROJECT NO - NTPL-278-PM
DRAWN	V.W		28-04-2025	PRODUCT - DOME
CHK'D	S.W.		28-04-2025	SITE LOCATION - LONAVLA
APPV'D	V.T.		28-04-2025	
if any queries contact - supportautomation@nihva.com				REVISION - QTY - 1
ALL DIMENSION ARE IN mm			A3	SCALE SHEET 15 OF 18


ITEM NO.	PART NUMBER	DESCRIPTION	QTY.
1	..VERTICAL TUBE FOR CAP SHAPE SUPPORT MS 60*30*1.5MM THK	MS	6

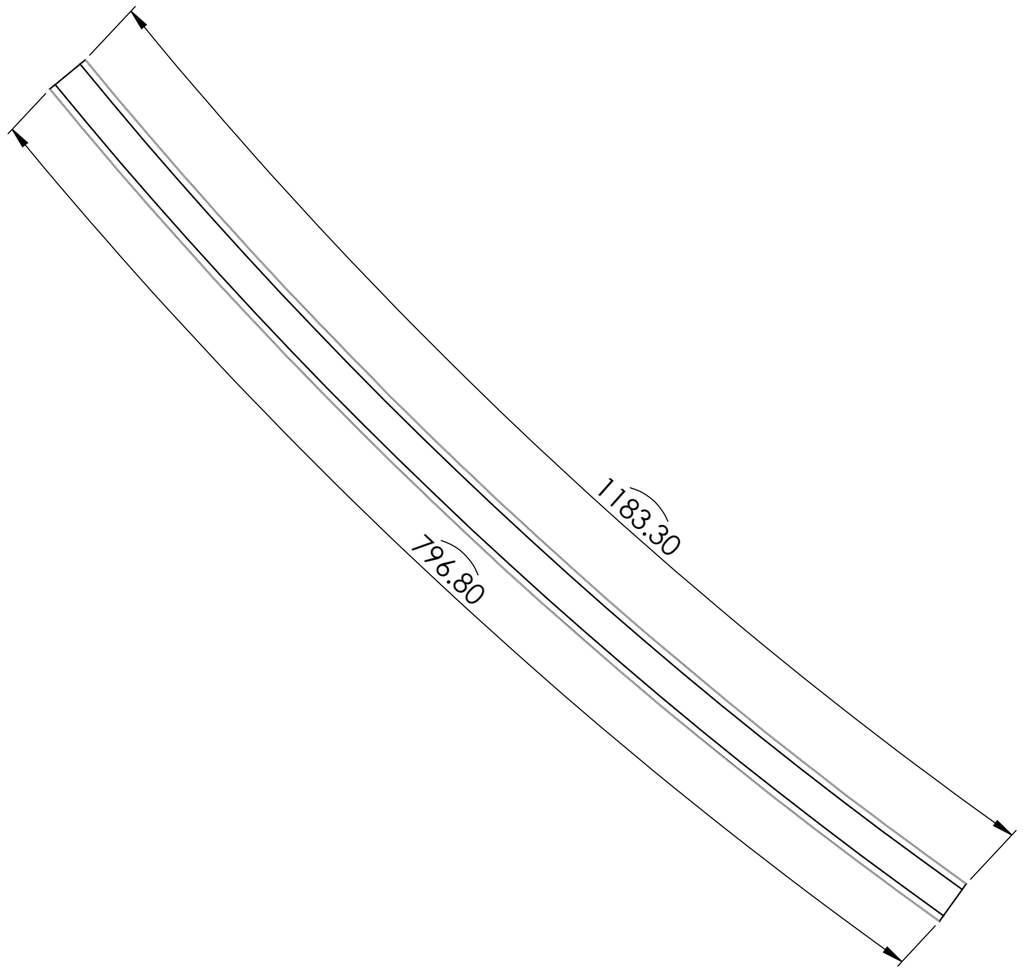


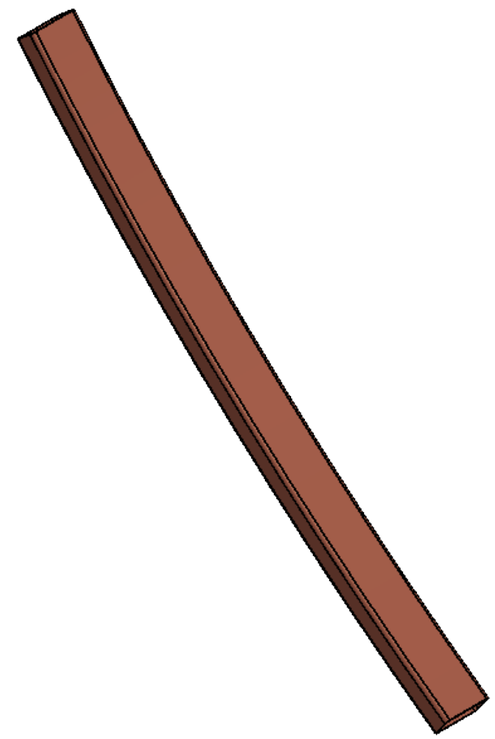


NOTE
CAP VERTICAL SUPPORT SQ TUBE
MS - 60*30*1.5M THK

TITLE - ROOF AUTOMATION				NIHVA TECHNOLOGIES PVT.LTD.PUNE
DWG NO - NTPL-278-PM-001-19-00-19				Website - www.nihva.com
	NAME	SIGNATURE	DATE	PROJECT NO - NTPL-278-PM
DRAWN	V.W		28-04-2025	PRODUCT - DOME
CHK'D	S.W.		28-04-2025	SITE LOCATION - LONAVLA
APPV'D	V.T.		28-04-2025	
if any queries contact - supportautomation@nihva.com				REVISION - QTY - 1
ALL DIMENSION ARE IN mm		A3		SCALE SHEET 16 OF 18

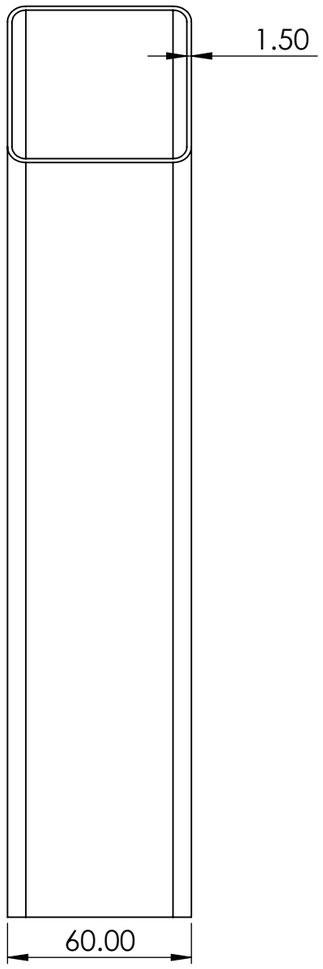

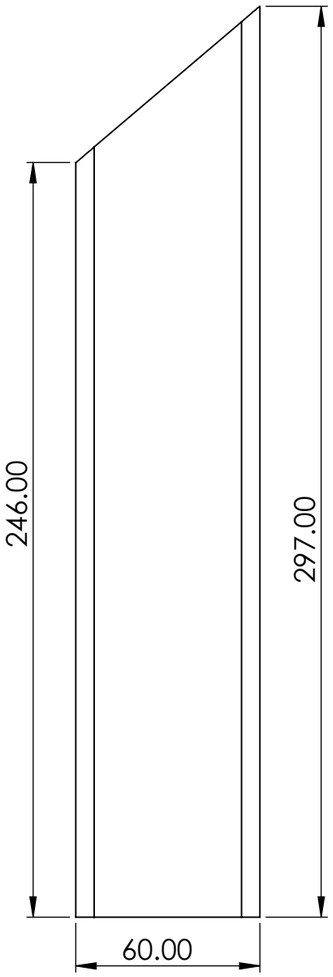


ITEM NO.	PART NUMBER	DESCRIPTION	QTY.
1	..VERTICAL TUBE FOR CAP SHAPE SUPPORT MS-60*30*1.5MM THK	MS	6
		TUBE, SQUARE 60.000000 X 60.000000 X 1.500000	1

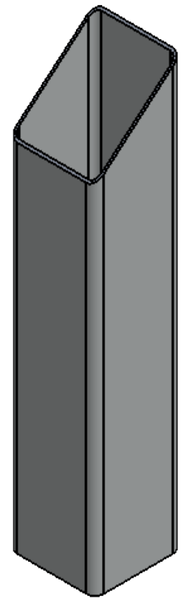



NOTE
VERTICAL TIBE CAP SUPPORT
MS -60*60*1.5MM THK

TITLE - ROOF AUTOMATIOM				NIHVA TECHNOLOGIES PVT.LTD.PUNE
DWG NO - NTPL-278-PM-001-20-00-20				Website - www.nihva.com
	NAME	SIGNATURE	DATE	PROJECT NO - NTPL-278-PM
DRAWN	V.W		28-04-2025	PRODUCT - DOME
CHK'D	S.W.		28-04-2025	SITE LOCATION - LONAVLA
APPV'D	V.T.		28-04-2025	
if any queries contact - supportautomation@nihva.com				REVISION - QTY - 1
ALL DIMENSION ARE IN mm		A3		SCALE SHEET 17 OF 18

ITEM NO.	PART NUMBER	DESCRIPTION	QTY.
1	..MESH	MS	1
		Sheet	1

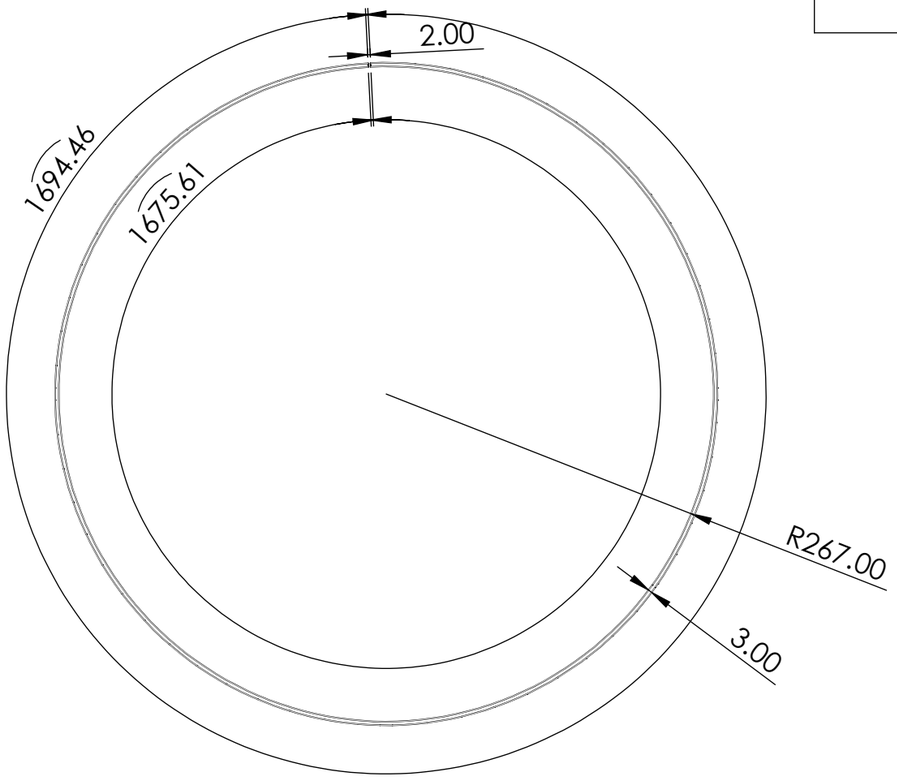

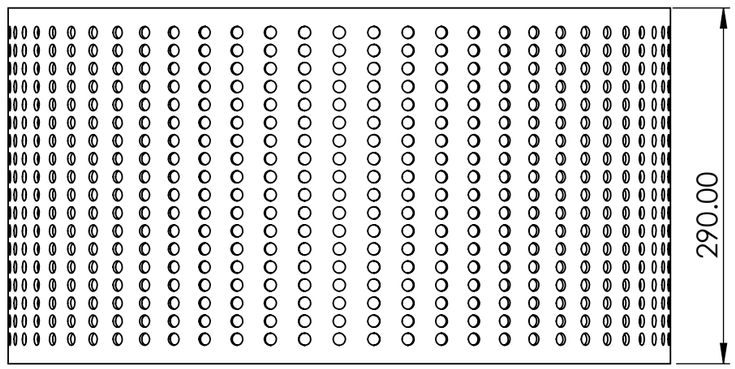

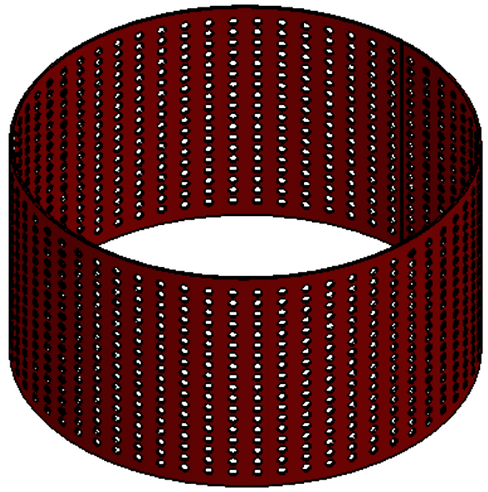

NOTE
MESH
THIS MESH IS PROVIDED FOR VENTIALTION

TITLE - ROOF AUTOMATION				NIHVA TECHNOLOGIES PVT.LTD.PUNE
DWG NO - NTPL-278-PM-001-21-00-21				Website - www.nihva.com
	NAME	SIGNATURE	DATE	PROJECT NO - NTPL-278-PM
DRAWN	V.W		28-04-2025	PRODUCT - DOME
CHK'D	S.W.		28-04-2025	SITE LOCATION - LONAVLA
APPV'D	V.T.		28-04-2025	
if any queries contact - supportautomation@nihva.com				REVISION - QTY - 1
ALL DIMENSION ARE IN mm		A3		SCALE SHEET 18 OF 18