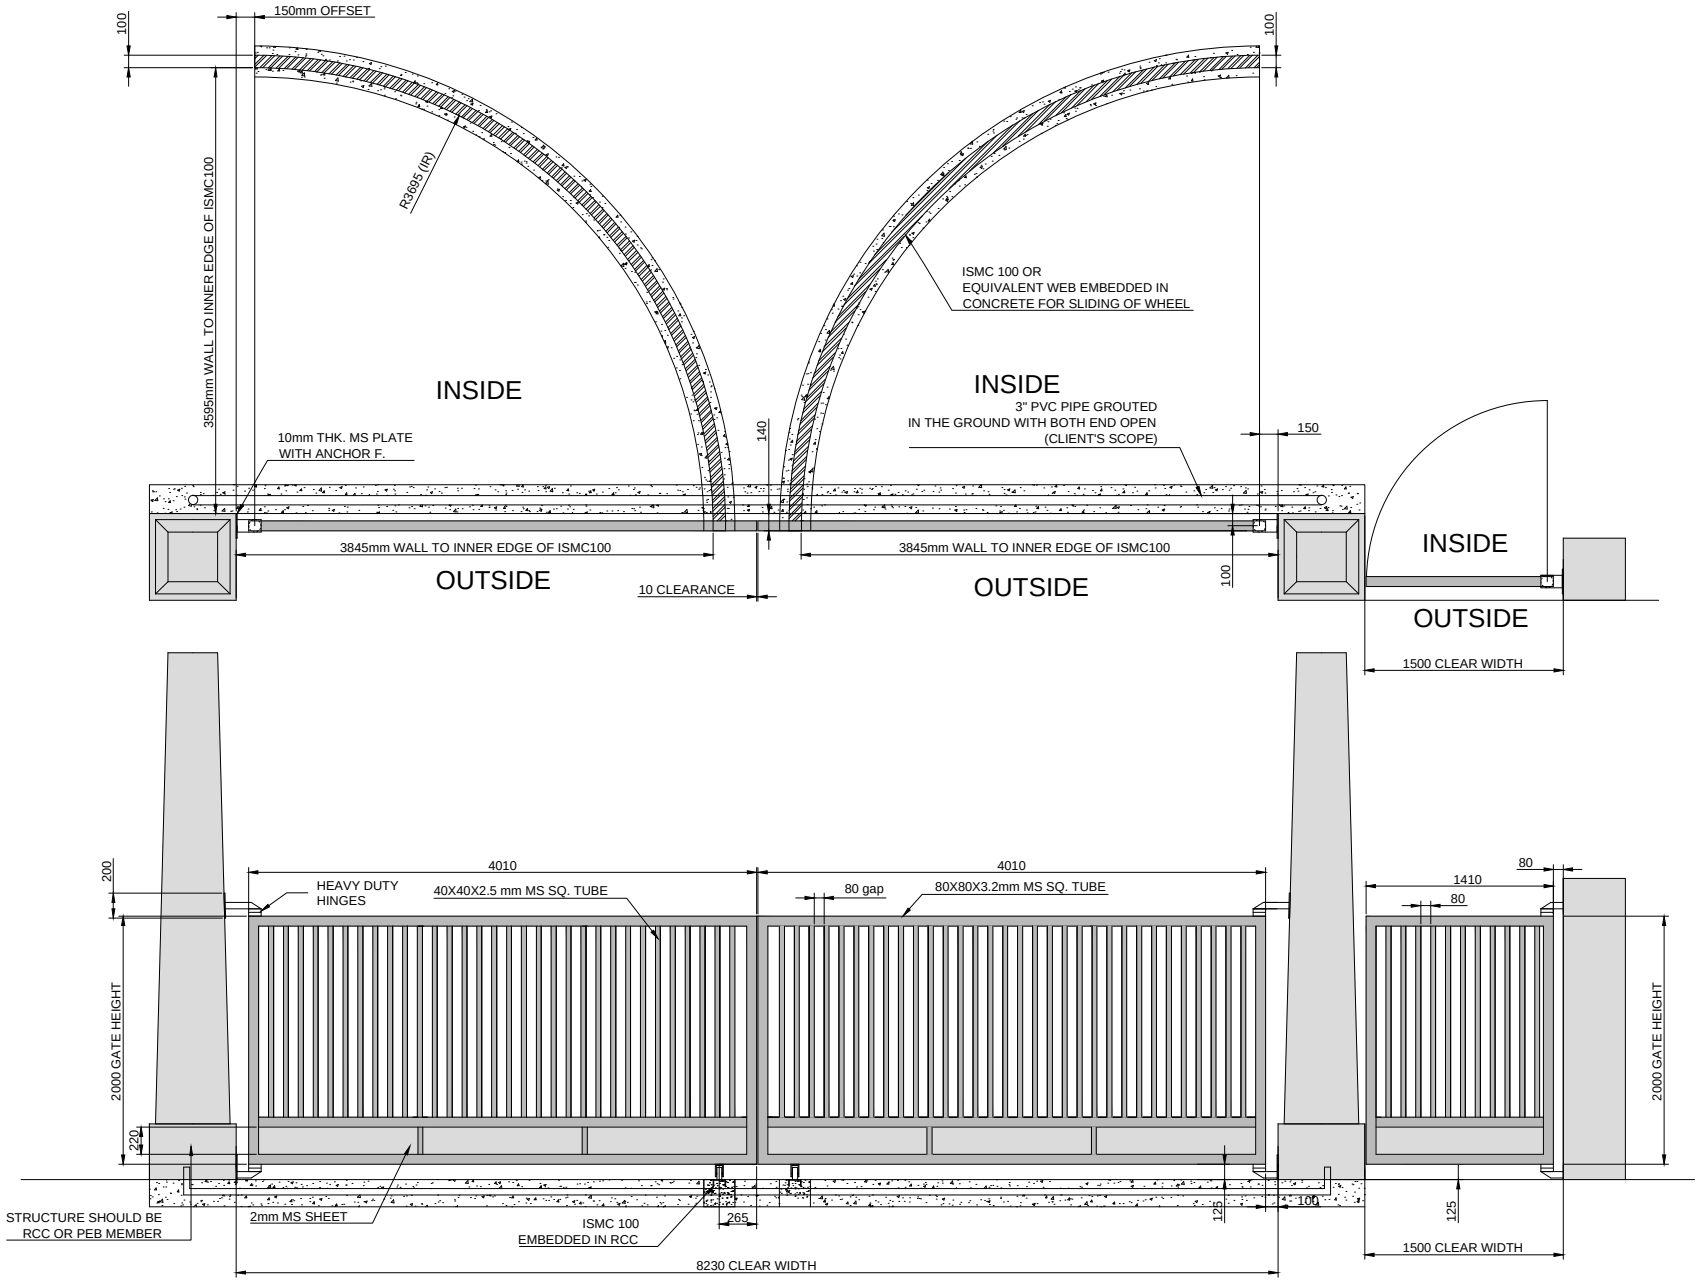

OUTSIDE ELEVATION

DIMENSION :

CLEAR WIDTH	CLEAR HEIGHT	QUANTITY
8230 mm	2000 mm	01 NOS.
1500 mm	2000 mm	01 NOS.

MATERIAL SPECIFICATIONS:

SR NO.	TUBE SIZES	
1	80x80x3.2mm MS TUBE	OUTER TUBE
2	40x40x2.5mm MS TUBE	INNER TUBE
3	2mm MS SHEET	AT BOTTOM

MODIFICATIONS DONE:-
1.Tube pattern are changed as per instructions
2.Gate dimensions have been revised according to actual site dimensions.
3.Ball type bearing and thrust bearing are respectively used in Top and Bottom hinges for swing gate & wicket gate.

NIHVA TECHNOLOGIES PVT. LTD.
NIHVA TECHNOLOGY PVT. LTD. PUNE
Email:- info@nihva.com
Website:- www.nihva.com

TITLE:

MANUAL SWING GATE & WICKET GATE

CLIENT'S APPROVAL :

CLIENT - LUPIN LIMITED

PROJECT -

SITE LOCATION - SIKKIM

DWG. NO. : NIHVA/16-17/0098/R03

SCALE: NTS | WT: | SHEET:1 OF 1

DRAWN BY: OMKAR | DATE: 21-11-2016

CHECK : SAGAR P. | DATE: 21-11-2016

If any queries contact : projects@nihva.com

NOTE: ALL DIMENSION ARE IN mm

THIS DRAWING & DESIGNING IS THE PROPERTY OF NIHVA TECHNOLOGIES. NOT BE SOLD OR COPY TO ANY OTHER CONCERN.