

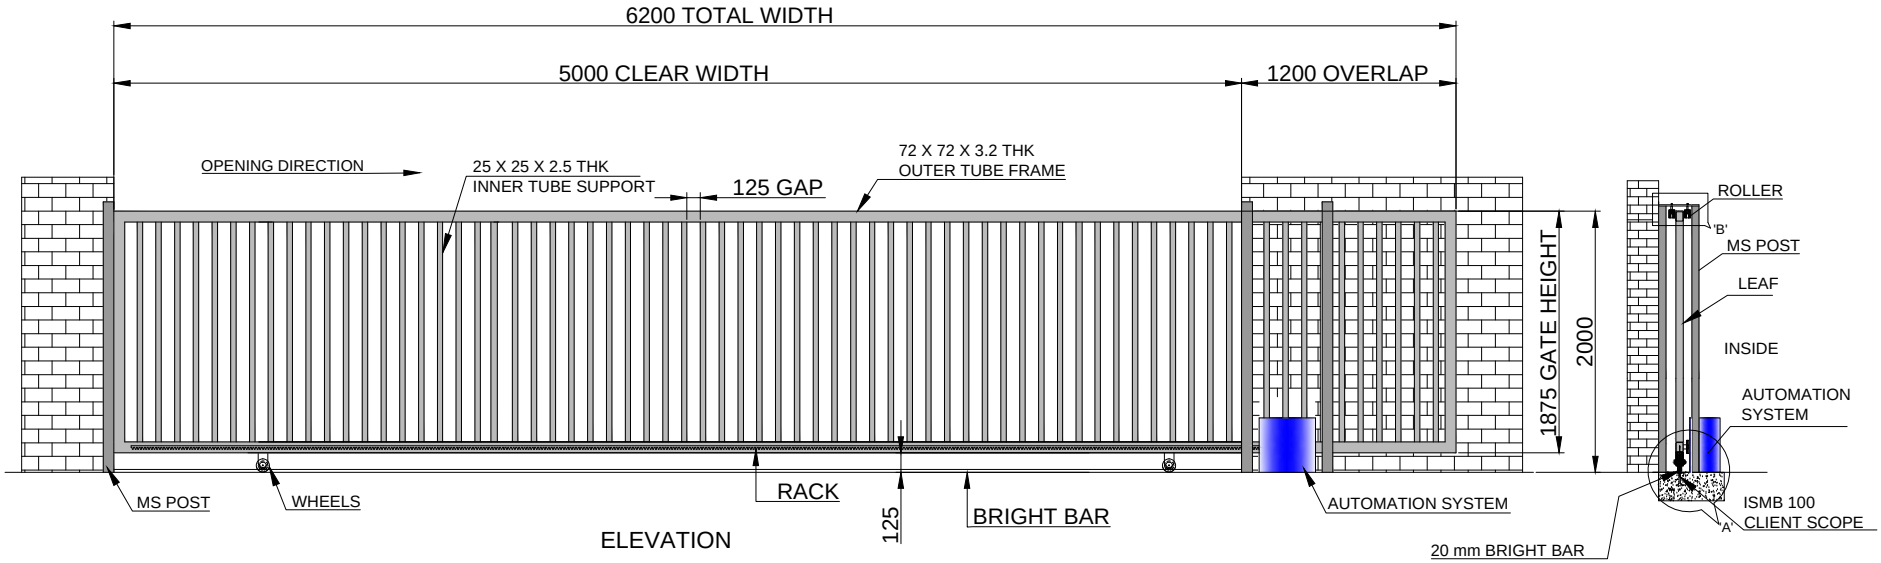



ELEVATION

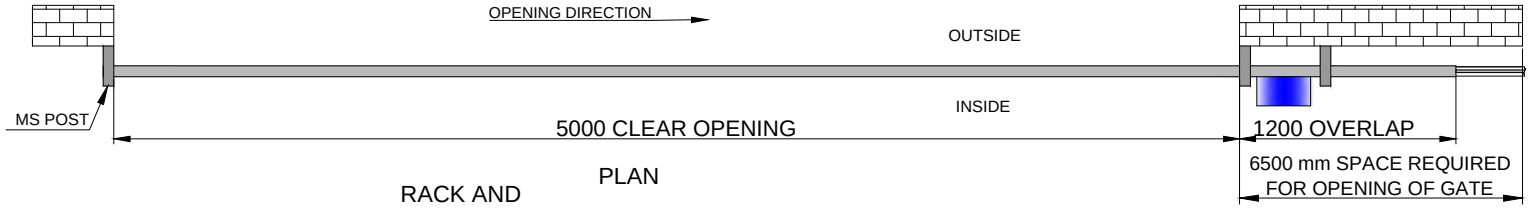

PLAN

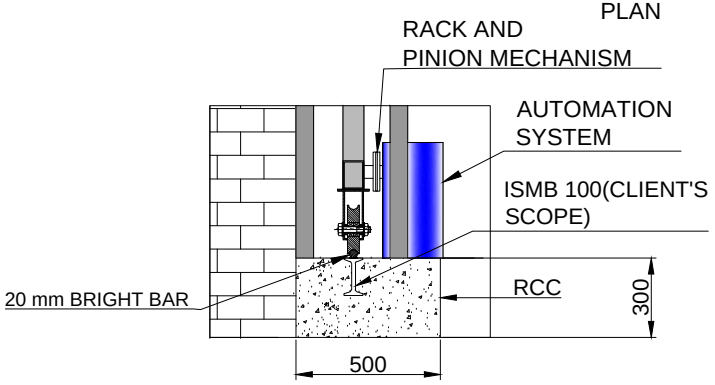

DETAIL VIEW OF A

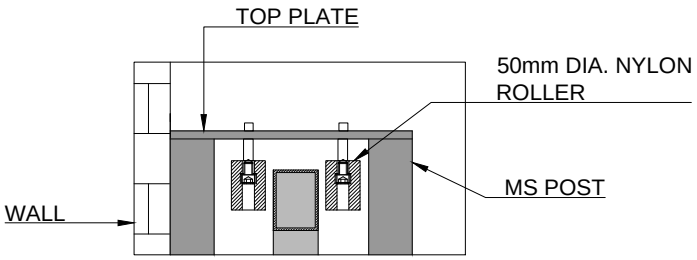

DETAIL VIEW OF B

TOLERANCE- ±10mm

NOTE-
1. ALL REQUIRED CIVIL WORK WILL BE IN CLIENTS SCOPE.
2. TWO COATS OF PRIMER AND TWO COATS OF SYNTHETIC ENAMEL PAINT OF APPROVE SHADE.
3. SAFETY ACCESSORIES : FLASHING LIGHT, SAFETY PHOTOCELL.
4. GATE LEAF WILL BE IN TWO PARTS FOR TRANSPORTATION & WILL BE WELD TOGETHER ON SITE.

This drawing & design is the property of NIHVA TECHNOLOGIES. Not to be sold or copied to any other concern.

TITLE: AUTOMATIC SLIDING GATE			NIHVA TECHNOLOGIES PVT. LTD. PUNE Tel : 020 66304033 Email:- info@nihva.com Website:- www.nihva.com
	NAME	SIGN	DATE
DRAWN	P.A		18.06.2020
CHECK	G.J		18.06.2020
APPRD.			
CLIENT - MEENAKSHI METAL FORMS			
PROJECT -			
SITE LOCATION -			
If any queries contact : design@nihva.com			DWG. NO. : NIHVA/20-21/0021 REV- R00
ALL DIMENSION ARE IN mm			SCALE: NTS WT: SHEET: