


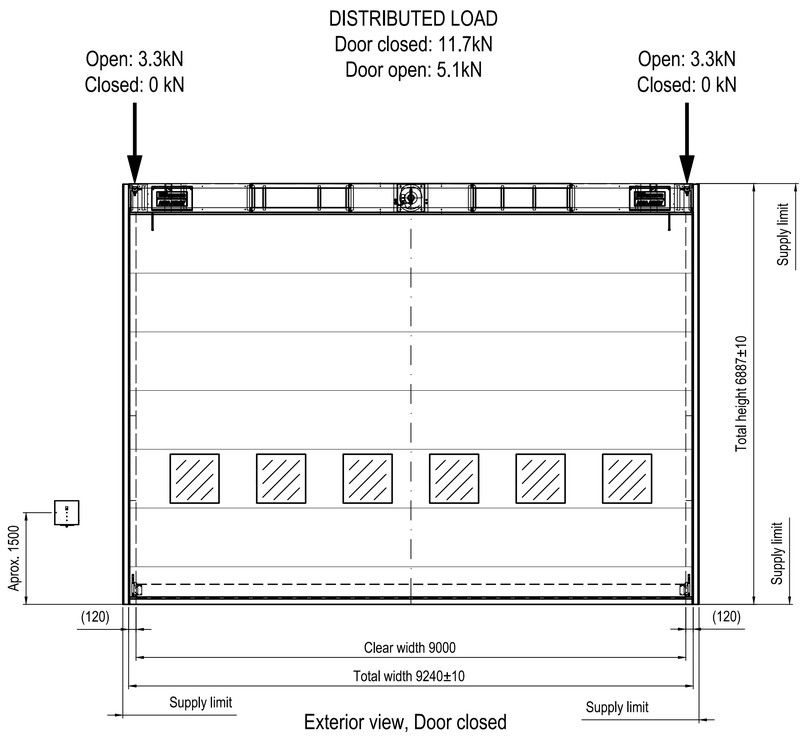



Exterior view, Door closed

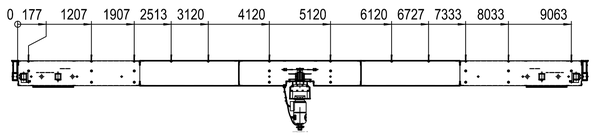


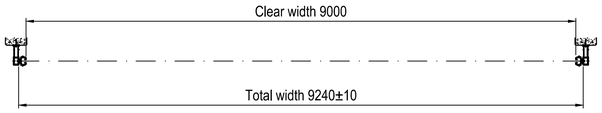



Door leaf is not shown for clarification

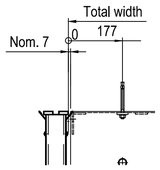

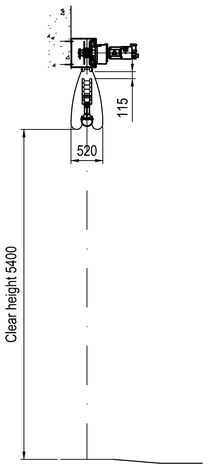


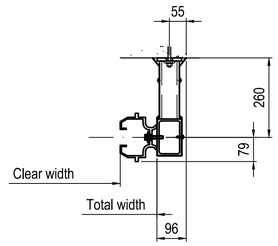

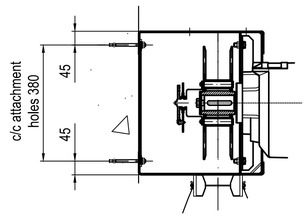

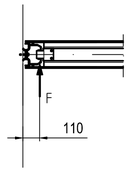

Force by differential pressure transferred to guide rail at each intermediate position.
F=5.1 kN

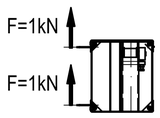

Load on header box attachment (each screw), due to wind load and door weight

NOT INCLUDED IN DOOR SUPPLY:

1. Design and supply of all door supporting structural components.
2. Design and supply of all closure between door and adjacent steel.
3. Door jambs adjustable for overall door width and true to plumb.
4. Paint job after completed door installation.
5. Any frameworks being provided by ASSA ABLOY will be clearly indicated as "by ASSA ABLOY".

REQUIREMENTS ON BUILDING:

6. Door head support must be straight within 1/600 of span in the in/out direction and free from protrusions of any kind.
7. For a single door leaf, door head support should be horizontal and straight within 1/600 of span at distributed full door load.
8. Door side jambs must be smooth, straight and parallel, out of plumb must not exceed 2mm/m (total deviation at full length 5 mm) in any direction.
9. Any footings at bottom of jamb columns must not interfere with installation of guide rails at floor level.
10. At time of installation, finished floor, free from obstructions, out to a distance of 2 m on each side of door centreline must be available.
11. Header box must be accessible from both sides during installation.

DOOR PROPERTIES:

12. The door is designed to withstand a differential pressure of 1.15 Kpa x 1.5 FOS
13. Color of door fabric: Please specify
14. Side profiles
15. Metal trim: motor side

ELECTRICAL:

16. One main control panel provided of PLC type.
17. Audible and visual alarm
18. Back-up power switch
19. Safety edge
20. Approx. size of main control panel: WxHxD (500mm x 600mmx250 mm),
21. Power: 2.7kW
22. Nom. current: 6.4A
23. (max. allowed voltage drop at start: 5%)

BELT HOIST UNITS:
SK 873.1-100L/4 Z dual brake

DESIGNED KMÖ		SIZE A1	SCALE 1:50
CODE 84691		If not otherwise stated:	
ITEM NO		Tolerances ISO 2768-m EN ISO 13920-B	
DATE 2021-08-12		Cutting class ISO 9013-442	
ASSA ABLOY		Weld class ISO 5817-C	
		Surface finish Smooth raw surface	

Delhi Fire Station

India

Megadoor 9000 x 5400

Sales interface

DRAWING NO 74147

REVISION --

PLOT DATE

This document is the property of ASSA ABLOY Entrance Systems AB and shall not be used, sold, copied, imparted to a third party or used for any other unauthorized purpose.