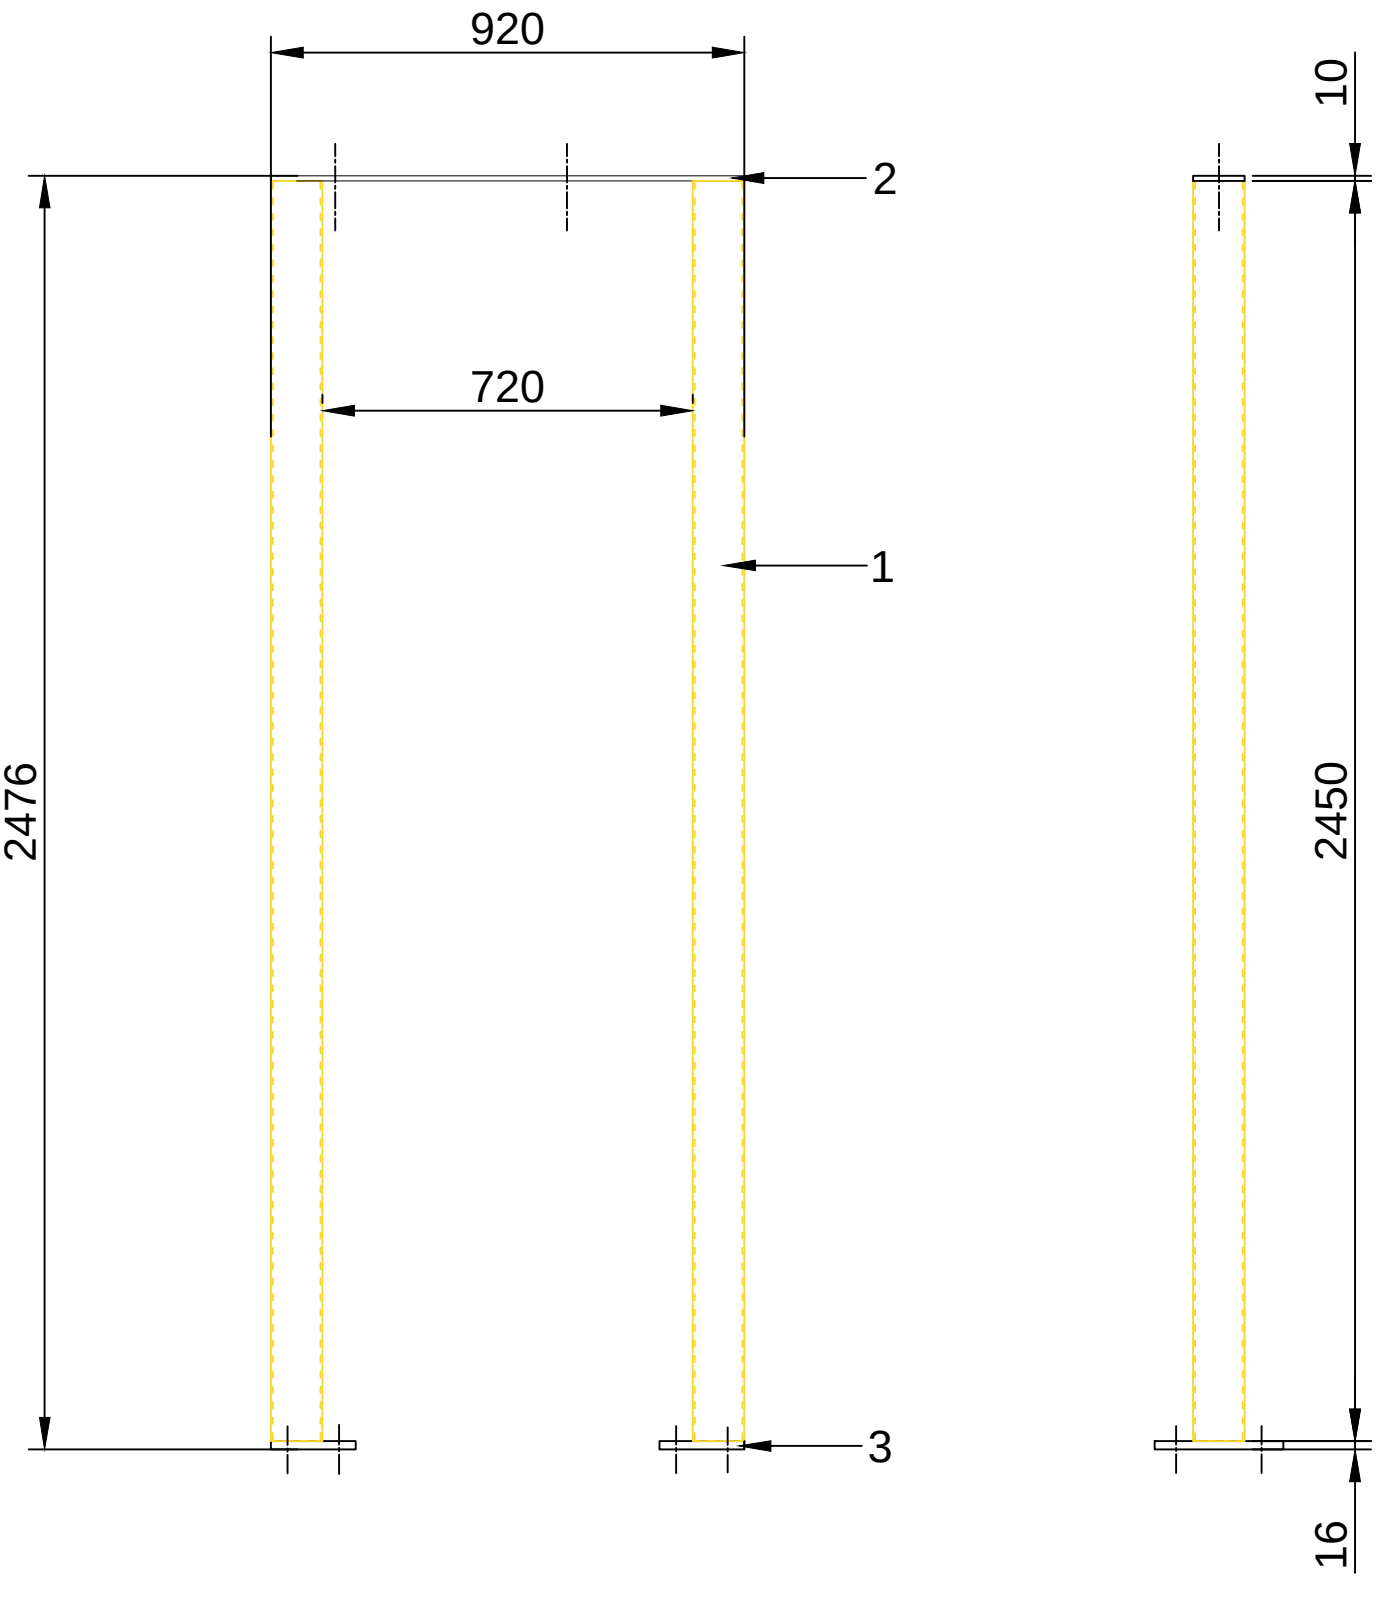

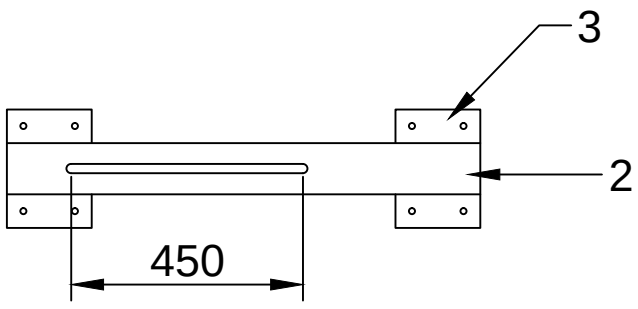

Note: Given quantity is for single gate i.e. 4 post.

SR. NO.	DESCRIPTION	SPECIFICATION	QTY
1	SQ. TUBE	100 X 100 X 4, 2450 LENGTH	8 NOS
2	TOP PLATE (NIHVA/21-22/VDR/054)	920 X 100 X 10 THK	4 NOS
3	BOTTOM PLATE (NIHVA/21-22/VDR/054)	230 X 165 X 16 THK	8 NOS
4	ANCHOR FASTNER	M12 X 150	32 NOS

This drawing & design is the property of NIHVA TECHNOLOGIES. Not to be sold or copied to any other concern.

TITLE: POST

	NAME	SIGN	DATE
DRAWN	G.P.		05.03.22
CHECK	A.K.		05.03.22
APPRD.	V.T.		05.03.22

If any queries contact : design@nihva.com

ALL DIMENSION ARE IN mm

NIHVA TECHNOLOGIES PVT. LTD.
NIHVA TECHNOLOGIES PVT. LTD. PUNE
Tel : 020 66304033
Email:- info@nihva.com
Website:- www.nihva.com

CLIENT -SRF

LOCATION - PITHAMPUR

PRODUCT - MOTORIZED SLIDING GATE

NIHVA\21-22\MFG\030 | REV- 00

SCALE: NTS | SHEET: 01 OF 01