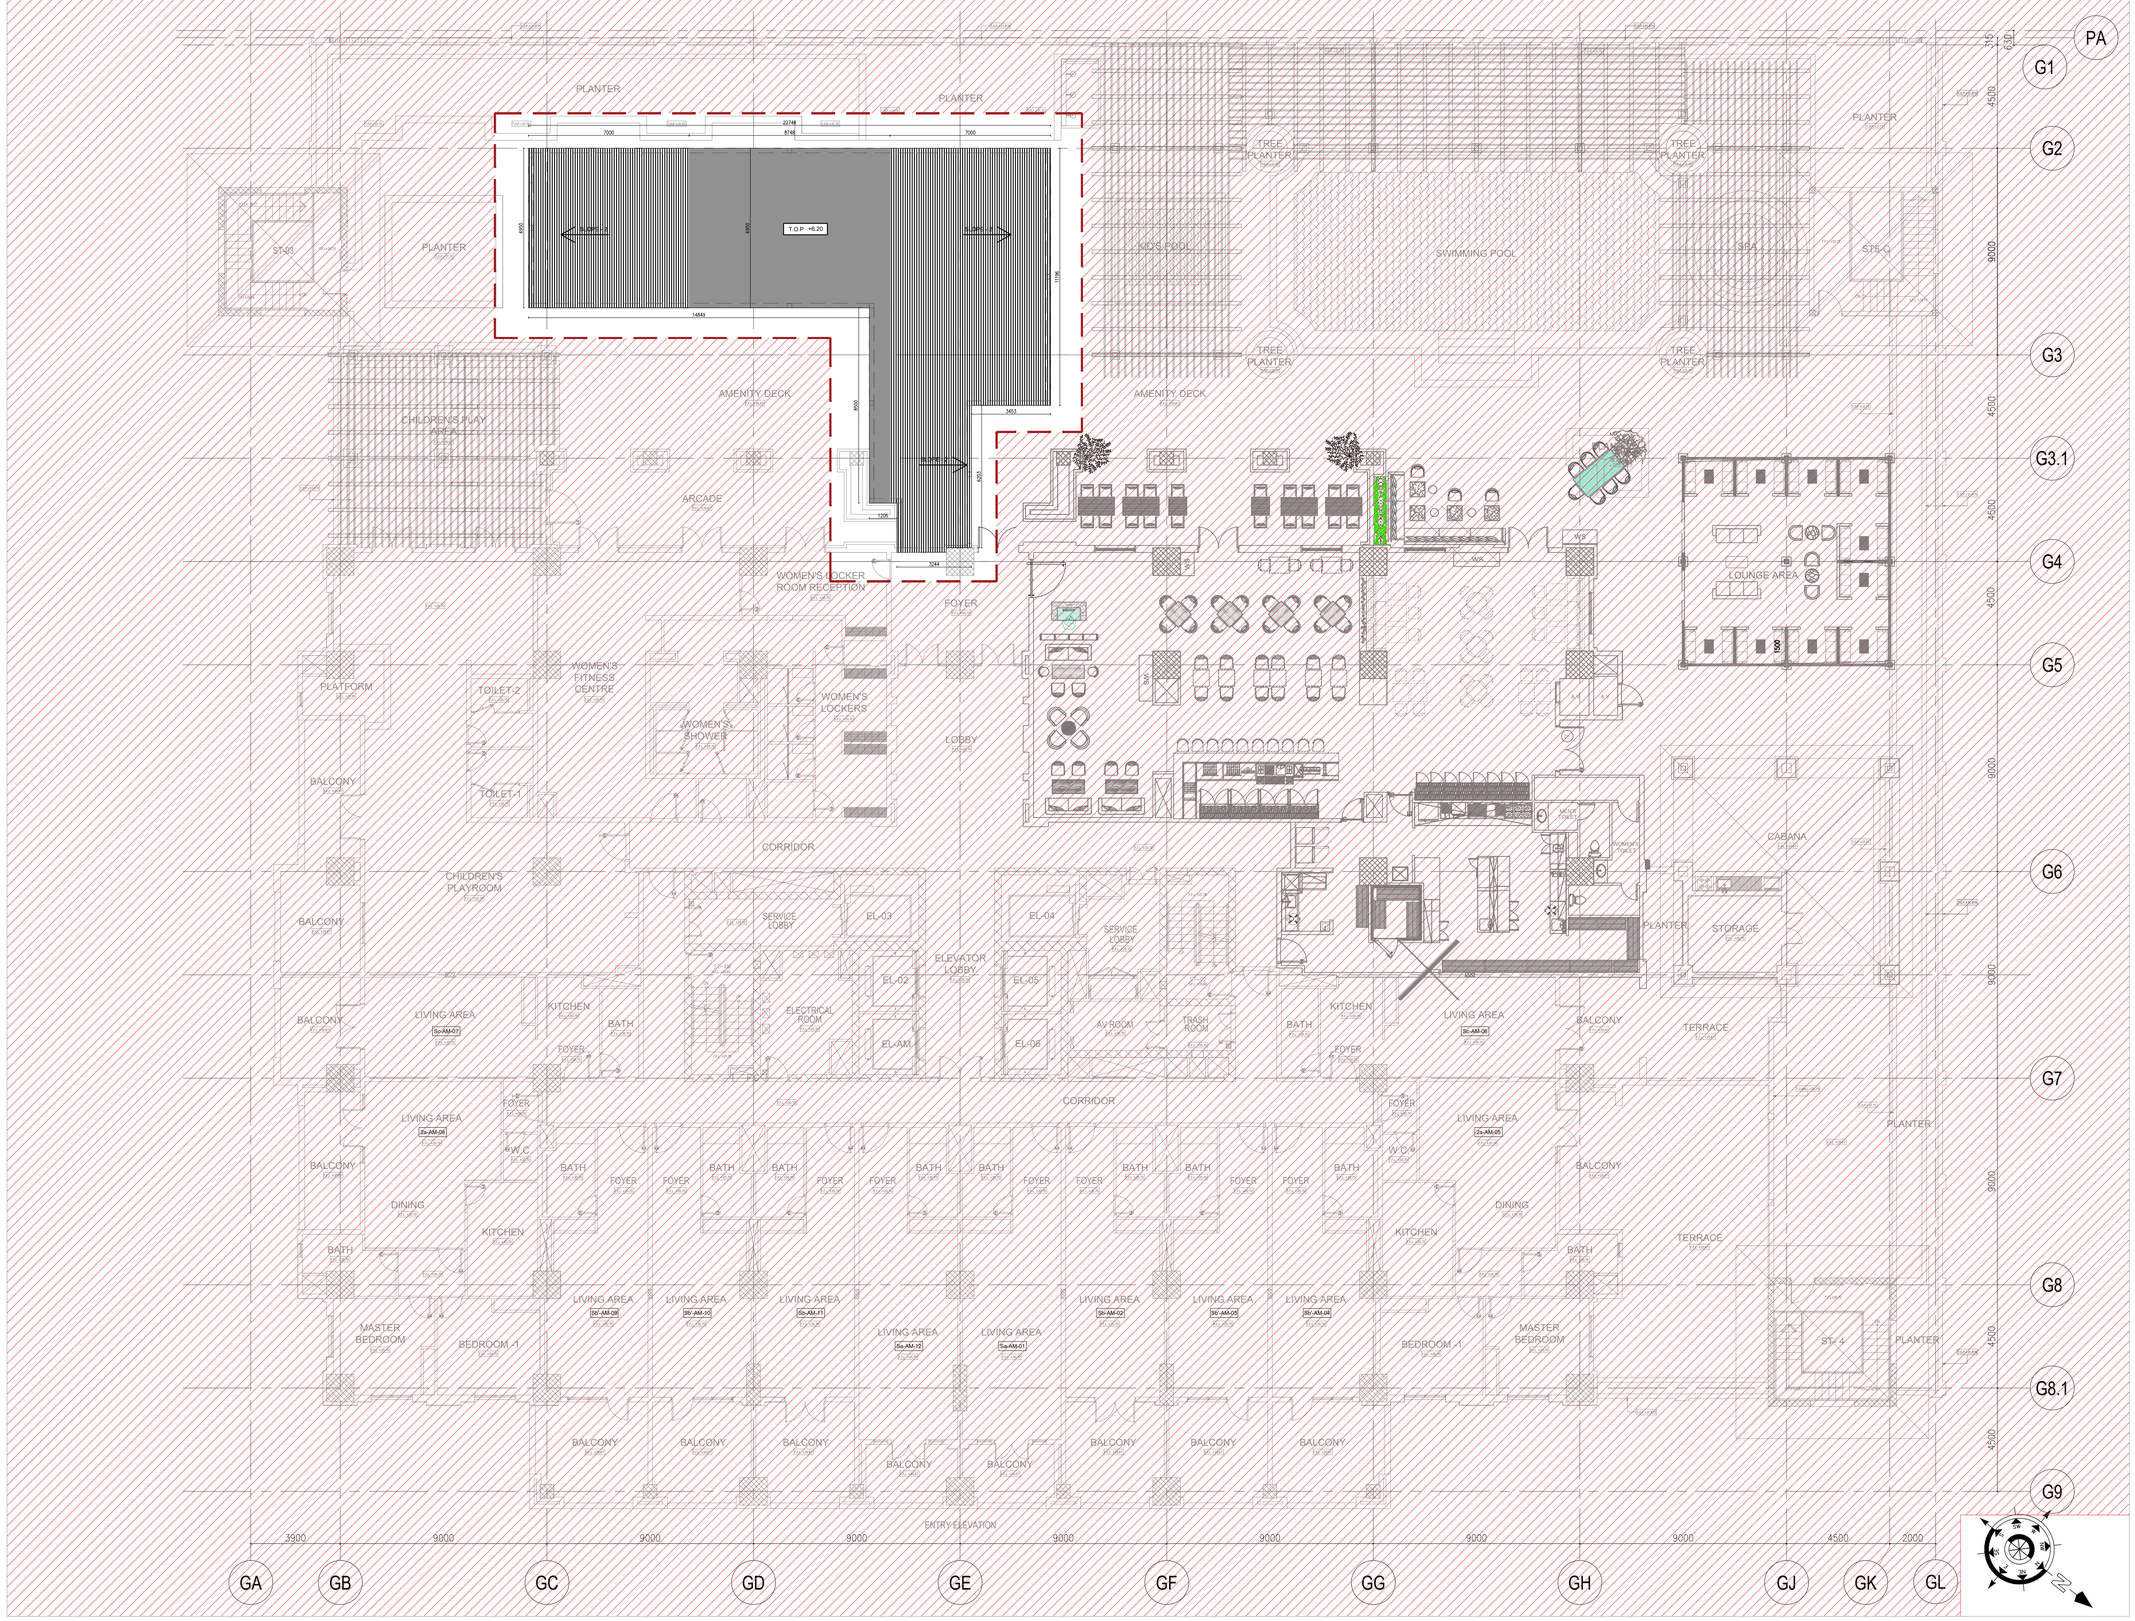


GENERAL NOTES :

1 - ALL DIMENSIONS ARE IN METERS, LEVELS ARE IN METERS.
2 - DO NOT SCALE THIS DRAWING.
3 - ALL ARCHITECTURAL DWGS. MUST BE READ IN CONJUNCTION WITH STRUCTURAL & ELECTRO -MECHANICAL DRAWINGS RELATED SPECIFICATIONS.
4 - THE CONTRACTOR MUST INFORM THE ENGINEER ABOUT ANY CONTRADICTION OF ANY KIND BEFORE BEGINNING OF CONSTRUCTION.
5 - ALL MATERIALS TO BE APPROVED BY ARCHITECTS/ ENGINEERS. BEFORE PROCURING THE SAME.
6 - THE CONTRACTOR SHALL SUBMIT THE SHOP DRAWING AS PER ACTUAL SITE MEASUREMENTS FOR APPROVAL, BEFORE COMMENCING THE WORK /FABRICATION ON SITE.

1	ISSUED FOR APPROVAL	08.09.2025	T.B.M	J.K.
0	ISSUED FOR APPROVAL	16.07.2025	M.S	J.K.
Rev.No.	DESCRIPTION	DATE	CHECKED	APPROVED

PROJECT OWNER :

PROJECT :

TOWER 26 - OUTSIDE RESTAURANT


LOCATION :

THE PEARL - QATAR

DRAWING TITLE :

SITE DEVELOPMENT PLAN

DATE :	JULY 2025	SCALE	N.T.S
		DRAWN BY	K.H
DRAWING NUMBER	A-100	CHECKED BY	M.S
		JOB No.	----

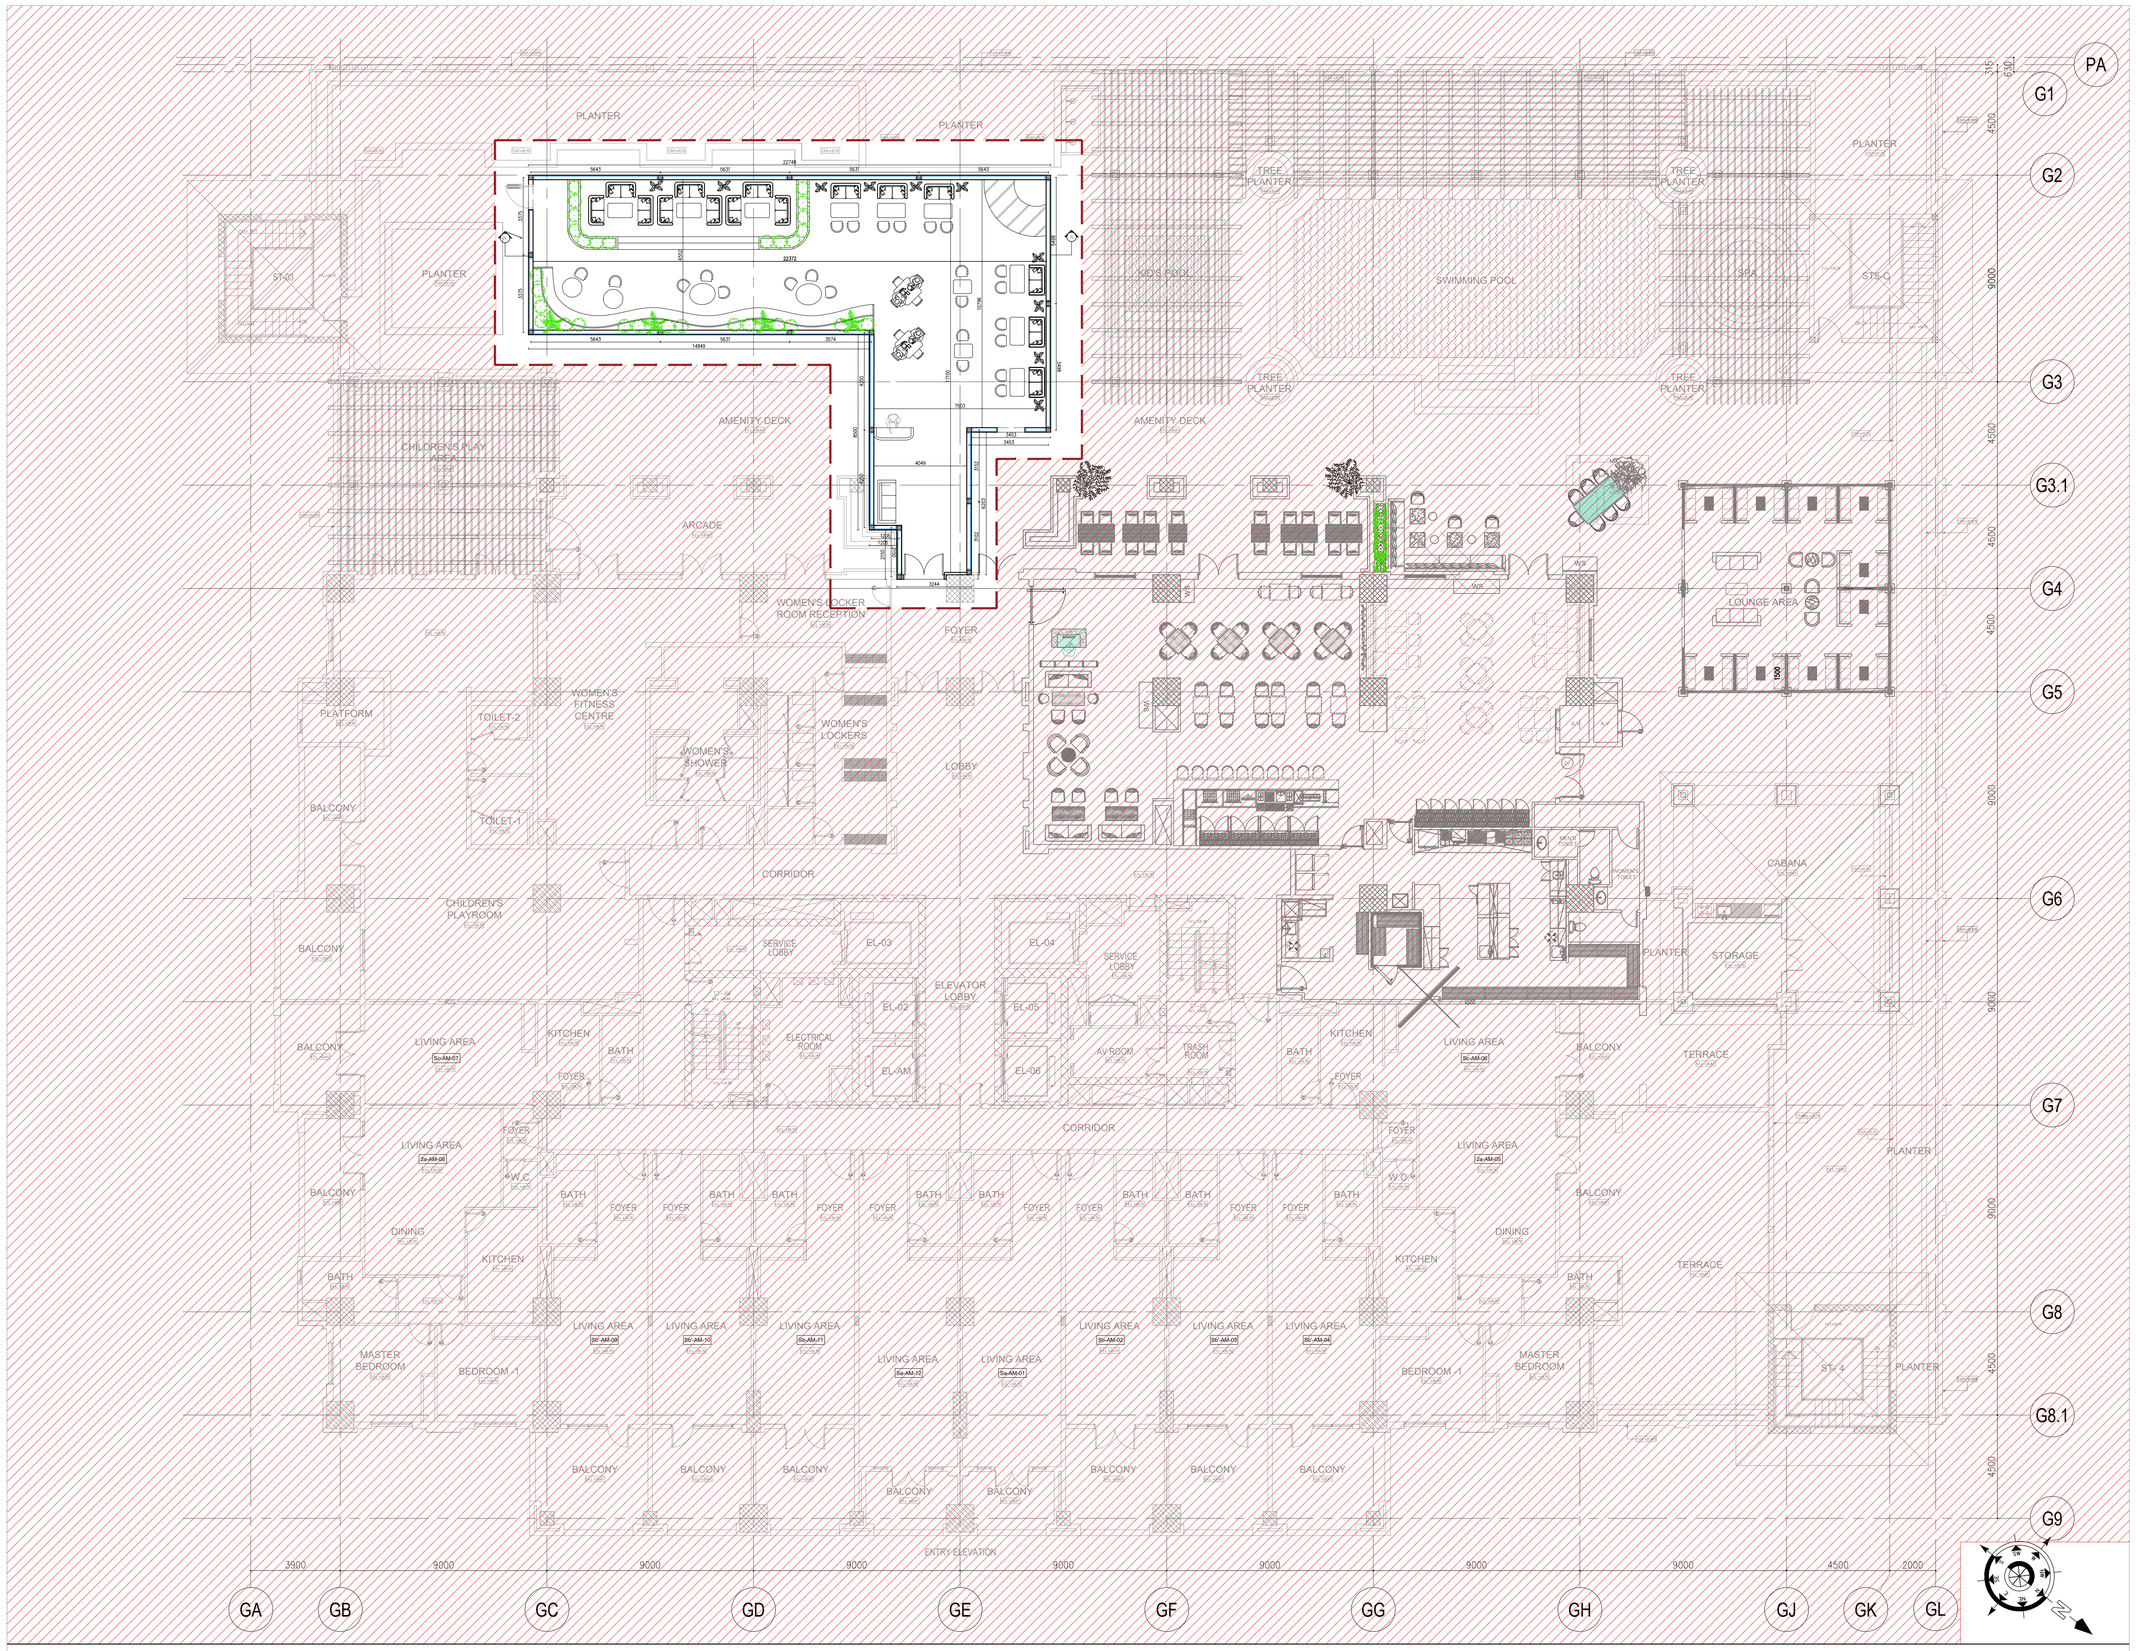

GENERAL NOTES :

1 - ALL DIMENSIONS ARE IN METERS, LEVELS ARE IN METERS.
2 - DO NOT SCALE THIS DRAWING.
3 - ALL ARCHITECTURAL DWGS. MUST BE READ IN CONJUNCTION WITH STRUCTURAL & ELECTRO -MECHANICAL DRAWINGS RELATED SPECIFICATIONS.
4 - THE CONTRACTOR MUST INFORM THE ENGINEER ABOUT ANY CONTRADICTION OF ANY KIND BEFORE BEGINNING OF CONSTRUCTION.
5 - ALL MATERIALS TO BE APPROVED BY ARCHITECTS/ ENGINEERS. BEFORE PROCURING THE SAME.
6 - THE CONTRACTOR SHALL SUBMIT THE SHOP DRAWING AS PER ACTUAL SITE MEASUREMENTS FOR APPROVAL, BEFORE COMMENCING THE WORK /FABRICATION ON SITE.

Rev.No.	DESCRIPTION	DATE	CHECKED	APPROVED
1	ISSUED FOR APPROVAL	08.09.2025	T.B.M	J.K.
0	ISSUED FOR APPROVAL	16.07.2025	M.S	J.K.

PROJECT :

TOWER 26 - OUTSIDE RESTAURANT


LOCATION :

THE PEARL - QATAR

DRAWING TITLE :

OVERALL FLOOR PLAN

DATE :	JULY 2025	SCALE	N.T.S
		DRAWN BY	K.H
DRAWING NUMBER	A-101	CHECKED BY	M.S
		JOB No.	----

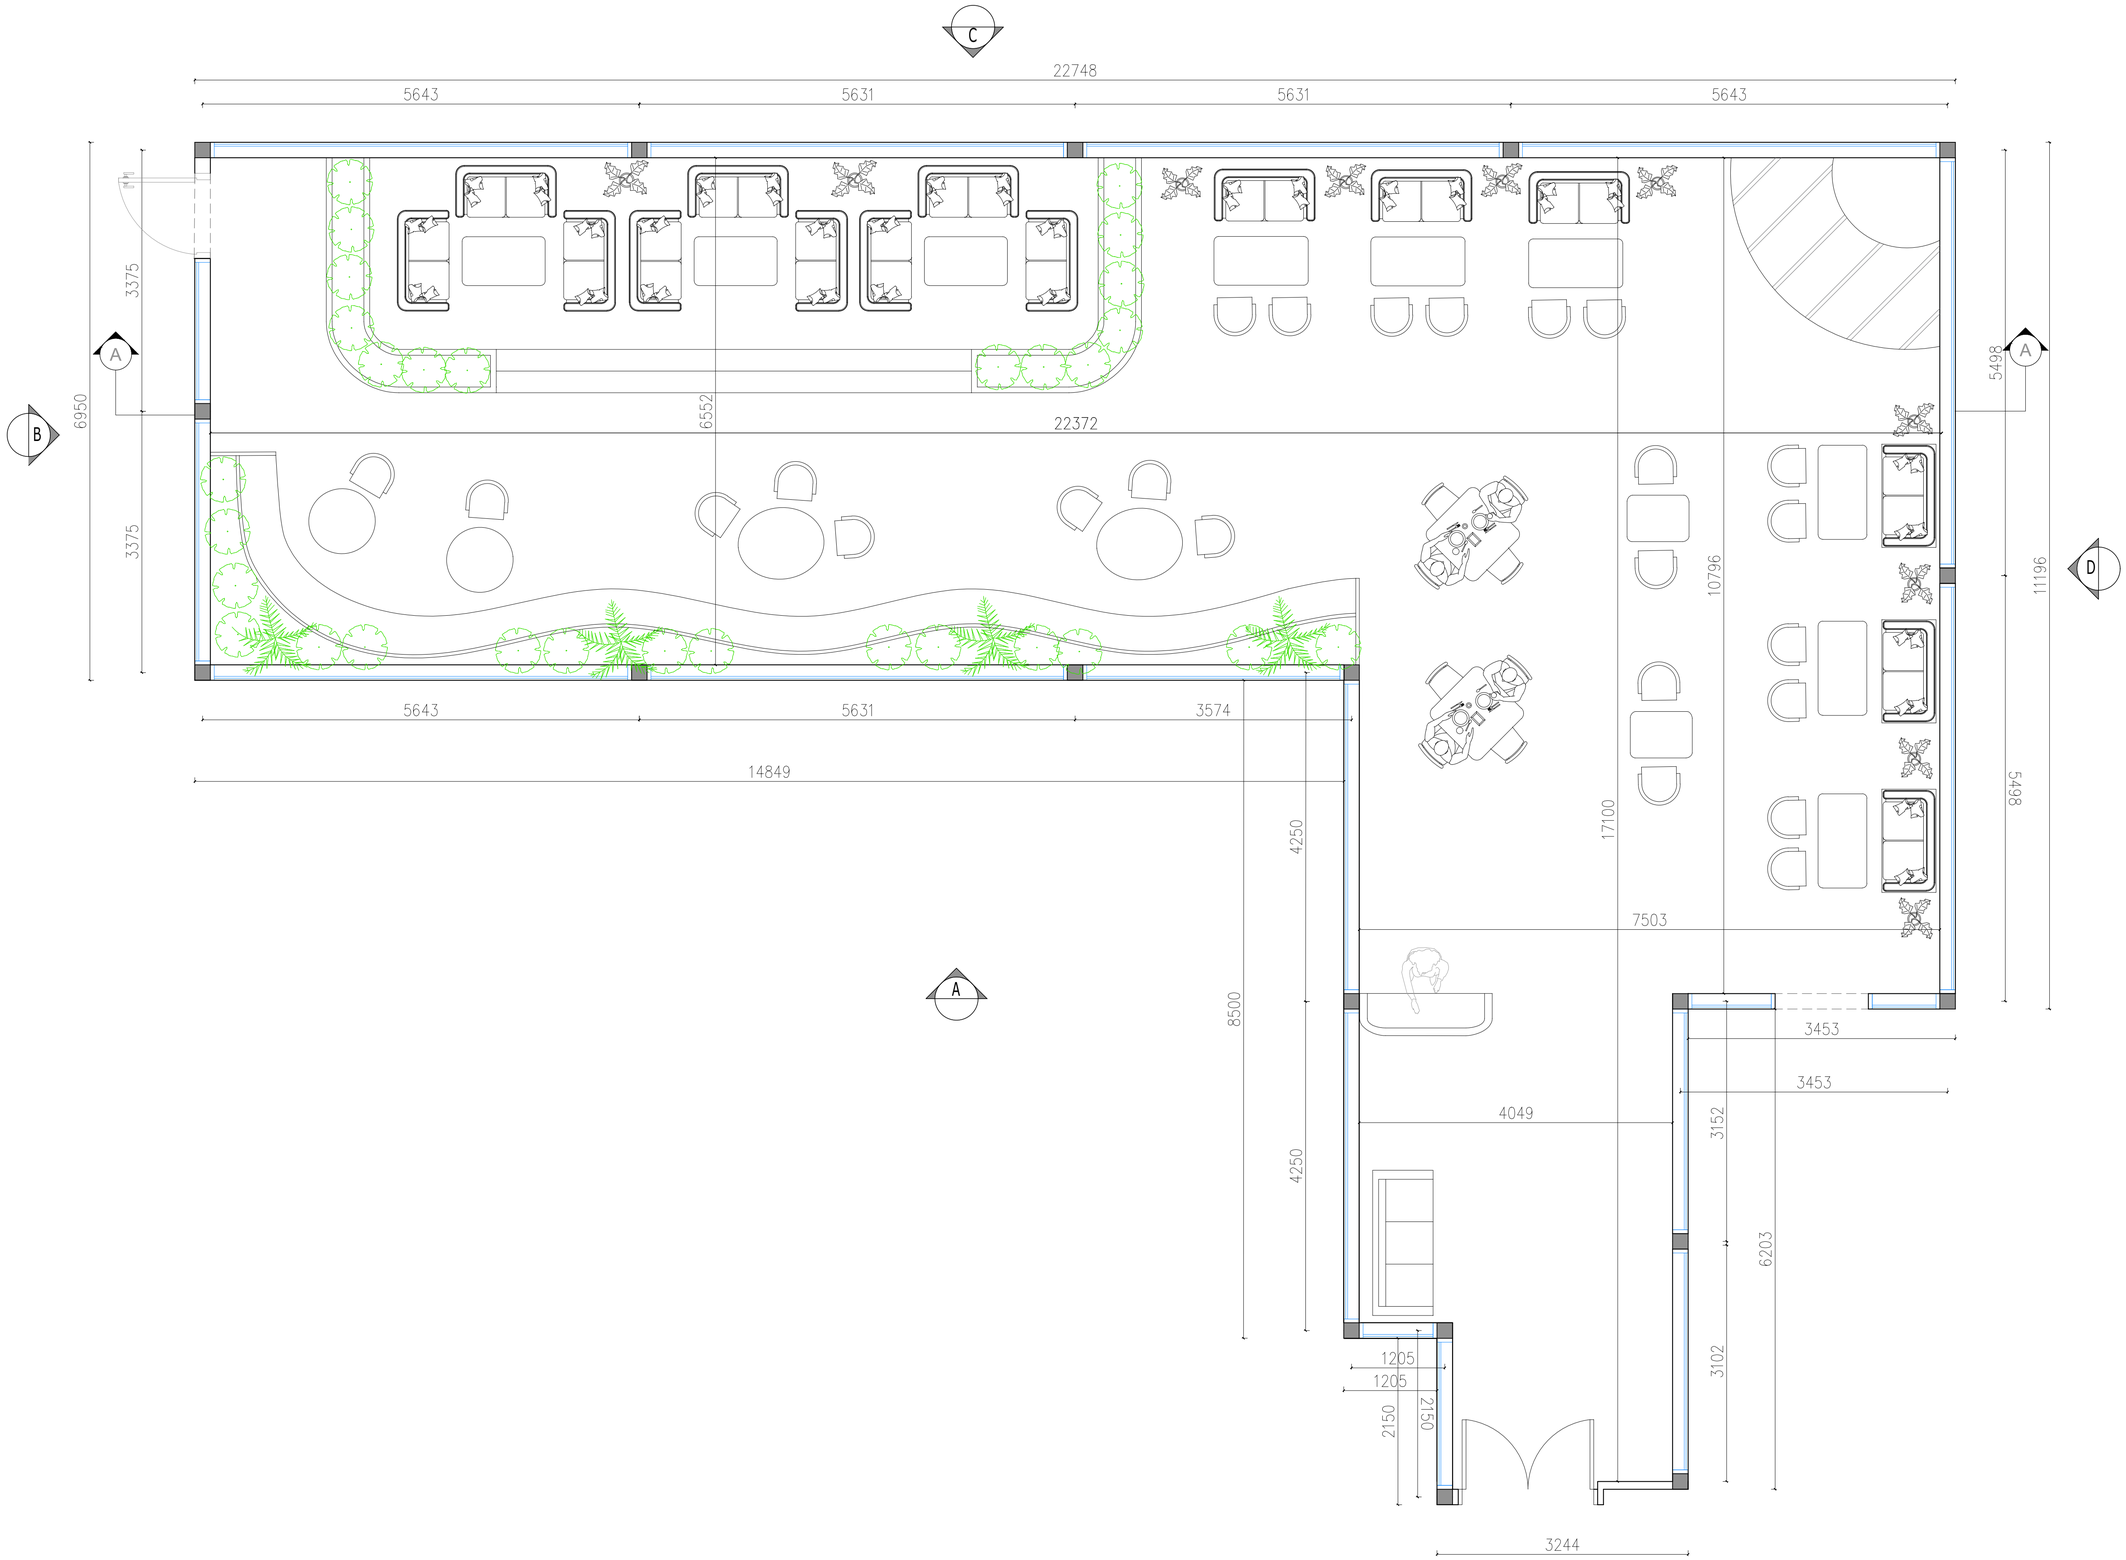

GENERAL NOTES :

1 - ALL DIMENSIONS ARE IN METERS, LEVELS ARE IN METERS.
2 - DO NOT SCALE THIS DRAWING.
3 - ALL ARCHITECTURAL DWGS. MUST BE READ IN CONJUNCTION WITH STRUCTURAL & ELECTRO -MECHANICAL DRAWINGS RELATED SPECIFICATIONS.
4 - THE CONTRACTOR MUST INFORM THE ENGINEER ABOUT ANY CONTRADICTION OF ANY KIND BEFORE BEGINNING OF CONSTRUCTION.
5 - ALL MATERIALS TO BE APPROVED BY ARCHITECTS/ ENGINEERS. BEFORE PROCURING THE SAME.
6 - THE CONTRACTOR SHALL SUBMIT THE SHOP DRAWING AS PER ACTUAL SITE MEASUREMENTS FOR APPROVAL, BEFORE COMMENCING THE WORK /FABRICATION ON SITE.

1	ISSUED FOR APPROVAL	08.09.2025	T.B.M	J.K.
0	ISSUED FOR APPROVAL	16.07.2025	M.S	J.K.
Rev.No.	DESCRIPTION	DATE	CHECKED	APPROVED

PROJECT :

TOWER 26 - OUTSIDE RESTAURANT


LOCATION :

THE PEARL - QATAR

DRAWING TITLE :

RESTAURANT FLOOR PLAN

DATE :	JULY 2025	SCALE	N.T.S
		DRAWN BY	K.H
DRAWING NUMBER	A-102	CHECKED BY	M.S
		JOB No.	----

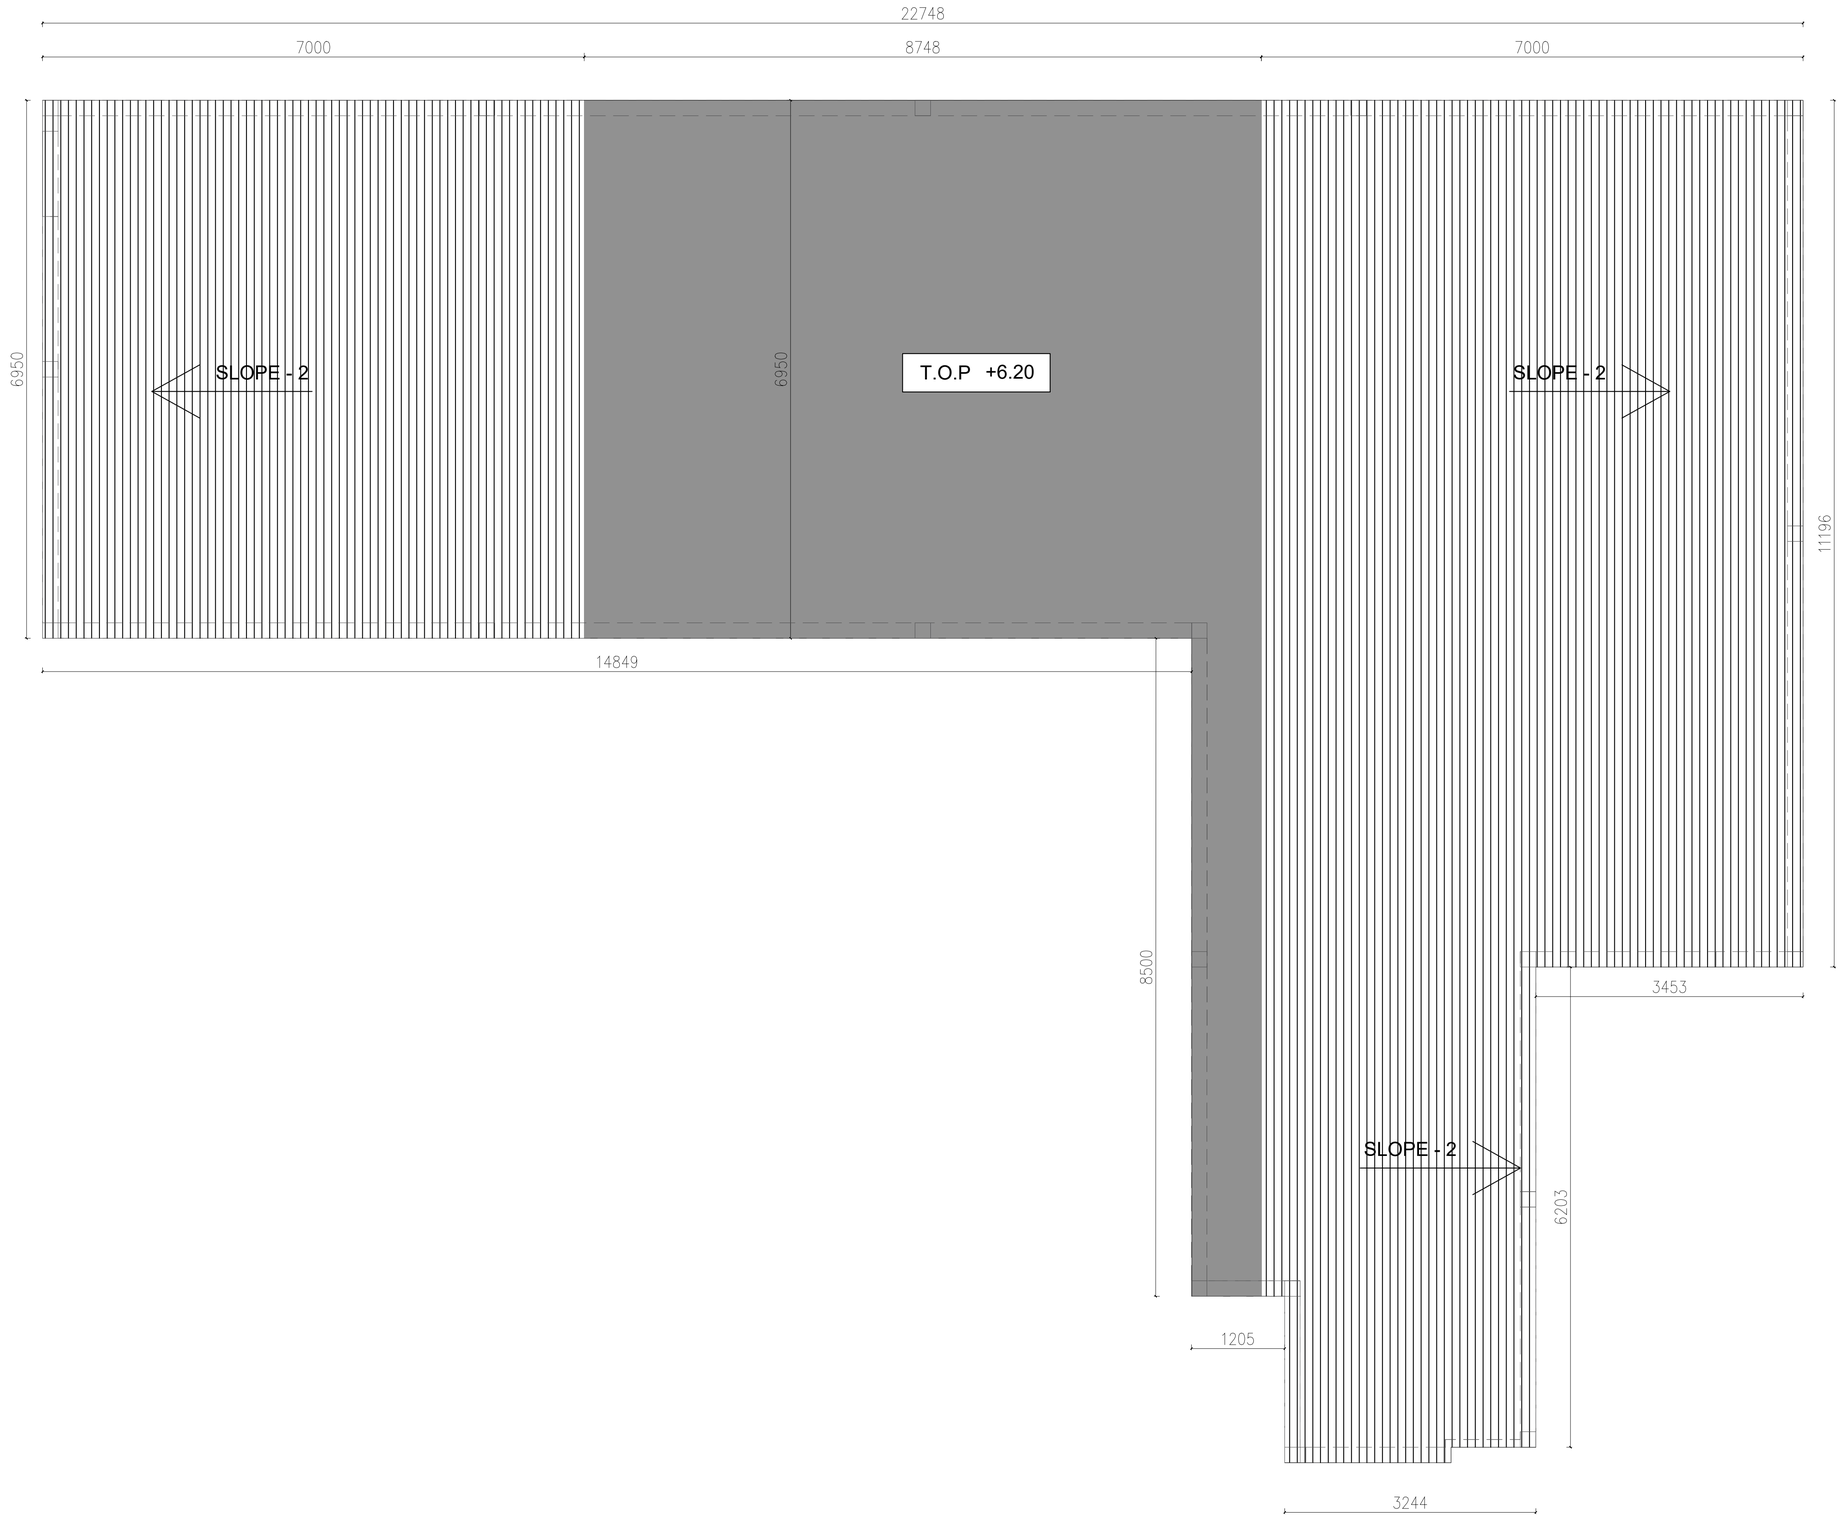

GENERAL NOTES :

1 - ALL DIMENSIONS ARE IN METERS, LEVELS ARE IN METERS.
2 - DO NOT SCALE THIS DRAWING.
3 - ALL ARCHITECTURAL DWGS. MUST BE READ IN CONJUNCTION WITH STRUCTURAL & ELECTRO -MECHANICAL DRAWINGS RELATED SPECIFICATIONS.
4 - THE CONTRACTOR MUST INFORM THE ENGINEER ABOUT ANY CONTRADICTION OF ANY KIND BEFORE BEGINNING OF CONSTRUCTION.
5 - ALL MATERIALS TO BE APPROVED BY ARCHITECTS/ ENGINEERS. BEFORE PROCURING THE SAME.
6 - THE CONTRACTOR SHALL SUBMIT THE SHOP DRAWING AS PER ACTUAL SITE MEASUREMENTS FOR APPROVAL, BEFORE COMMENCING THE WORK /FABRICATION ON SITE.

1	ISSUED FOR APPROVAL	08.09.2025	T.B.M	J.K.
0	ISSUED FOR APPROVAL	16.07.2025	M.S	J.K.
Rev.No.	DESCRIPTION	DATE	CHECKED	APPROVED

PROJFCT OWNFR :

PROJECT :

TOWER 26 - OUTSIDE RESTAURANT


LOCATION :

THE PEARL - QATAR


DRAWING TITLE :

CEILING LAYOUT


DATE :	JULY 2025	SCALE	N.T.S
		DRAWN BY	K.H
DRAWING NUMBER	A-103	CHECKED BY	M.S
		JOB No.	----

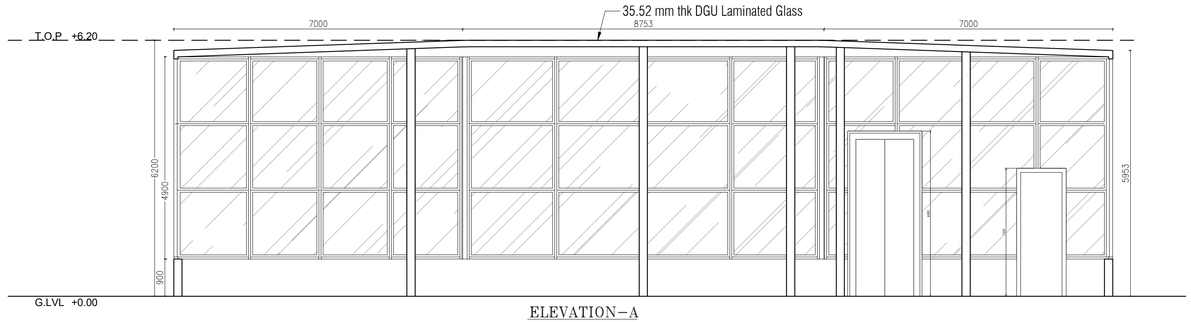


ELEVATION–A
ENTRANCE

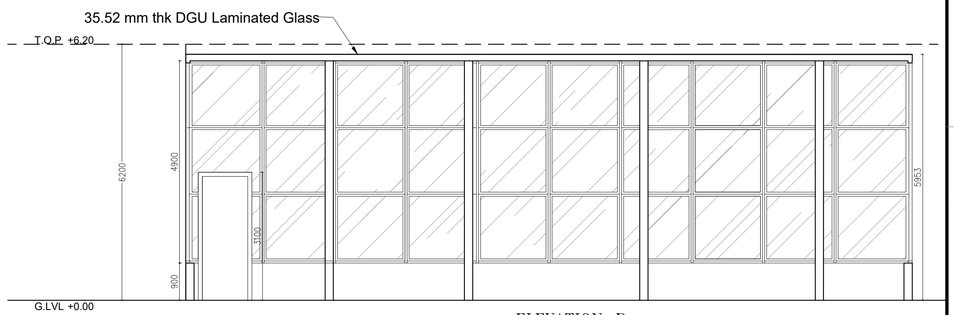


ELEVATION–B

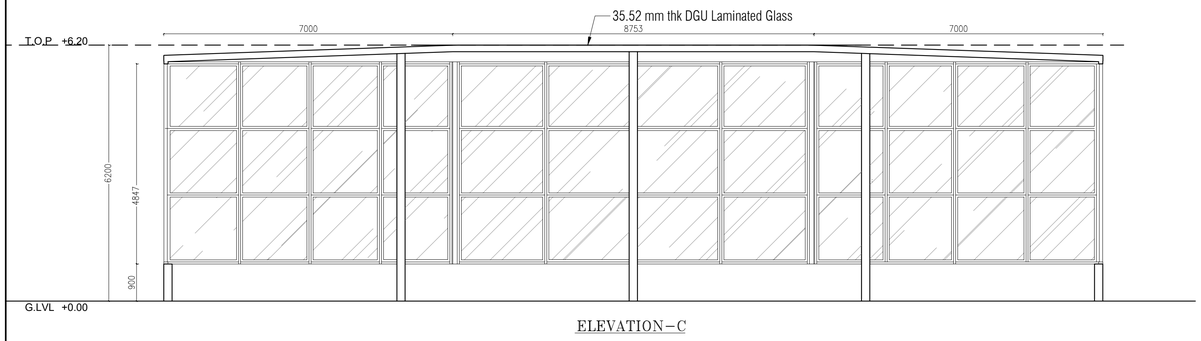

ELEVATION–C

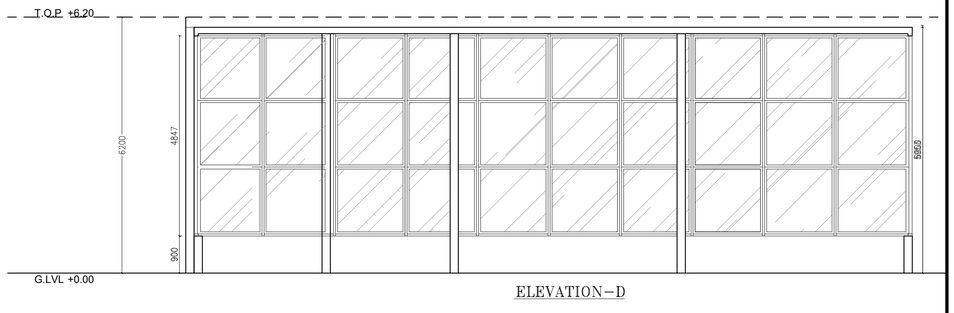

ELEVATION–D

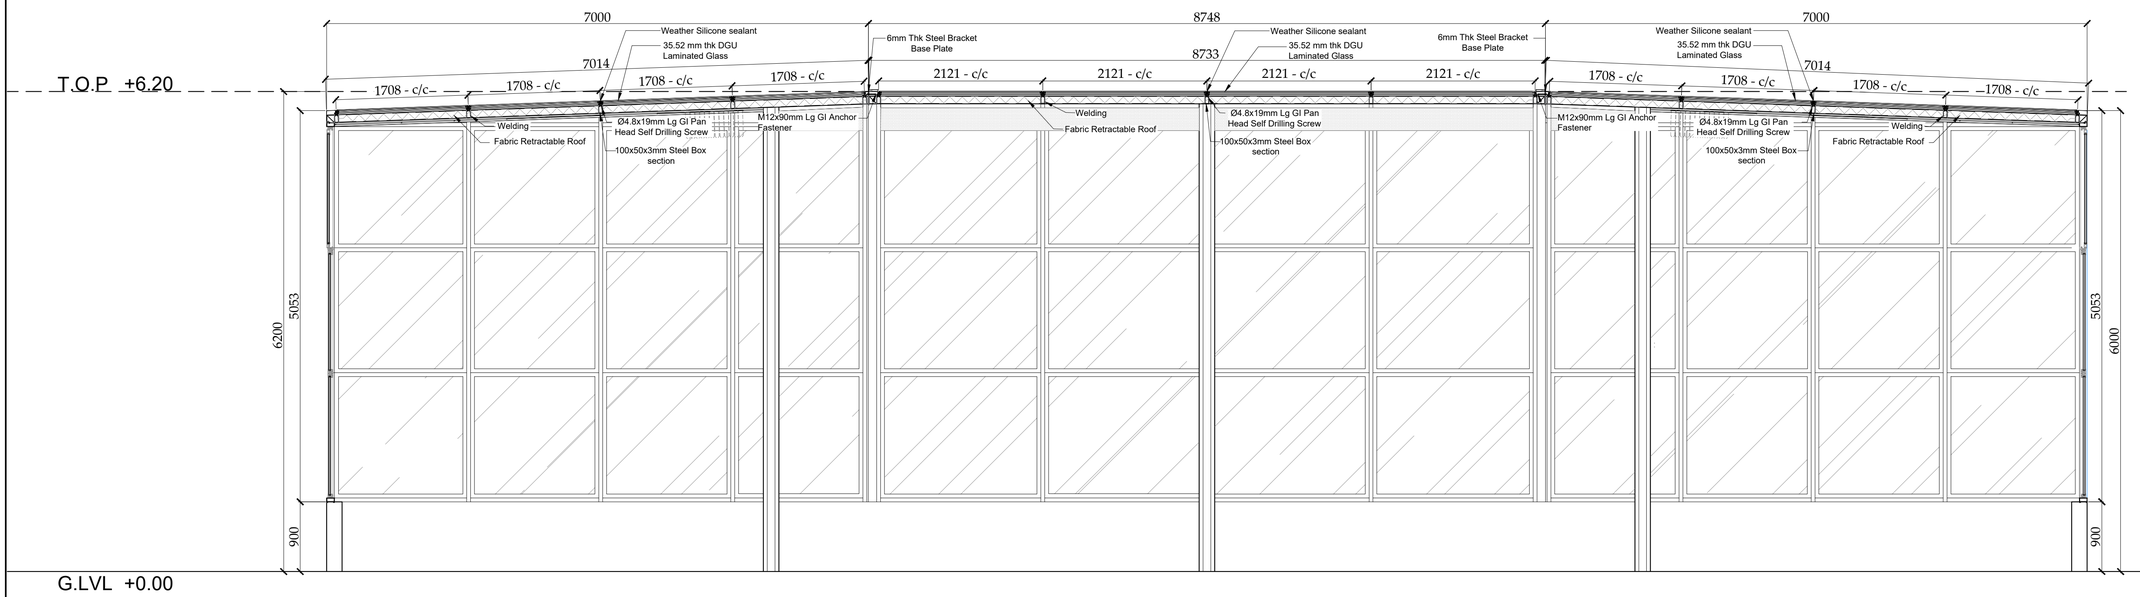

SECTION–AA

GENERAL NOTES :

1 - ALL DIMENSIONS ARE IN METERS, LEVELS ARE IN METERS.
2 - DO NOT SCALE THIS DRAWING.
3 - ALL ARCHITECTURAL DWGS. MUST BE READ IN CONJUNCTION WITH STRUCTURAL & ELECTRO -MECHANICAL DRAWINGS RELATED SPECIFICATIONS.
4 - THE CONTRACTOR MUST INFORM THE ENGINEER ABOUT ANY CONTRADICTION OF ANY KIND BEFORE BEGINNING OF CONSTRUCTION.
5 - ALL MATERIALS TO BE APPROVED BY ARCHITECTS/ ENGINEERS. BEFORE PROCURING THE SAME.
6 - THE CONTRACTOR SHALL SUBMIT THE SHOP DRAWING AS PER ACTUAL SITE MEASUREMENTS FOR APPROVAL, BEFORE COMMENCING THE WORK /FABRICATION ON SITE.


Rev.No.	DESCRIPTION	DATE	CHECKED	APPROVED
1	ISSUED FOR APPROVAL	08.09.2025	T.B.M	J.K.
0	ISSUED FOR APPROVAL	16.07.2025	M.S	J.K.

PROJECT :
TOWER 26 - OUTSIDE RESTAURANT

LOCATION :
THE PEARL - QATAR

DRAWING TITLE :
ELEVATIONS & SECTION-A


DATE :	JULY 2025	SCALE	N.T.S
		DRAWN BY	K.H
DRAWING NUMBER	A-104	CHECKED BY	M.S
		JOB No.	----

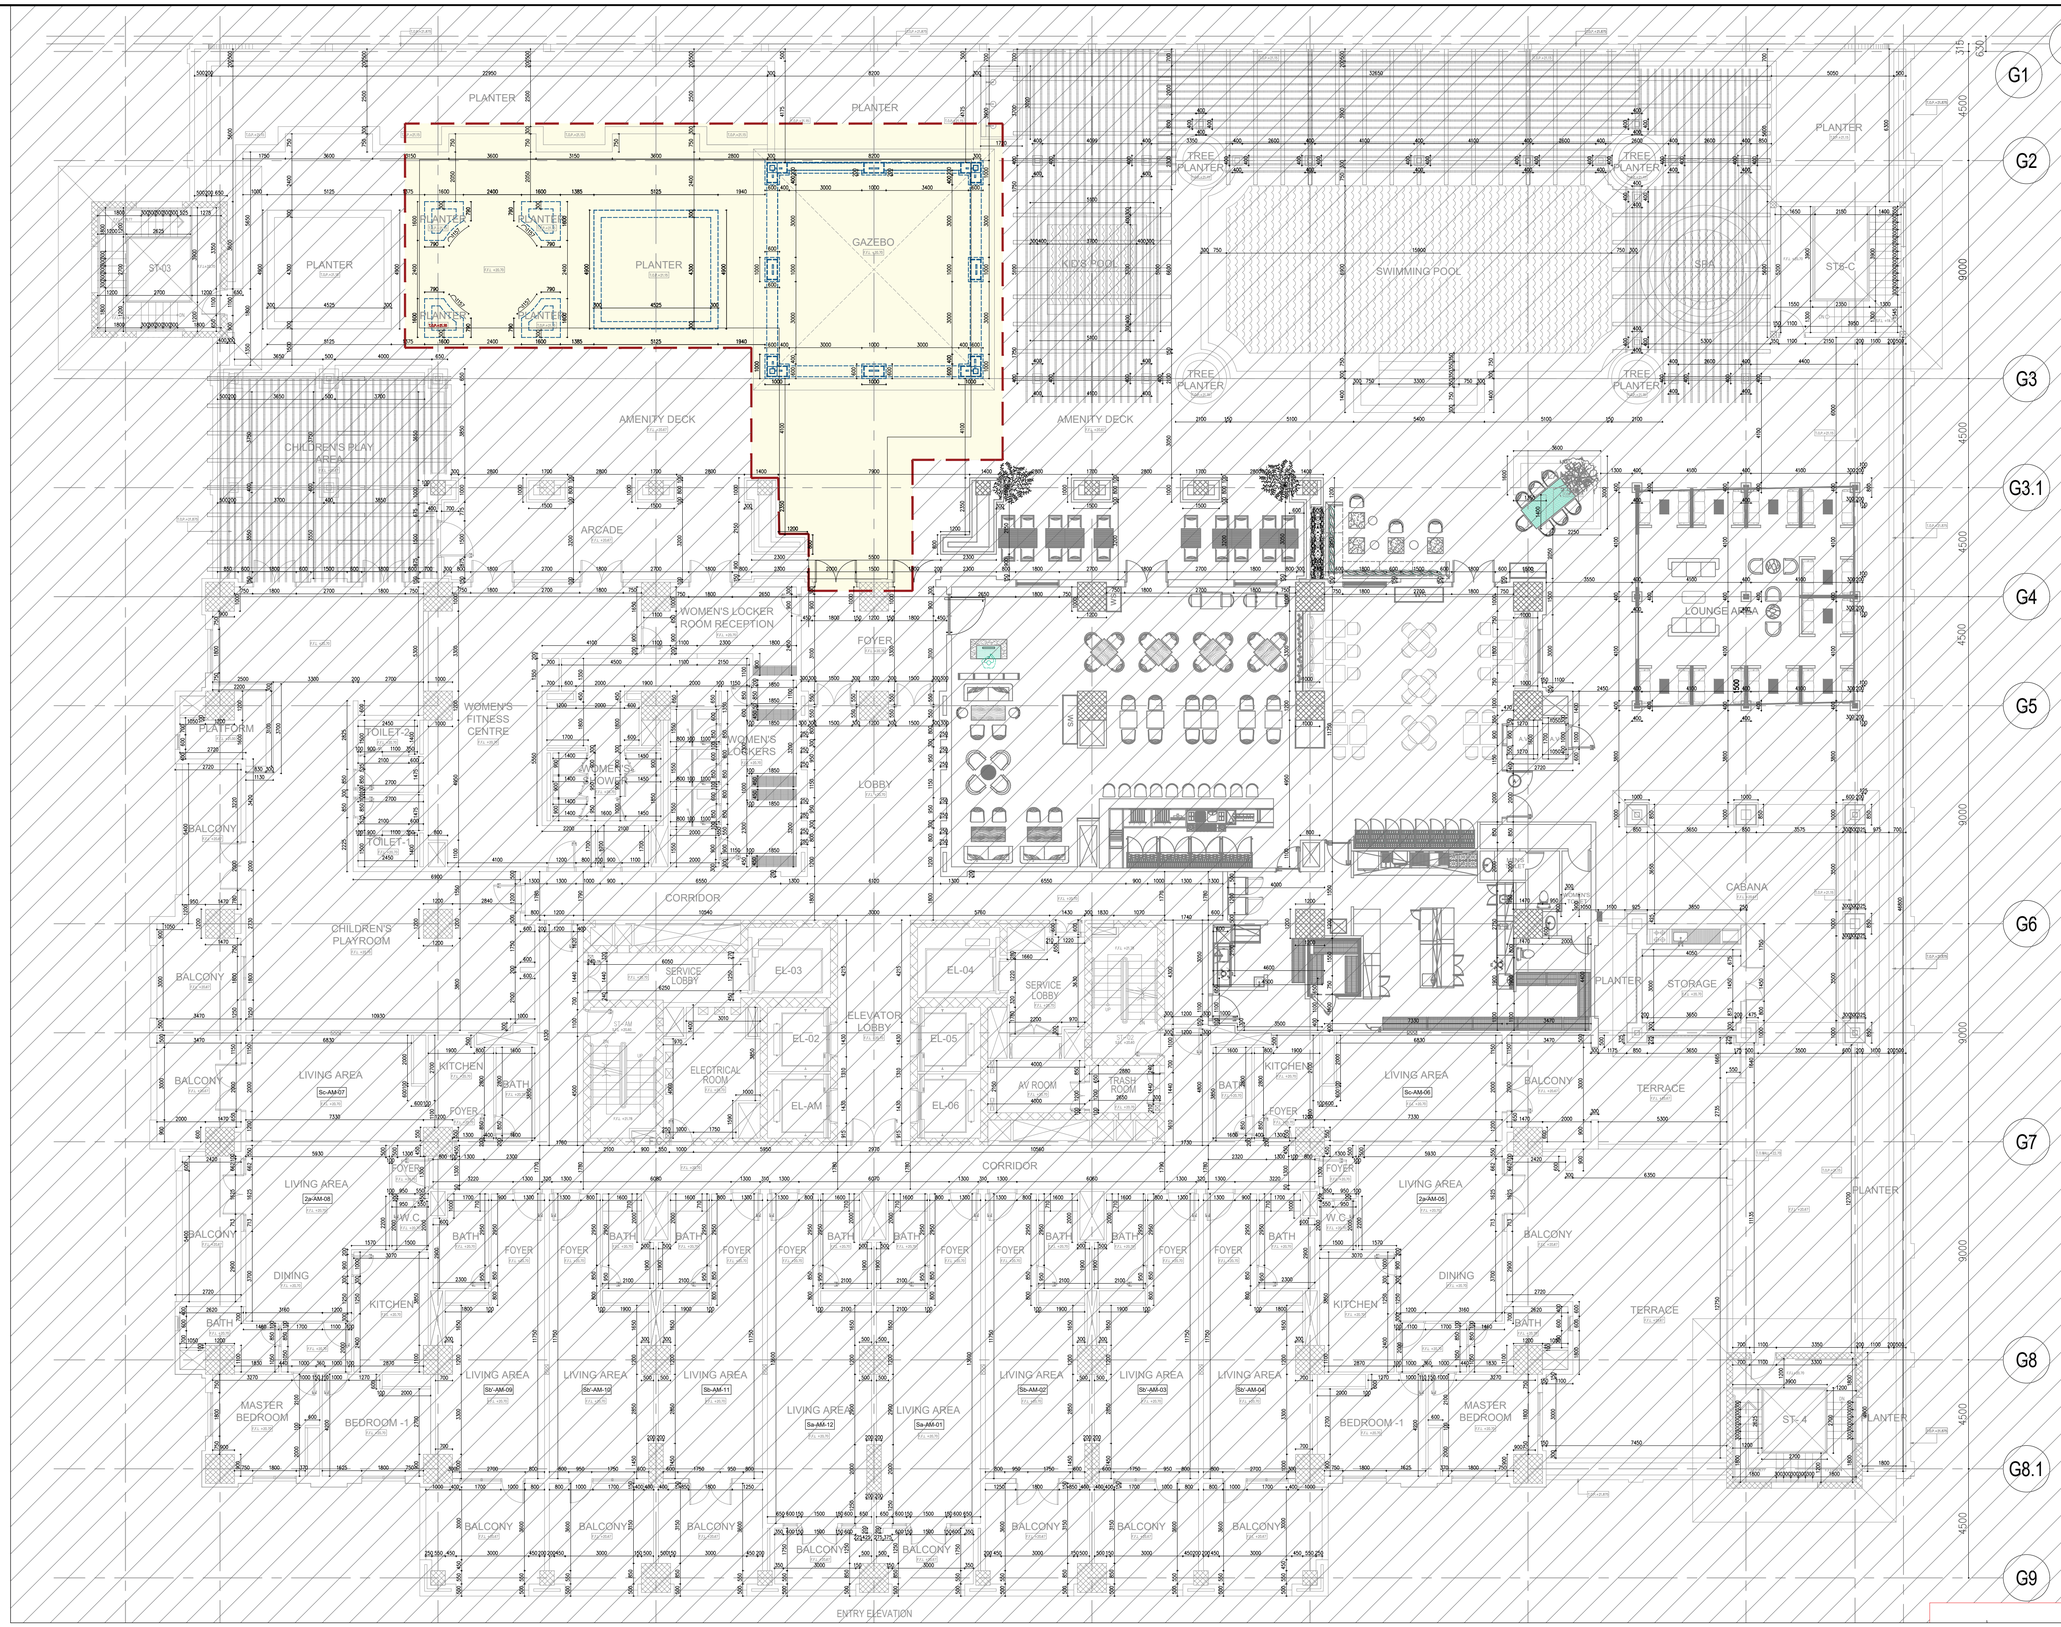

TO BE DEMOLISHED

GENERAL NOTES :

1 - ALL DIMENSIONS ARE IN METERS, LEVELS ARE IN METERS.
2 - DO NOT SCALE THIS DRAWING.
3 - ALL ARCHITECTURAL DWGS. MUST BE READ IN CONJUNCTION WITH STRUCTURAL & ELECTRO -MECHANICAL DRAWINGS RELATED SPECIFICATIONS.
4 - THE CONTRACTOR MUST INFORM THE ENGINEER ABOUT ANY CONTRADICTION OF ANY KIND BEFORE BEGINNING OF CONSTRUCTION.
5 - ALL MATERIALS TO BE APPROVED BY ARCHITECTS/ ENGINEERS. BEFORE PROCURING THE SAME.
6 - THE CONTRACTOR SHALL SUBMIT THE SHOP DRAWING AS PER ACTUAL SITE MEASUREMENTS FOR APPROVAL, BEFORE COMMENCING THE WORK /FABRICATION ON SITE.

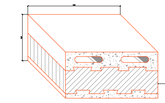

THERMO INSULATION BLOCK
FOR EXTERNAL WALL- Scale- 1:20

Rev.No.	DESCRIPTION	DATE	CHECKED	APPROVED
0	ISSUED FOR APPROVAL	03.08.2025	J.K.	J.K.

PROJECT :
TOWER 26 - OUTSIDE RESTAURANT

LOCATION :
THE PEARL - QATAR

DRAWING TITLE :
DEMOLITION PLAN


DATE :	JULY 2025	SCALE	
		DRAWN BY	K.H
DRAWING NUMBER	A-105	CHECKED BY	J.K
		JOB No.	----

PLANTER
PLANTER
GAZEBO
F.F.L +20.70
PLANTER
T.O.P.+21.15
AMENITY DECK
F.F.L +20.67
ARCADE
F.F.L +20.67

TO BE DEMOLISHED

GENERAL NOTES :

1 - ALL DIMENSIONS ARE IN METERS, LEVELS ARE IN METERS.
2 - DO NOT SCALE THIS DRAWING.
3 - ALL ARCHITECTURAL DWGS. MUST BE READ IN CONJUNCTION WITH STRUCTURAL & ELECTRO -MECHANICAL DRAWINGS RELATED SPECIFICATIONS.
4 - THE CONTRACTOR MUST INFORM THE ENGINEER ABOUT ANY CONTRADICTION OF ANY KIND BEFORE BEGINNING OF CONSTRUCTION.
5 - ALL MATERIALS TO BE APPROVED BY ARCHITECTS/ ENGINEERS. BEFORE PROCURING THE SAME.
6 - THE CONTRACTOR SHALL SUBMIT THE SHOP DRAWING AS PER ACTUAL SITE MEASUREMENTS FOR APPROVAL, BEFORE COMMENCING THE WORK /FABRICATION ON SITE.

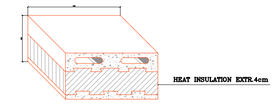

THERMO INSULATION BLOCK
FOR EXTERNAL WALL- Scale- 1:20

Rev.No.	DESCRIPTION	DATE	CHECKED	APPROVED
0	ISSUED FOR APPROVAL	03.08.2025	J.K.	J.K.

PROJECT OWNER :

MR. ALI AL MALKI

MAIN CONSULTANT :

ACG
ARCHITECTURAL CONSULTING GROUP
DOHA • QATAR
T +974 44369471
F +974 44368178
P.O.Box -18579, DOHA.

PROJECT :

TOWER 26 - OUTSIDE RESTAURANT

LOCATION :

THE PEARL - QATAR

DRAWING TITLE :

DEMOLITION PLAN

DATE :	JULY 2025	SCALE	
		DRAWN BY	K.H
DRAWING NUMBER	A-106	CHECKED BY	J.K
		JOB No.	----



GENERAL NOTES :

1 - ALL DIMENSIONS ARE IN METERS, LEVELS ARE IN METERS.
2 - DO NOT SCALE THIS DRAWING.
3 - ALL ARCHITECTURAL DWGS. MUST BE READ IN CONJUNCTION WITH STRUCTURAL & ELECTRO -MECHANICAL DRAWINGS RELATED SPECIFICATIONS.
4 - THE CONTRACTOR MUST INFORM THE ENGINEER ABOUT ANY CONTRADICTION OF ANY KIND BEFORE BEGINNING OF CONSTRUCTION.
5 - ALL MATERIALS TO BE APPROVED BY ARCHITECTS/ ENGINEERS. BEFORE PROCURING THE SAME.
6 - THE CONTRACTOR SHALL SUBMIT THE SHOP DRAWING AS PER ACTUAL SITE MEASUREMENTS FOR APPROVAL, BEFORE COMMENCING THE WORK /FABRICATION ON SITE.

1	ISSUED FOR APPROVAL	08.09.2025	T.B.M	J.K.
0	ISSUED FOR APPROVAL	16.07.2025	M.S	J.K.
Rev.No.	DESCRIPTION	DATE	CHECKED	APPROVED

PROJECT :

TOWER 26 - OUTSIDE RESTAURANT


LOCATION :

THE PEARL - QATAR

DRAWING TITLE :

INTERNAL VIEW- 01

DATE :	JULY 2025	SCALE	N.T.S
		DRAWN BY	K.H
DRAWING NUMBER	A-200	CHECKED BY	M.S
		JOB No.	----

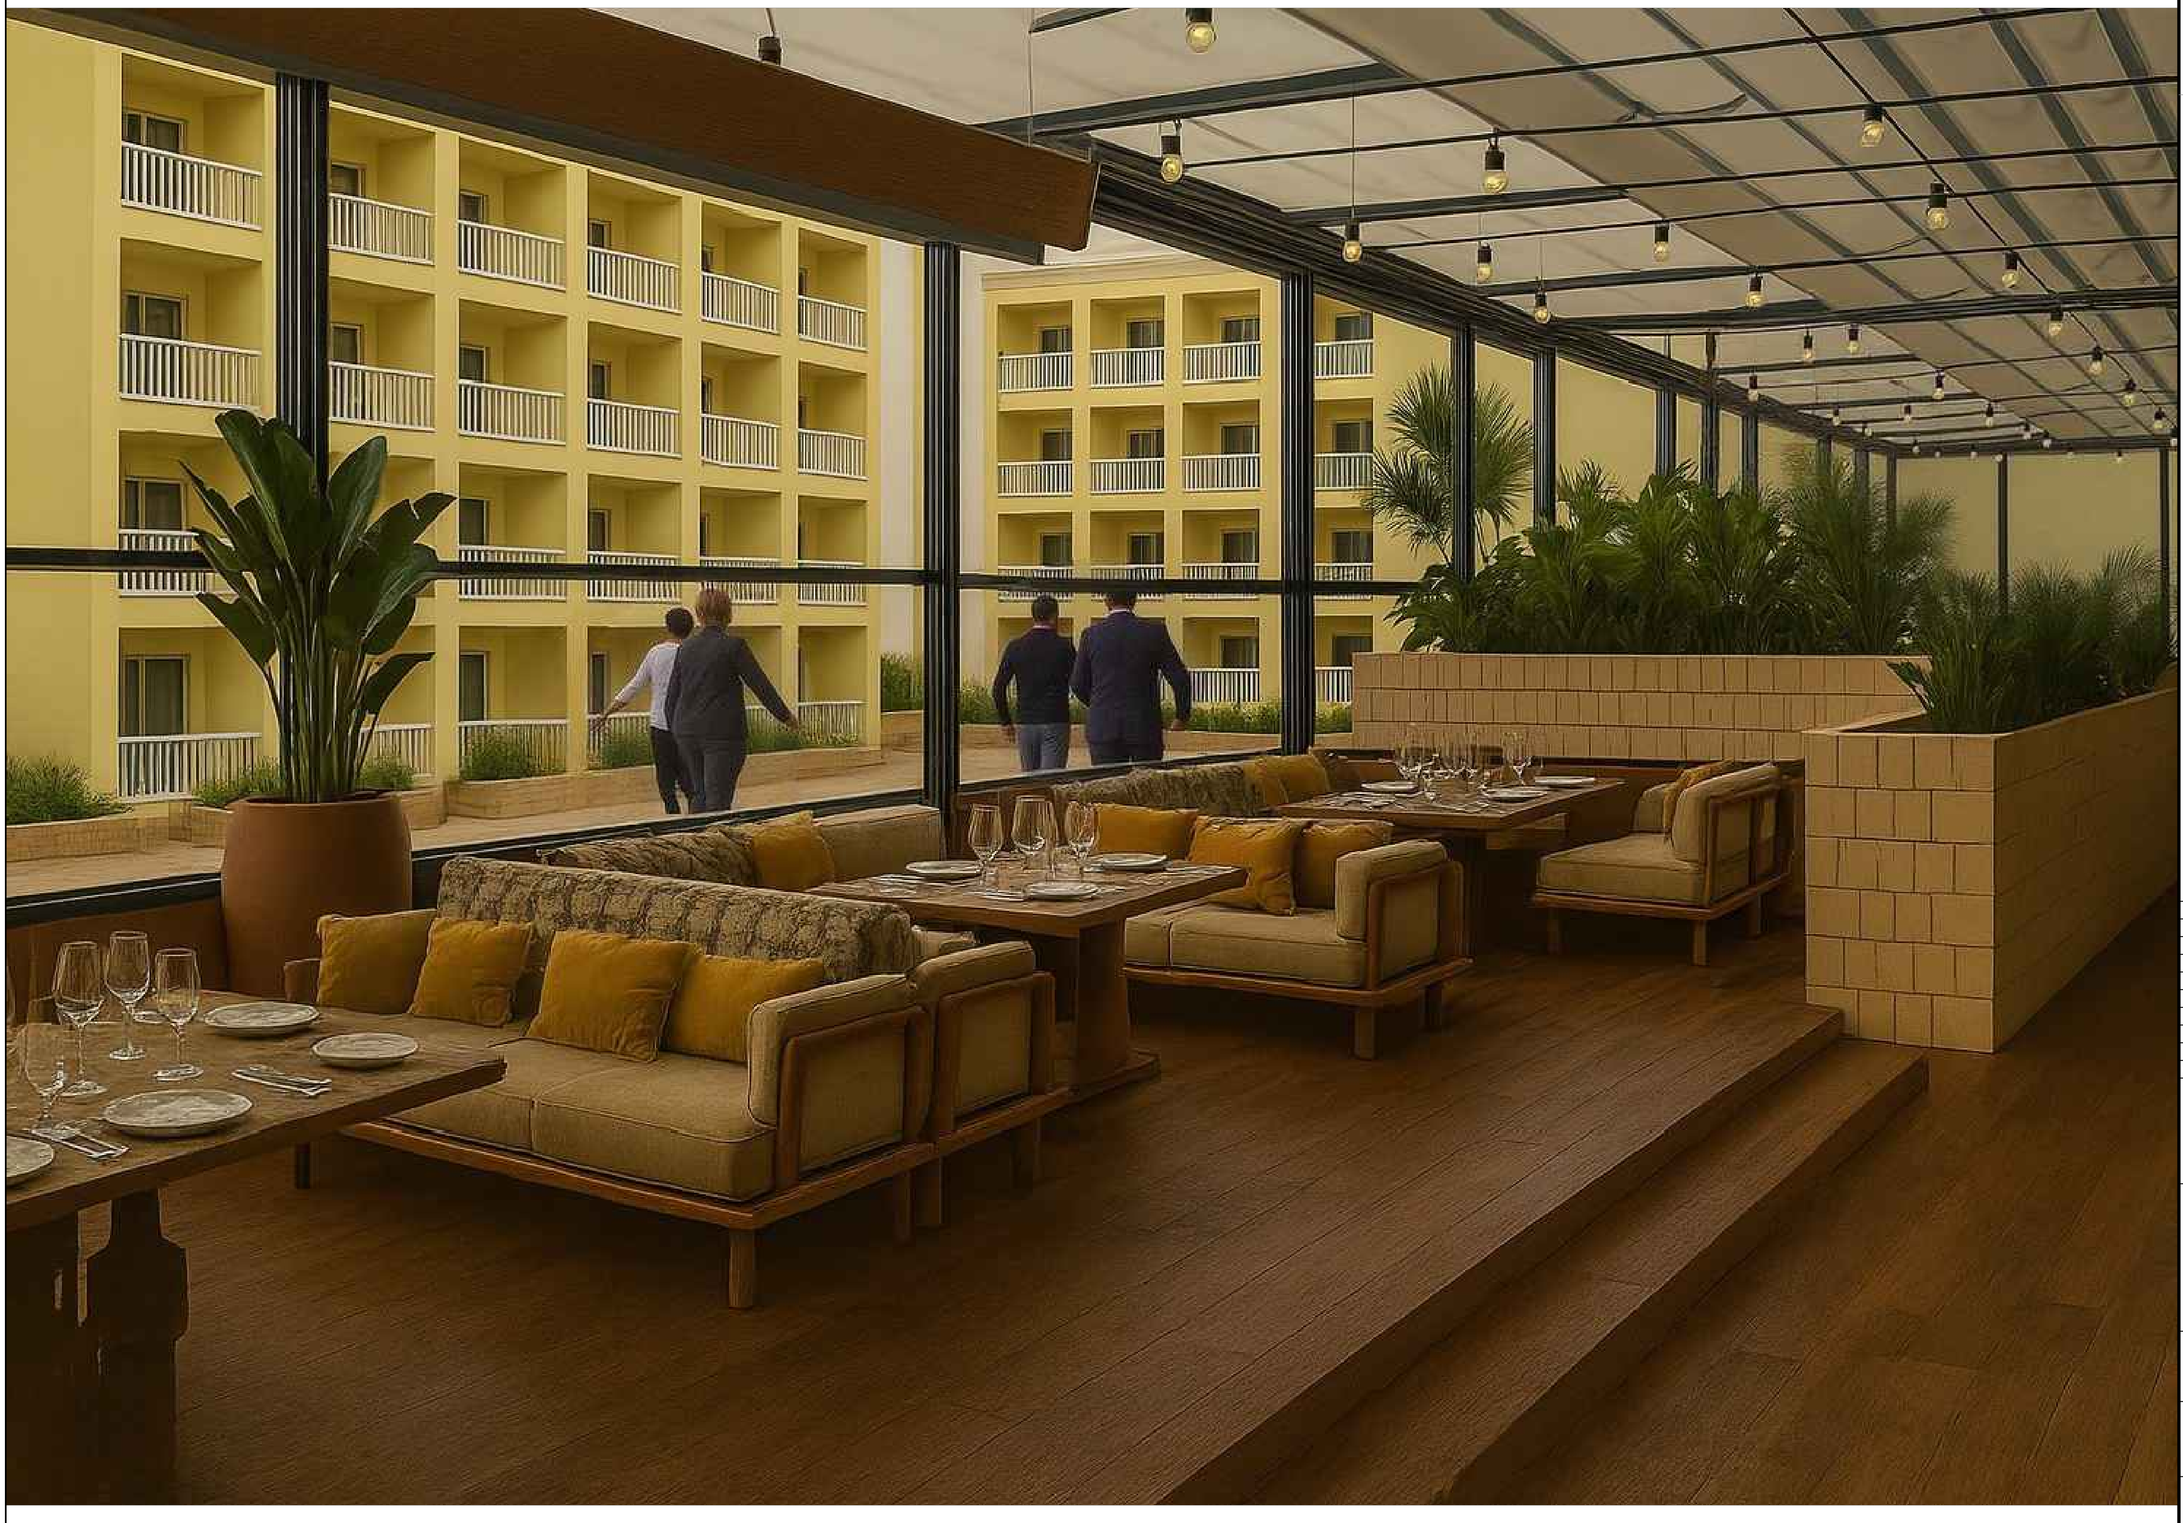

GENERAL NOTES :

1 - ALL DIMENSIONS ARE IN METERS, LEVELS ARE IN METERS.
2 - DO NOT SCALE THIS DRAWING.
3 - ALL ARCHITECTURAL DWGS. MUST BE READ IN CONJUNCTION WITH STRUCTURAL & ELECTRO -MECHANICAL DRAWINGS RELATED SPECIFICATIONS.
4 - THE CONTRACTOR MUST INFORM THE ENGINEER ABOUT ANY CONTRADICTION OF ANY KIND BEFORE BEGINNING OF CONSTRUCTION.
5 - ALL MATERIALS TO BE APPROVED BY ARCHITECTS/ ENGINEERS. BEFORE PROCURING THE SAME.
6 - THE CONTRACTOR SHALL SUBMIT THE SHOP DRAWING AS PER ACTUAL SITE MEASUREMENTS FOR APPROVAL, BEFORE COMMENCING THE WORK /FABRICATION ON SITE.

Rev.No.	DESCRIPTION	DATE	CHECKED	APPROVED
1	ISSUED FOR APPROVAL	08.09.2025	T.B.M	J.K.
0	ISSUED FOR APPROVAL	16.07.2025	M.S	J.K.

PROJECT OWNER :

PROJECT :

TOWER 26 - OUTSIDE RESTAURANT

LOCATION :

THE PEARL - QATAR

DRAWING TITLE :

INTERNAL VIEW- 02

DATE :	JULY 2025	SCALE	N.T.S
		DRAWN BY	K.H
DRAWING NUMBER	A-201	CHECKED BY	M.S
		JOB No.	----



GENERAL NOTES :

1 - ALL DIMENSIONS ARE IN METERS, LEVELS ARE IN METERS.
2 - DO NOT SCALE THIS DRAWING.
3 - ALL ARCHITECTURAL DWGS. MUST BE READ IN CONJUNCTION WITH STRUCTURAL & ELECTRO -MECHANICAL DRAWINGS RELATED SPECIFICATIONS.
4 - THE CONTRACTOR MUST INFORM THE ENGINEER ABOUT ANY CONTRADICTION OF ANY KIND BEFORE BEGINNING OF CONSTRUCTION.
5 - ALL MATERIALS TO BE APPROVED BY ARCHITECTS/ ENGINEERS. BEFORE PROCURING THE SAME.
6 - THE CONTRACTOR SHALL SUBMIT THE SHOP DRAWING AS PER ACTUAL SITE MEASUREMENTS FOR APPROVAL, BEFORE COMMENCING THE WORK /FABRICATION ON SITE.

Rev.No.	DESCRIPTION	DATE	CHECKED	APPROVED
1	ISSUED FOR APPROVAL	08.09.2025	T.B.M	J.K.
0	ISSUED FOR APPROVAL	16.07.2025	M.S	J.K.

PROJECT OWNER :

MAIN

PROJECT :

TOWER 26 - OUTSIDE RESTAURANT

LOCATION :

THE PEARL - QATAR

DRAWING TITLE :

INTERNAL VIEW- 03

DATE :	JULY 2025	SCALE	N.T.S
		DRAWN BY	K.H
DRAWING NUMBER	A-202	CHECKED BY	M.S
		JOB No.	----



GENERAL NOTES :

1 - ALL DIMENSIONS ARE IN METERS, LEVELS ARE IN METERS.
2 - DO NOT SCALE THIS DRAWING.
3 - ALL ARCHITECTURAL DWGS. MUST BE READ IN CONJUNCTION WITH STRUCTURAL & ELECTRO -MECHANICAL DRAWINGS RELATED SPECIFICATIONS.
4 - THE CONTRACTOR MUST INFORM THE ENGINEER ABOUT ANY CONTRADICTION OF ANY KIND BEFORE BEGINNING OF CONSTRUCTION.
5 - ALL MATERIALS TO BE APPROVED BY ARCHITECTS/ ENGINEERS. BEFORE PROCURING THE SAME.
6 - THE CONTRACTOR SHALL SUBMIT THE SHOP DRAWING AS PER ACTUAL SITE MEASUREMENTS FOR APPROVAL, BEFORE COMMENCING THE WORK /FABRICATION ON SITE.

Rev.No.	DESCRIPTION	DATE	CHECKED	APPROVED
1	ISSUED FOR APPROVAL	08.09.2025	T.B.M	J.K.
0	ISSUED FOR APPROVAL	16.07.2025	M.S	J.K.

PROJECT OWNER :

MAIN CONSUL"

PROJECT :

TOWER 26 - OUTSIDE RESTAURANT

LOCATION :

THE PEARL - QATAR

DRAWING TITLE :

INTERNAL VIEW- 04

DATE :	JULY 2025	SCALE	N.T.S
		DRAWN BY	K.H
DRAWING NUMBER	A-203	CHECKED BY	M.S
		JOB No.	----



GENERAL NOTES :

1 - ALL DIMENSIONS ARE IN METERS, LEVELS ARE IN METERS.
2 - DO NOT SCALE THIS DRAWING.
3 - ALL ARCHITECTURAL DWGS. MUST BE READ IN CONJUNCTION WITH STRUCTURAL & ELECTRO -MECHANICAL DRAWINGS RELATED SPECIFICATIONS.
4 - THE CONTRACTOR MUST INFORM THE ENGINEER ABOUT ANY CONTRADICTION OF ANY KIND BEFORE BEGINNING OF CONSTRUCTION.
5 - ALL MATERIALS TO BE APPROVED BY ARCHITECTS/ ENGINEERS. BEFORE PROCURING THE SAME.
6 - THE CONTRACTOR SHALL SUBMIT THE SHOP DRAWING AS PER ACTUAL SITE MEASUREMENTS FOR APPROVAL, BEFORE COMMENCING THE WORK /FABRICATION ON SITE.

1	ISSUED FOR APPROVAL	08.09.2025	T.B.M	J.K.
0	ISSUED FOR APPROVAL	16.07.2025	M.S	J.K.
Rev.No.	DESCRIPTION	DATE	CHECKED	APPROVED

PROJECT OWNER :

MAIN CON

PROJECT :

TOWER 26 - OUTSIDE RESTAURANT

LOCATION :

THE PEARL - QATAR

DRAWING TITLE :

INTERNAL VIEW- 05

DATE :	JULY 2025	SCALE	N.T.S
		DRAWN BY	K.H
DRAWING NUMBER	A-204	CHECKED BY	M.S
		JOB No.	----

GENERAL NOTES :

1 - ALL DIMENSIONS ARE IN METERS, LEVELS ARE IN METERS.
2 - DO NOT SCALE THIS DRAWING.
3 - ALL ARCHITECTURAL DWGS. MUST BE READ IN CONJUNCTION WITH STRUCTURAL & ELECTRO -MECHANICAL DRAWINGS RELATED SPECIFICATIONS.
4 - THE CONTRACTOR MUST INFORM THE ENGINEER ABOUT ANY CONTRADICTION OF ANY KIND BEFORE BEGINNING OF CONSTRUCTION.
5 - ALL MATERIALS TO BE APPROVED BY ARCHITECTS/ ENGINEERS. BEFORE PROCURING THE SAME.
6 - THE CONTRACTOR SHALL SUBMIT THE SHOP DRAWING AS PER ACTUAL SITE MEASUREMENTS FOR APPROVAL, BEFORE COMMENCING THE WORK /FABRICATION ON SITE.

0	ISSUED FOR APPROVAL	08.09.2025	T.B.M	J.K.
Rev.No.	DESCRIPTION	DATE	CHECKED	APPROVED

PROJECT OWNER :

MAIN CONSU

PROJECT :

TOWER 26 - OUTSIDE RESTAURANT

LOCATION :

THE PEARL - QATAR

DRAWING TITLE :

DRAINAGE LAYOUT H/L

DATE :	JULY 2025	SCALE	N.T.S
		DRAWN BY	K.H
DRAWING NUMBER	A-300	CHECKED BY	M.S
		JOB No.	----

GENERAL NOTES :

1 - ALL DIMENSIONS ARE IN METERS, LEVELS ARE IN METERS.
2 - DO NOT SCALE THIS DRAWING.
3 - ALL ARCHITECTURAL DWGS. MUST BE READ IN CONJUNCTION WITH STRUCTURAL & ELECTRO -MECHANICAL DRAWINGS RELATED SPECIFICATIONS.
4 - THE CONTRACTOR MUST INFORM THE ENGINEER ABOUT ANY CONTRADICTION OF ANY KIND BEFORE BEGINNING OF CONSTRUCTION.
5 - ALL MATERIALS TO BE APPROVED BY ARCHITECTS/ ENGINEERS. BEFORE PROCURING THE SAME.
6 - THE CONTRACTOR SHALL SUBMIT THE SHOP DRAWING AS PER ACTUAL SITE MEASUREMENTS FOR APPROVAL, BEFORE COMMENCING THE WORK /FABRICATION ON SITE.

Rev.No.	DESCRIPTION	DATE	CHECKED	APPROVED
0	ISSUED FOR APPROVAL	08.09.2025	T.B.M	J.K.

PROJECT OWNER :

MAIN CONSU

P.O.Bo 18579, DO A.

PROJECT :

TOWER 26 - OUTSIDE RESTAURANT

LOCATION :

THE PEARL - QATAR

DRAWING TITLE :

IRRIGATION LAYOUT U/T

DATE :	JULY 2025	SCALE	N.T.S
		DRAWN BY	K.H
DRAWING NUMBER	A-301	CHECKED BY	M.S
		JOB No.	----