

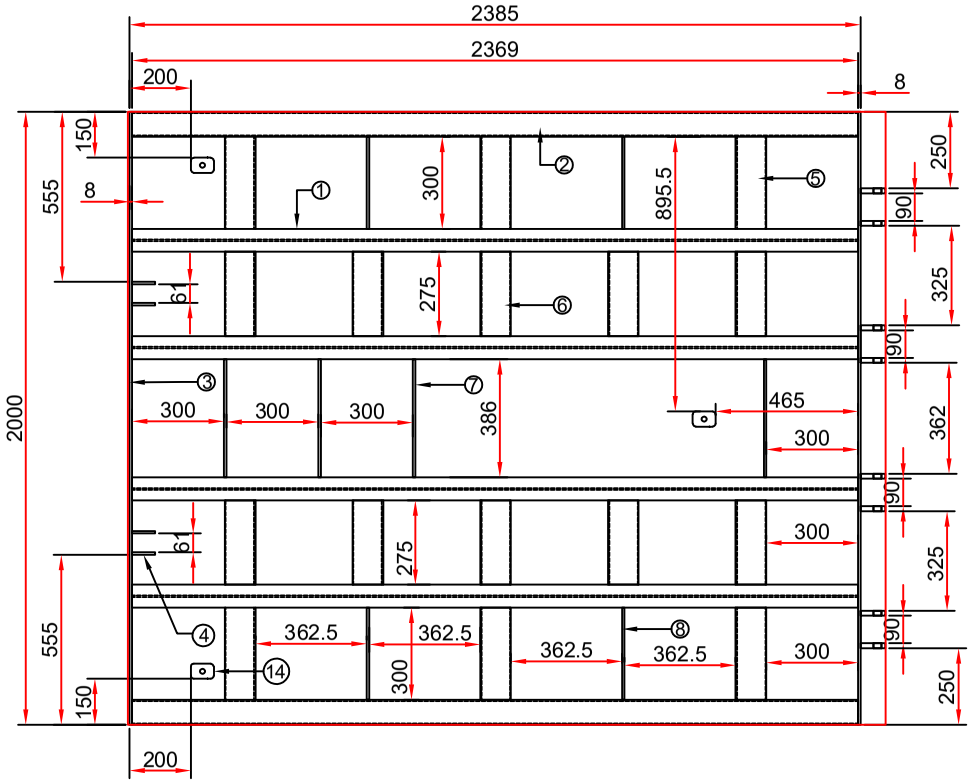


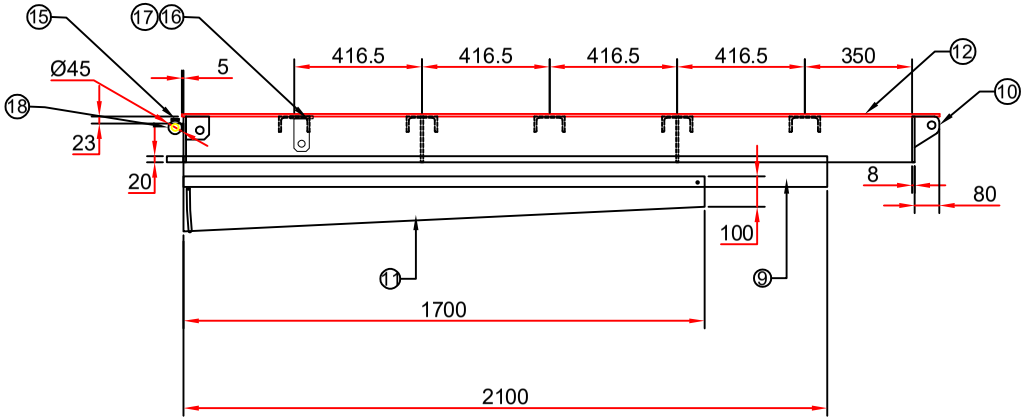

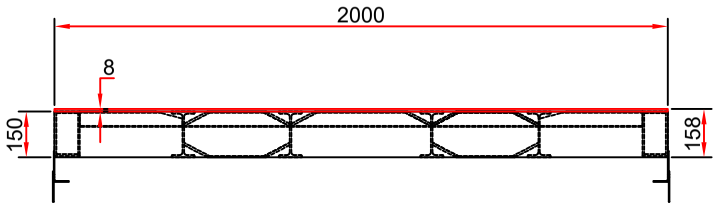

BOM			
SL NO.	DESCRIPTION	SPECIFICATION	QTY
1	ISMB	150X75X2369L	4NOS
2	MS RECT.TUBE	145X82X2369X4.8THK	2NOS
3	MS FLAT	150X8X2000L	2NOS
4	CYLINDER MTG BKT	75X75X8THK	4NOS
5	C CHANNEL	100X50x5X300L	6NOS
6	C CHANNEL	100X50x5X275L	10NOS
7	MS FLAT	100X8X386L	4NOS
8	MS FLAT	100X8X300L	4NOS
9	L BEND	100X2100X1.6THK	2NOS
10	HOLDING BKT	100X80X16THK	8NOS
11	SIDE COVER	180X1700X1.6THK	2NOS
12	CHEQ.SHEET	2471X2000X8THK	1NO
13	EYE BOLT	M16XSTD WITH NUT	3NOS
14	EYE BOLT MTNG BKT	50X75X16	3NOS
15	MS FLAT	25X5X100	20NOS
16	MS BRACKET	50X106X8	2NOS
17	MS FLAT	75X10X115	2NOS
18	MS BUSH	OD45X26ID	20NOS
19	BRIGHT BAR	24DIAX1600MM	1NO
20	LIP PLATE	2000X400X16	1NO
21	ROUND BAR	Ø20X55L	2NOS
22	BRIGHT BAR	24DIAX2300MM	1NO

This drawing & design is the property of NIHVA TECHNOLOGIES. Not to be sold or copied to any other concern.

TITLE: DECK FRAME

NIHVA TECHNOLOGIES PVT. LTD.

	NAME	DATE
DRAWN	SUJATA	17/04/2023
CHECK		
APPRD.		

If any queries contact : design1@nihva.com

ALL DIMENSION ARE IN mm

PRODUCT - DOCK LEVELER

DWG NO:-NIHVA/22-23/MFG/0111 REV- 0

SCALE: NTS SCALE:-- 1:1 SHEET: 01 OF 01

Rev No.	Revision	Date	Revised By