


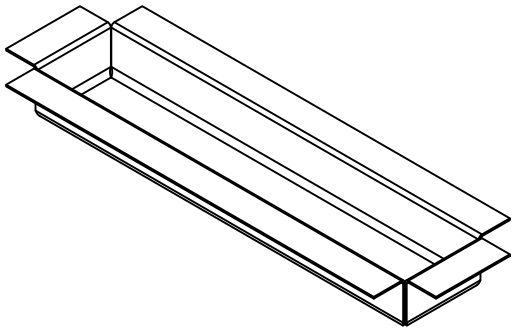
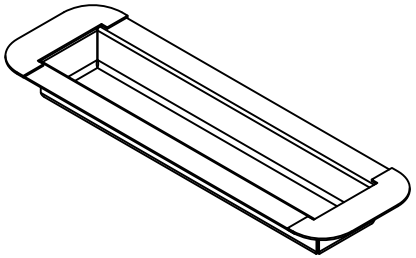


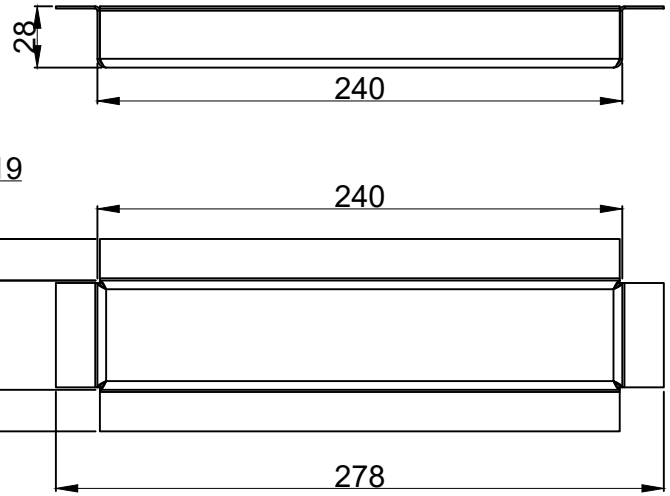

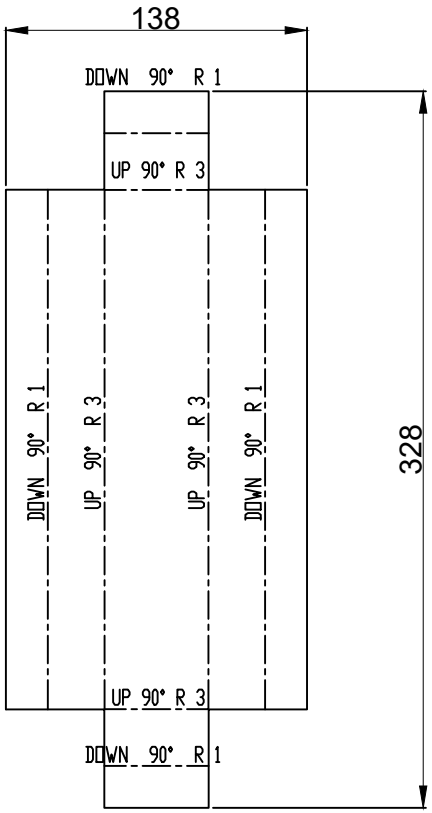


QTY . 25 NOS.

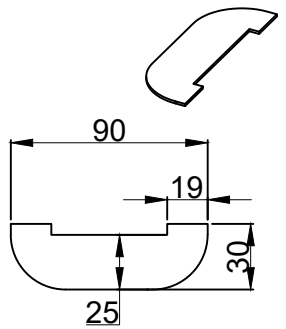


QTY . 50 NOS.

SS SHEET 1.2 MM

| REV. | REVISION DESCRIPTION | Date | Revised By |
|---|---|---|---|
| | | | |
| 000 | RELEASED FOR PRODUCTION | 23/05/2022 | MAHESH S. |
| | | | |
| | | | |

This drawing & design is the property of NIHVA TECHNOLOGIES. Not to be sold or copied to any other concern.

TITLE:- SS HANDLE CRM DOOR

NIHVA TECHNOLOGIES PVT. LTD. PUNE
Tel : 020 66304033
Email:- info@nihva.com
Website:- www.nihva.com

| | NAME | DATE | SIGN |
|---|---|---|---|
| DRAWN | M.SUTAR | 23/05/2022 | |
| CHECK | M.SUTAR | 23/05/2022 | |
| APPRD. | | | |

If any queries contact : design@nihva.com

ALL DIMENSION ARE IN mm

CLIENT - NIHVA TECHNOLOGIES PVT.LTD

LOCATION -

PRODUCT - SLIDING DOOR - PPGI CLADDING

DWG NO:-NIHVA/22-23/VDR/0015 REV- 0

SCALE: NTS SCALE:-- 1:1 SHEET: 02 OF 02