

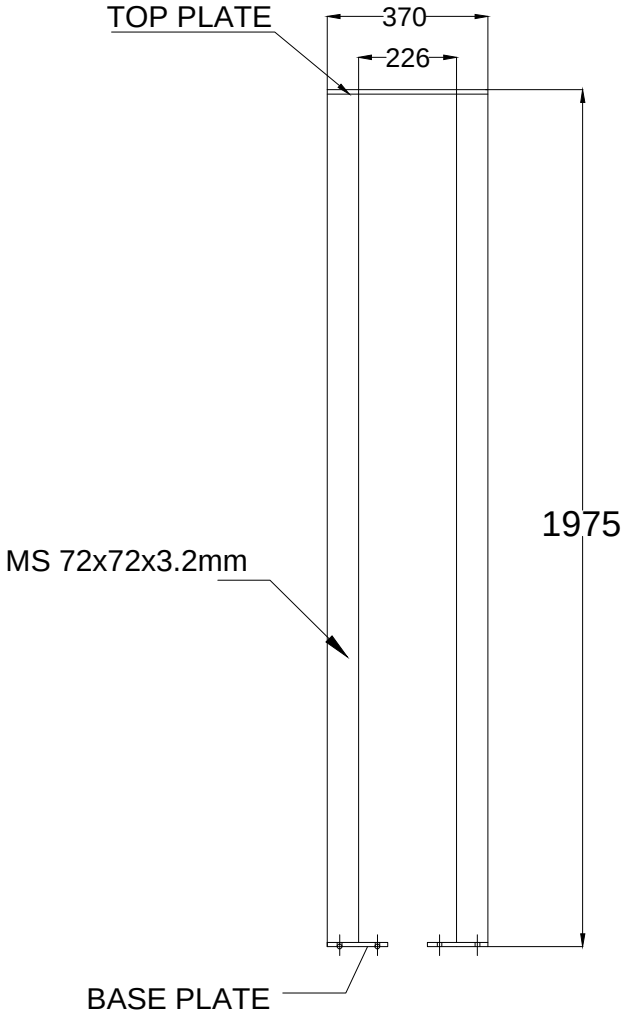


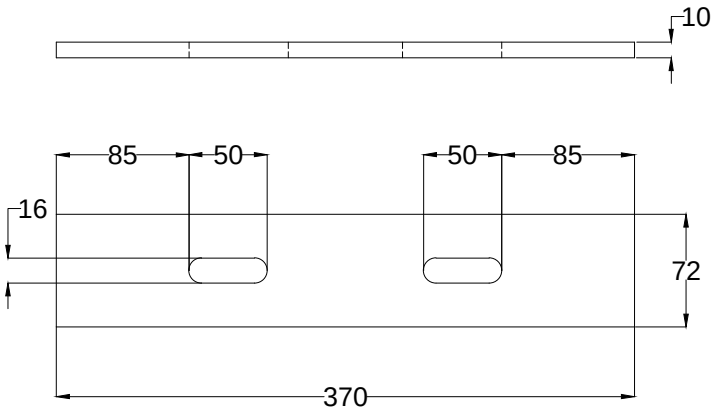

TOP PLATE


MATERIAL:-MS
THICKNESS:-10mm
QTY:- 09NOS

MATERIAL:-MS
QTY:- 09NOS

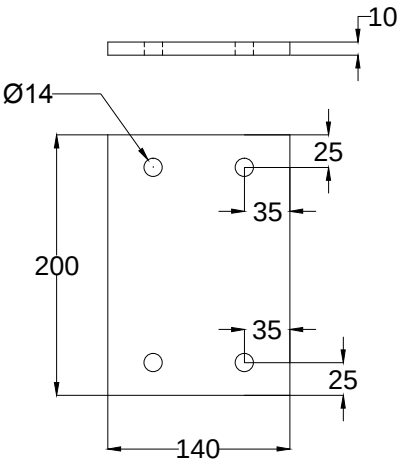

BASE PLATE

MATERIAL:-MS
THICKNESS:-10mm
QTY:- 18 NOS

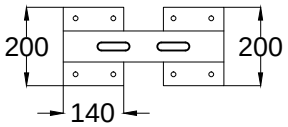

POST

NOTE:-ALL PLATE SHOULD BE LASER CUTTING

SR NO	TUBE SPECIFICATION		MATERIAL	SIZE
1	72X72X3.2mm MS TUBE	POST	MILD STEEL	1.955MTR- 18NOS
2	370X72X10mm MS PLATE	TOP PLATE	MILD STEEL	370X72X10mm- 09NOS
3	200X140X10mm MS PLATE	BOTTOM PLATE	MILD STEEL	140X200X10mm- 18NOS

This drawing & designing is the property of NIHVA TECHNOLOGIES. Not to be sold or copied to any other concern.

TITLE: SLIDING GATE POST DRAWING

NIHVA TECHNOLOGIES PVT. LTD.

NIHVA TECHNOLOGIES PVT. LTD. PUNE
Tel : 020 66304033
Email:- info@nihva.com
Website:- www.nihva.com

	Name	SIGN	DATE
DRAWN	SURAJ		05/12/18
CHECK	PRADEEP		05/12/18
APPROVAL	R.D		05/12/18

CLIENT -

PROJECT -

SITE LOCATION -MODINAGAR,UTTAR PRADESH.

If any queries contact : design@nihva.com

DWG. NO. : NIHVA/18-19/VDR/248 REV.:- 0

ALL DIMENSION ARE IN mm

SCALE: NTS WT: SHEET: 01 OF 01